

A0.0

CC BY Attribution Share-Alike by Jay Osborne. These drawings are for informational purposes only. This design and its related documents are provided "as is" with no guarantees or warranties, express or implied. FreeFarmhouse & Jay Osborne disclaim liability for any damages that may result from using this work.

PROJECT INFORMATION

LOCATION

54321 EXAMPLE AVENUE
NOWHERE, NC 12345

PROJECT DESCRIPTION

ADU OR SINGLE-FAMILY HOUSE

PROJECT NUMBER

APN 0000-0000-000-000

FLOOR AREA

1ST FLOOR: CORE: 384 SQUARE FEET
"ADDITIONS" (ALL): 191 SQUARE FEET
TOTAL FLOOR 1 AREA: 575 SQUARE FEET
2ND FLOOR: CORE: 346 SQUARE FEET

TOTAL FLOOR AREA: 923 SQUARE FEET

CONSTRUCTION TYPE

TYPE V - WOOD FRAME CONSTRUCTION

PARCEL SIZE

[RECOMMENDED: AT LEAST 50 FEET BY 60 FEET]


APPLICABLE CODES

2022 EXAMPLE STATE BUILDING CODE

PRESENTATION PLANS



CAROLINE

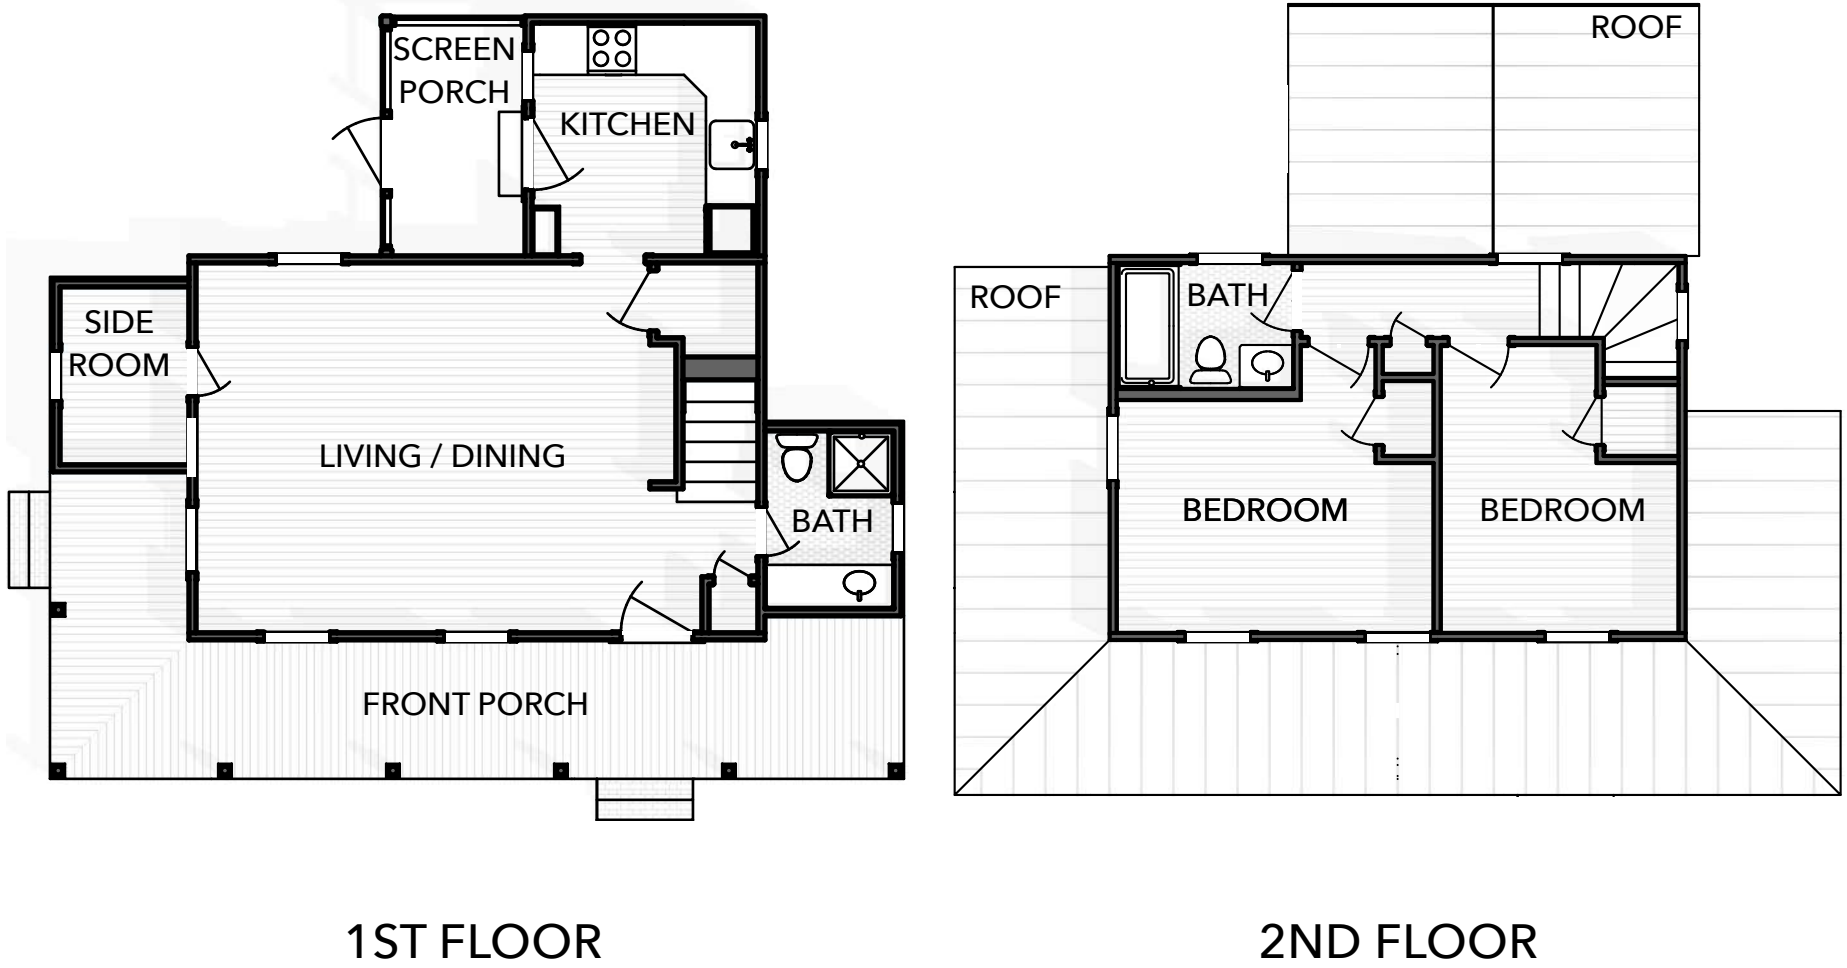

CONTACT INFORMATION

OWNER

NAME
PHONE NUMBER
EMAIL ADDRESS
NOTES
STREET ADDRESS
CITY / STATE / ZIP

ARCHITECT (OR DESIGNER OF RECORD)

CONTACT PERSON
PHONE NUMBER
EMAIL ADDRESS
NOTES
COMPANY NAME
STREET ADDRESS
CITY / STATE / ZIP

GENERAL CONTRACTOR

CONTACT PERSON
PHONE NUMBER
EMAIL ADDRESS
NOTES
COMPANY NAME
STREET ADDRESS
CITY / STATE / ZIP

SURVEYOR

CONTACT PERSON
PHONE NUMBER
EMAIL ADDRESS
NOTES
COMPANY NAME
STREET ADDRESS
CITY / STATE / ZIP

PLUMBING

CONTACT PERSON
PHONE NUMBER
EMAIL ADDRESS
NOTES
COMPANY NAME
STREET ADDRESS
CITY / STATE / ZIP

MECHANICAL (AND/OR ELECTRICAL)

CONTACT PERSON
PHONE NUMBER
EMAIL ADDRESS
NOTES
COMPANY NAME
STREET ADDRESS
CITY / STATE / ZIP

STRUCTURAL

CONTACT PERSON
PHONE NUMBER
EMAIL ADDRESS
NOTES
COMPANY NAME
STREET ADDRESS
CITY / STATE / ZIP

LANDSCAPE

CONTACT PERSON
PHONE NUMBER
EMAIL ADDRESS
NOTES
COMPANY NAME
STREET ADDRESS
CITY / STATE / ZIP

INTERIORS

CONTACT PERSON
PHONE NUMBER
EMAIL ADDRESS
NOTES
COMPANY NAME
STREET ADDRESS
CITY / STATE / ZIP

PROJECT HISTORY & CREDITS

- 2023-01-04
- 1 STARTER FARMHOUSE SCHEMATIC DESIGNS
PRESENT DIGITAL MODELS TESTING THE FIRST FOUR VARIATIONS.
- 2023-10-01
- 2 CAROLINE: 1ST DRAFT OF PLAN DRAWINGS
JAY OSBORNE CREATES DETAILED DRAWINGS FOR PATREON.
- 2025-08-08
- 3 CAROLINE: ORIGINAL DESIGN (FINISHED PLANS)
ADDED DETAILS PAGES – THANKS TO KICKSTARTER SUPPORTERS

NOTES:

1. ALL WORK SO FAR IS BY JAY OSBORNE. SEE GENERAL NOTES (SHEET A0.2, SECTION 9) FOR INFORMATION ABOUT ATTRIBUTION AND THE OPEN SOURCE LICENSE.

2. THESE ARCHITECTURAL DRAWINGS ARE ONLY A TEMPLATE. FOR IT TO BE BUILT, THE DESIGN MUST BE ADAPTED TO LOCAL NEEDS & REQUIREMENTS. TO DO THIS, YOU CAN CUSTOMIZE THE SOURCE FILES (WHICH ARE FREE TO DOWNLOAD) AT FREEFARMHOUSE.COM.

3. THIS IS PART OF JAY OSBORNE'S "STARTER FARMHOUSE PROJECT". THE FIRST DESIGNS INCLUDE VIRGINIA, GEORGIA, CAROLINE, AND MARILYN. ON PATREON.COM/FREEFARMHOUSE, YOU CAN ALSO GET EARLY ACCESS TO DELAWARE'S, OREGON'S, AND PENNY & SYLVIA'S FARMHOUSE– AND MANY MORE DESIGNS STILL TO COME.



OPEN-SOURCE ARCHITECTURAL DRAWINGS
You may share, copy, and customize these blueprints.
License: [www.CreativeCommons.org/licenses/BY-SA/4.0](https://creativecommons.org/licenses/by-sa/4.0/)
Some rights reserved. No promises or guarantees given.
Download the free files at www.FreeFarmhouse.com

A DESIGN BY JAY OSBORNE
CAROLINE'S FARMHOUSE
THE ORIGINAL STARTER FARMHOUSE PLANS

- 3 2025-08-08 ORIGINAL DESIGN (FINISHED PLANS)
2 2023-10-01 CAROLINE: BLUEPRINTS ON PATREON
1 2023-01-04 STARTER FARMHOUSE SCHEMATICS
- + See A0.1 for more project history and credits

PROJECT INFO
A0.1

GENERAL NOTES

1A – WORK SHALL CONFORM TO ALL APPLICABLE CODES AND ORDINANCES, INCLUDING BUT NOT LIMITED TO BUILDING, PLUMBING, ELECTRICAL, AND MECHANICAL CODES.

1B – ANY ERRORS, OMISSIONS, OR CONFLICTS FOUND IN THESE DRAWINGS SHALL BE BROUGHT TO THE ATTENTION OF THE OWNER OR THEIR REPRESENTATIVE BEFORE PROCEEDING WITH THE WORK.

1C – IF PRINTING FULL-SIZE DRAWING SET, DO NOT SCALE DRAWINGS.

1D – WRITTEN DIMENSIONS TAKE PRECEDENCE OVER MEASUREMENTS.

~~**1E** – METRIC DIMENSIONS DO NOT PRECISELY MATCH IMPERIAL DIMS (AS DRAWN) DUE TO DIFFERING CODES AND MODULAR STANDARDS. IF ACCURACY IS DOUBTED, IMPERIAL DIMENSIONS TAKE PRECEDENCE.~~

1F – DIMENSIONS ARE TAKEN FROM FACE OF FRAMING LUMBER, FACE OF CONCRETE/ MASONRY, CENTER/FACE OF COLUMN, AND CENTERLINE OF FIXTURE, UNLESS OTHERWISE NOTED.

1G – ALL DIMENSIONS NOTED "VERIFY IN FIELD" (V.I.F.) SHALL BE MEASURED BY THE CONTRACTOR PRIOR TO CONSTRUCTION. REPORT ANY DISCREPANCIES TO THE OWNER OR THEIR REPRESENTATIVE.

1H – ALL NOTES AND DETAILS ARE TYPICAL. SIMILAR NOTES, DETAILS, AND DIMENSIONS APPLY IN SIMILAR SITUATIONS.

1I – IN THE CASE OF DISCREPANCIES WITHIN DESCRIPTIONS OF SIMILAR ITEMS, PRECEDENCE SHALL BE GIVEN TO NOTES AND DRAWINGS OF GREATER DETAIL.

1J – INSTALL FIXTURES, MATERIALS, AND EQUIPMENT ACCORDING TO MANUFACTURERS' SPECIFICATIONS. SHOULD THOSE SPECS CONFLICT WITH THE DRAWINGS, OR VIOLATE LOCAL REGULATIONS, IMMEDIATELY NOTIFY THE OWNER OR THEIR REPRESENTATIVE.

1K – VERIFY CLEARANCES FOR FIXTURES, VENTS, CHASES, ETC. BEFORE ORDERING OR INSTALLING RELATED WORK ITEMS.

1L – COORDINATE ALL WORK WITH EXISTING CONDITIONS, INCLUDING BUT NOT LIMITED TO: IRRIGATION PIPES, ELECTRICAL CONDUITS, WATER LINES, GAS LINES, AND DRAINAGE LINES.

1M – IT IS BEYOND THE SCOPE OF ARCHITECTURAL DRAWINGS TO ILLUSTRATE THE BUILDING CODE. BUILDERS: READ IT, FOLLOW IT.

2 (SITE / FOUNDATION)

2A – ANY SURVEY MARKERS WITHIN THE AREA OF CONSTRUCTION SHALL BE PRESERVED OR RESET BY A REGISTERED CIVIL ENGINEER OR LICENSED LAND SURVEYOR.

2B – GRADING AND SITEWORK SHALL BE MINIMAL IN ALL AREAS NOT DIRECTLY AFFECTED BY THE NEW CONSTRUCTION. FOLLOW BEST PRACTICES AND LOCAL REQUIREMENTS IN ORDER TO MINIMIZE ENVIRONMENTAL DAMAGE.

2C – FINISH GRADE SHALL SLOPE DOWN FROM HOUSE, AT A HEIGHT OF 6 INCHES OVER A 10 FOOT DISTANCE.

2D – BEFORE GRADING OPERATIONS, A TEMPORARY PROTECTION FENCE SHALL BE CONSTRUCTED AROUND ANY TREE WITHIN 30 FEET OF THE FOUNDATION. SILT FENCES SHALL BE CONSTRUCTED DOWNSLOPE OF ANY AREA WHERE THE SOIL IS DISTURBED.

2E – DEPICTED FOUNDATION IS BASED ON FICTIONAL CONDITIONS. CONDUCT A SOIL TEST AND STRUCTURAL ENGINEERING FOR A SITE-SPECIFIC FOUNDATION. (AND THEN YOU CAN DELETE THIS NOTE)

2F – FOOTINGS SHALL EXTEND BELOW THE LOCAL FROST LINE.

2G – PERFORATED DRAINAGE PIPES SHALL BE LOCATED WITHIN A GRAVEL PERIMETER AROUND THE FOUNDATION; AND MULTIPLE DRAINAGE OUTLETS LEAD DOWNSLOPE AWAY FROM THE BUILDING.

2H – ALL WOOD WITHIN 8 INCHES OF THE GROUND SHALL BE PRESSURE TREATED OR COMPRISE A SUITABLY ROT RESISTANT MATERIAL. METAL CONNECTIONS WHICH TOUCH THIS WOOD SHOULD BE GALVANIZED OR STAINLESS STEEL.

3 (CONSTRUCTION)

3A – ALL CONSTRUCTION SHALL BE TRUE, PLUMB, LEVEL, SQUARE, AND IN PROPER ALIGNMENT.

3B – THE GENERAL CONTRACTOR SHALL MAINTAIN A CURRENT AND COMPLETE FULL-SIZE SET OF DRAWINGS ON THE JOB SITE DURING ALL PHASES OF CONSTRUCTION. ALL SUBCONTRACTORS SHALL BE PROVIDED WITH A SET OF DRAWINGS.

3C – THE GENERAL CONTRACTOR SHALL VERIFY AND ASSUME RESPONSIBILITY FOR ALL DIMENSIONS AND SITE CONDITIONS, AS WELL AS INSPECT THE PREMISES AND TAKE NOTE OF EXISTING CONDITIONS PRIOR TO SUBMITTING PRICES. NO CLAIM SHALL BE ALLOWED FOR PROBLEMS [FREEFARMHOUSE.COM] WHICH COULD HAVE BEEN PREVENTED BY A THOROUGH EXAMINATION.

3A – PROVIDE TEMPORARY SUPPORT AS NECESSARY TO ENSURE THE STRUCTURAL INTEGRITY OF THE BUILDING UNDER CONSTRUCTION. THE GENERAL CONTRACTOR IS RESPONSIBLE FOR ALL CONSTRUCTION-RELATED ACTIVITIES.

3D – THE GENERAL CONTRACTOR SHALL BE RESPONSIBLE FOR REGULARLY REMOVING THE WASTE MATERIALS OF ALL SUBCONTRACTORS, AND MAINTAIN STRICT CONTROL OVER JOB CLEANING TO PREVENT DUST AND RUBBISH FROM INTERFERING WITH OPERATIONS.

3E – CONSTRUCTION EQUIPMENT NOISE SHALL BE MINIMIZED DURING THE CONSTRUCTION PHASES BY MUFFLING AND SHIELDING IMPACT TOOLS WHENEVER POSSIBLE.

3F – IF THE WORK OF ANY CONTRACTOR SIGNIFICANTLY DEVIATES FROM THE CONTRACT DRAWINGS WITHOUT THEM FIRST GETTING PERMISSION FROM THE APPROPRIATE PERSON, THAT CONTRACTOR MAY BE REQUIRED TO FIX THEIR WORK AT THEIR OWN EXPENSE.

4 (UTILITIES)

4A – ANY ELECTRICAL, PLUMBING AND/OR HVAC SYSTEMS INCLUDED IN THE WORK SHALL BE INSTALLED ON A DESIGN-BUILD BASIS, AND SHALL NOT SIGNIFICANTLY ALTER THE STRUCTURE OR FINISHES.

5 (WEATHERPROOFING)

5A – CHECK LOCAL CODES FOR INSULATION REQUIREMENTS.

5B – AVOID USING SPRAY FOAM INSULATION WITHOUT MITIGATING MOISTURE ISSUES & THE POSSIBILITY OF HIDDEN STRUCTURAL ROT.

5C – DEPICTED WEATHERPROOFING METHODS (SUCH AS SEALANT, CAULKING, AND FLASHING) ARE NOT COMPREHENSIVE. FOLLOW REQ'TS OF BUILDING CODES, PRODUCT MANUFACTURERS, ETC.

6 (EGRESS / FIRE SAFETY)

6A – FIRE BLOCKING AND FIRE-RATED SHEATHING SHALL BE PROVIDED AS REQUIRED AT CEILINGS, FLOORS, AND ENCLOSED USABLE SPACE UNDER STAIRS.

6B – SMOKE DETECTORS AND CARBON MONOXIDE DETECTORS SHALL BE INSTALLED PER APPLICABLE CODES.

6C – ALL GLASS SHALL CONFORM WITH HUMAN IMPACT AND SAFETY REQUIREMENTS.

6D – ALL REQUIRED EXITS SHALL BE OPERABLE FROM THE INSIDE, WITHOUT THE USE OF A KEY OR ANY SPECIAL KNOWLEDGE.

6E – THE MINIMUM STAIRCASE TREAD SHALL BE 10" AND MAXIMUM RISER OF 7.75", WITH A MAXIMUM 3/8" VARIATION WITHIN A FLIGHT.

6F – HANDRAILS SHALL BE LOCATED 34-38 INCHES [864-965 MM] ABOVE STAIR TREADS AS MEASURED FROM THE NOSINGS.

6G – GUARDRAILS MUST BE LOCATED ALONG ANY EDGE WHERE THE FLOOR DROPS 30" [762] OR MORE TO THE FLOOR OR GROUND BELOW.

7 (FINISHES & FIXTURES)

7A – PROVIDE ADEQUATE BLOCKING AROUND CABINETRY, PLUMBING FIXTURES, AND OTHER APPLICABLE AREAS.

7B – CONTRACTOR MUST ENSURE THE INTERIOR SHEATHING IS FLUSH, CLEAN AND FREE OF DUST AND DEFECTS BEFORE THE APPLICATION OF PAINT COATINGS

7C – FLOOR MATERIAL TRANSITIONS OCCUR AT THE CENTERLINE OF DOORS OR FRAMED OPENINGS.

7D – PROVIDE AT LEAST 1 COAT PRIMER AND 2 FINISH COATS OF PAINT AT INTERIOR AND EXTERIOR SURFACES.

7E – DO NOT USE SCREW-ON, NON-OPERABLE WINDOW SHUTTERS. THEY ARE AS TACKY AS CLIP-ON TIES.

7F – AN ECONOMICAL ALTERNATIVE TO LOUVERED SHUTTERS: BOARD & BATTEN SHUTTERS. BUT DO NOT USE SCREW-ON, NON-OPERABLE SHUTTERS. (IT WOULD BE BETTER TO USE NONE AT ALL.)

7G – DO NOT USE ALUMINUM OR VINYL SIDING. SNAP-ON SIDING MAKES ONCE-BEAUTIFUL HOUSES LOOK LIKE CHEAP PLASTIC TOYS.

7H – SCREEN PORCHES MAY BECOME FUTURE ADDITIONS TO THE CONDITIONED SPACE (AS A MUDROOM, BATHROOM TO A BEDROOM SUITE, ETC). BUILD THEM WITH THAT IN MIND.

7I – WALL-TO-WALL CARPETING IS FORBIDDEN.

9 (CONDITIONS OF USE)

9A – JAY OSBORNE IS THE ORIGINAL DESIGNER OF THIS WORK. INSTEAD OF A CONVENTIONAL COPYRIGHT, HE PROVIDES THESE PLANS UNDER AN OPEN SOURCE LICENSE. SOME RIGHTS RESERVED.

9B – THIS WORK IS PROVIDED UNDER A CREATIVE COMMONS ATTRIBUTION SHARE-ALIKE LICENSE. FOR MORE INFORMATION, SEE WWW.CREATIVECOMMONS.ORG/LICENSES/BY-SA/4.0.

9C – YOU MAY COPY, SHARE, AND MODIFY THIS WORK,

9D – IF YOU USE OR SHARE THIS DESIGN, PROVIDE APPROPRIATE CREDIT TO JAY OSBORNE, AND DO NOT COPYRIGHT HIS WORK.

9E – THIS WORK SHALL NOT BE CONSIDERED A LEGAL DOCUMENT, OR PROFESSIONAL ADVICE, UNLESS IT IS STAMPED OR SIGNED BY A LICENSED PROFESSIONAL (IN THE RELEVANT JURISDICTION) WHO ASSUMES RESPONSIBILITY FOR IT, INCLUDING ANY NECESSARY CHANGES.

9F – ARCHITECTS, BUILDERS, AND OTHER DESIGN PROFESSIONALS MAY PROFIT FROM USING THIS WORK.

9G – IF YOU USE THIS WORK AND/OR CREATE ANY DERIVATIONS, YOU AGREE TO PROVIDE APPROPRIATE CREDIT TO JAY OSBORNE. ATTRIBUTION IS AN ESSENTIAL REQUIREMENT OF THE LICENSE.

9H – APPROPRIATE CREDIT INCLUDES MENTIONING JAY OSBORNE IS THE ORIGINAL DESIGNER. SPECIFY THAT WHERE AND WHEN IT WOULD BE IMPORTANT FOR SOMEBODY. (IF THEY WOULD FEEL SCAMMED WHEN LEARNING THE TRUTH, THEN YOU DID IT WRONG.) ALSO MENTION ANY CHANGES YOU MADE, IF APPLICABLE– BUT DON'T IMPLY JAY OSBORNE HAD ENDORSED THEM.

9I – THESE DRAWINGS ARE DERIVED FROM SKETCHUP MODELS, WHICH CAN BE DOWNLOADED FOR FREE ONLINE.

9J – IT IS IMPOSSIBLE FOR ONE SET OF ARCHITECTURAL DRAWINGS TO FULFILL THE REQUIREMENTS OF EVERY JURISDICTION. THIS IS A TEMPLATE TO START FROM. THE GC OR DESIGNER OF RECORD (OR WHOEVER REMOVES THIS NOTE) SHALL TAKE RESPONSIBILITY FOR ADAPTING THIS DESIGN TO LOCAL REQUIREMENTS.

9K – USE THIS WORK AT YOUR OWN RISK. THIS DESIGN IS PROVIDED "AS IS" WITH NO GUARANTEES OR WARRANTIES, EXPRESS OR IMPLIED, INCLUDING (BUT NOT LIMITED TO) THE WARRANTIES OF MERCHANTABILITY, OR FITNESS FOR A PARTICULAR PURPOSE. IN NO EVENT SHALL JAY OSBORNE OR FREEFARMHOUSE BE HELD LIABLE FOR ANY CLAIM, DAMAGES, OR OTHER LIABILITY (WHETHER IN AN ACTION OF CONTRACT, TORT, OR OTHERWISE) ARISING FROM, OUT OF, OR IN CONNECTION WITH THIS WORK (OR THE USE, OR OTHER DEALINGS IN THIS DESIGN). IN SHORT: BE RESPONSIBLE.



OPEN-SOURCE ARCHITECTURAL DRAWINGS
You may share, copy, and customize these blueprints.
License: [www.CreativeCommons.org/licenses/BY-SA/4.0](https://creativecommons.org/licenses/by-sa/4.0/)
Some rights reserved. No promises or guarantees given.
Download the free files at www.FreeFarmhouse.com

A DESIGN BY JAY OSBORNE
CAROLINE'S FARMHOUSE
THE ORIGINAL STARTER FARMHOUSE PLANS

3 2025-08-08 ORIGINAL DESIGN (FINISHED PLANS)
2 2023-10-01 CAROLINE: BLUEPRINTS ON PATREON
1 2023-01-04 STARTER FARMHOUSE SCHEMATICS

+ See A0.1 for more project history and credits


GENERAL NOTES

A0.2

© ATTRIBUTION SHARE-A-LIKE BY JAY OSBORNE. THESE DRAWINGS ARE FOR INFORMATIONAL PURPOSES ONLY. THIS DESIGN AND ITS RELATED DOCUMENTS ARE PROVIDED "AS IS" WITH NO GUARANTEES OR WARRANTIES, EXPRESS OR IMPLIED. FREEFARMHOUSE & JAY OSBORNE DISCLAIM LIABILITY FOR ANY DAMAGES THAT MAY RESULT FROM USING THIS WORK.

FOUNDATION PLAN NOTES


- 1. ALL FOUNDATION DESIGNS MUST BE ENGINEERED TO LOCAL CONDITIONS. THIS IS ONLY A TEMPLATE. MANY FACTORS MUST BE CONSIDERED FOR A COMPLETE WORK, LIKE SOIL TYPE, SEISMIC ISSUES, SLOPING TERRAIN, FLOODING, AND HEIGHT RESTRICTIONS.
- 2. OTHER FOUNDATION TYPES CAN BE USED, LIKE A BASEMENT, SLAB, OR PIERS.
- 3. STRUCTURAL BRICK FACING MAY BE 1" THIN BRICK VENEER INSTEAD, WHICH CAN LOOK BETTER THAN 4-5" BRICK VENEERS. BRICKWORK SHOULDN'T PROTRUDE PAST THE SIDING.
- 4. DON'T USE CONCRETE WITH FAKE BRICK TEXTURE. PLAIN CONCRETE IS MUCH BETTER.

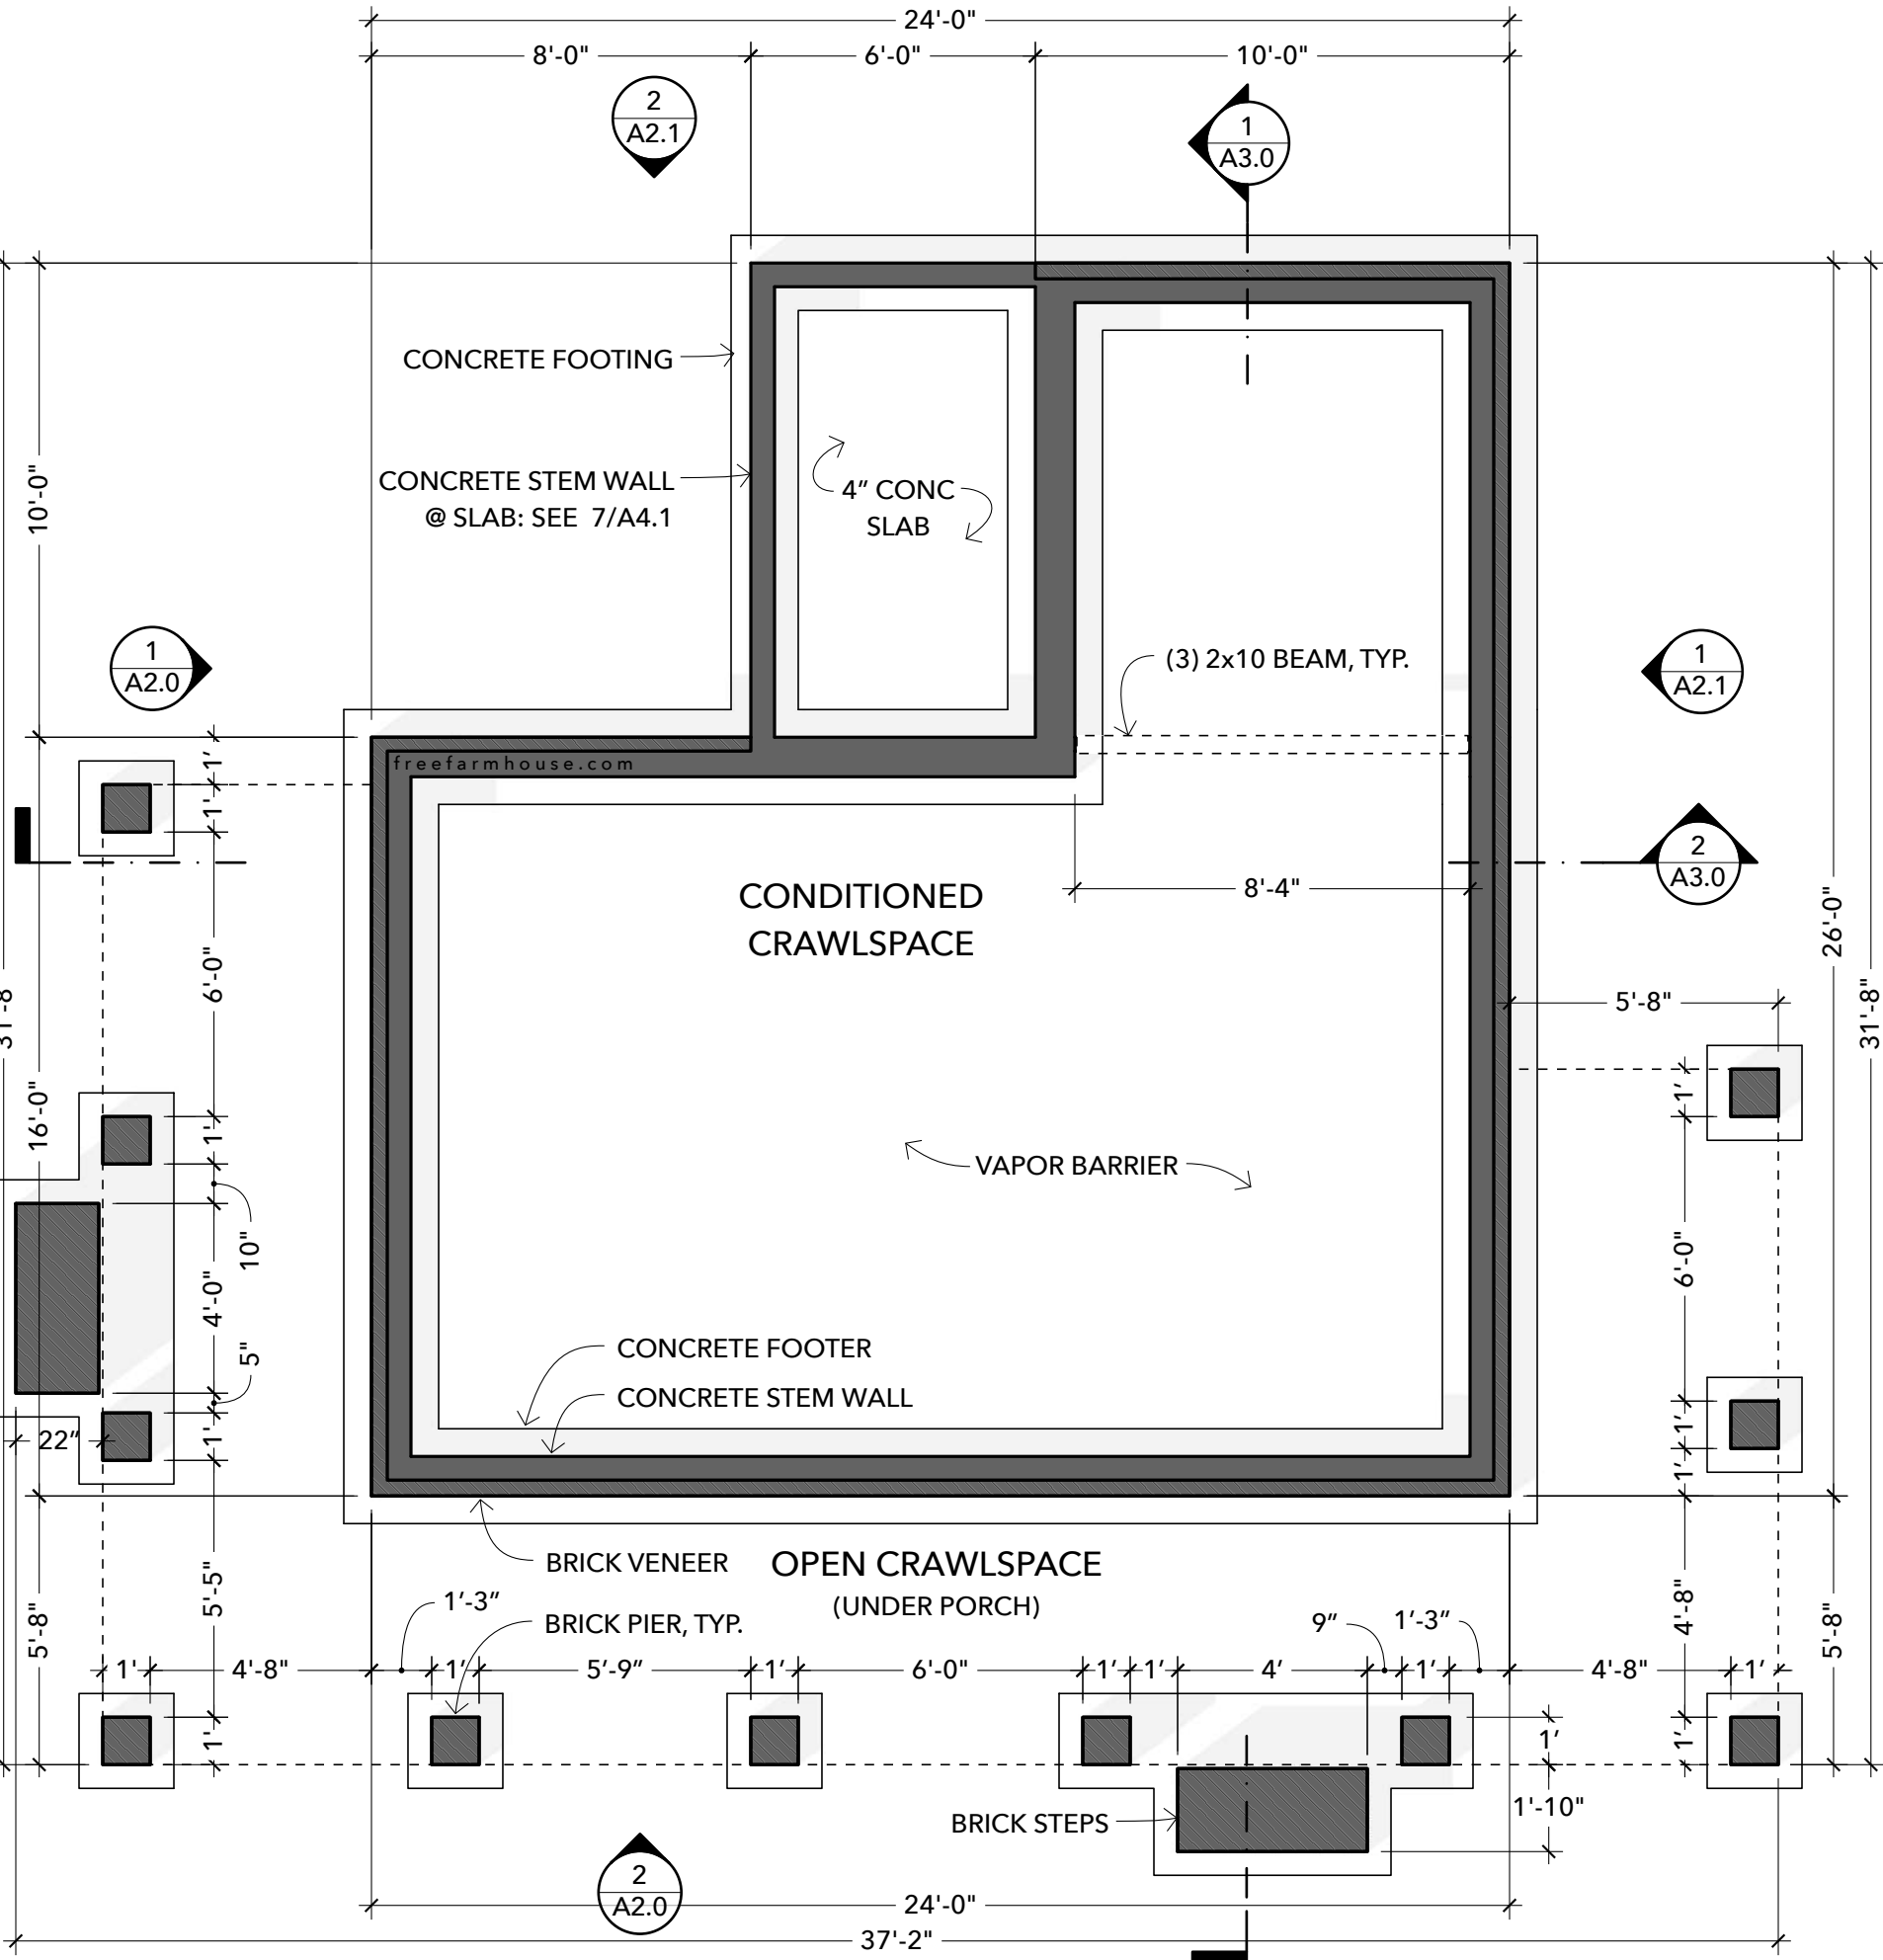

1 FOUNDATION PLAN
SCALE: 1/4" = 1'-0"

ROOF PLAN NOTES

- 1. DATUMS ARE TO FINISH FLOOR OF MAIN LEVEL. HOUSE HEIGHTS ARE MEASURED IN MANY WAYS. THIS DESIGN WORKS WITH MOST 25-FOOT BUILDING HEIGHT LIMITS.
- 2. TO REDUCE ROOFING COSTS, REPLACE STANDING SEAM WITH 5V METAL PANELS.
- 3. ROOF DIMENSIONS ARE ROUGH, NOT PRECISE ENOUGH FOR CONSTRUCTION. DIMENSIONS IN BUILDING SECTIONS AND FLOOR PLANS TAKE PRECEDENCE.
- 4. ROOF HAS MANY APPROPRIATE MATERIAL OPTIONS, BUT WAREHOUSE-LOOKING METAL ROOFING (WITH RECTANGULAR CORRUGATIONS) SHOULD BE AVOIDED.

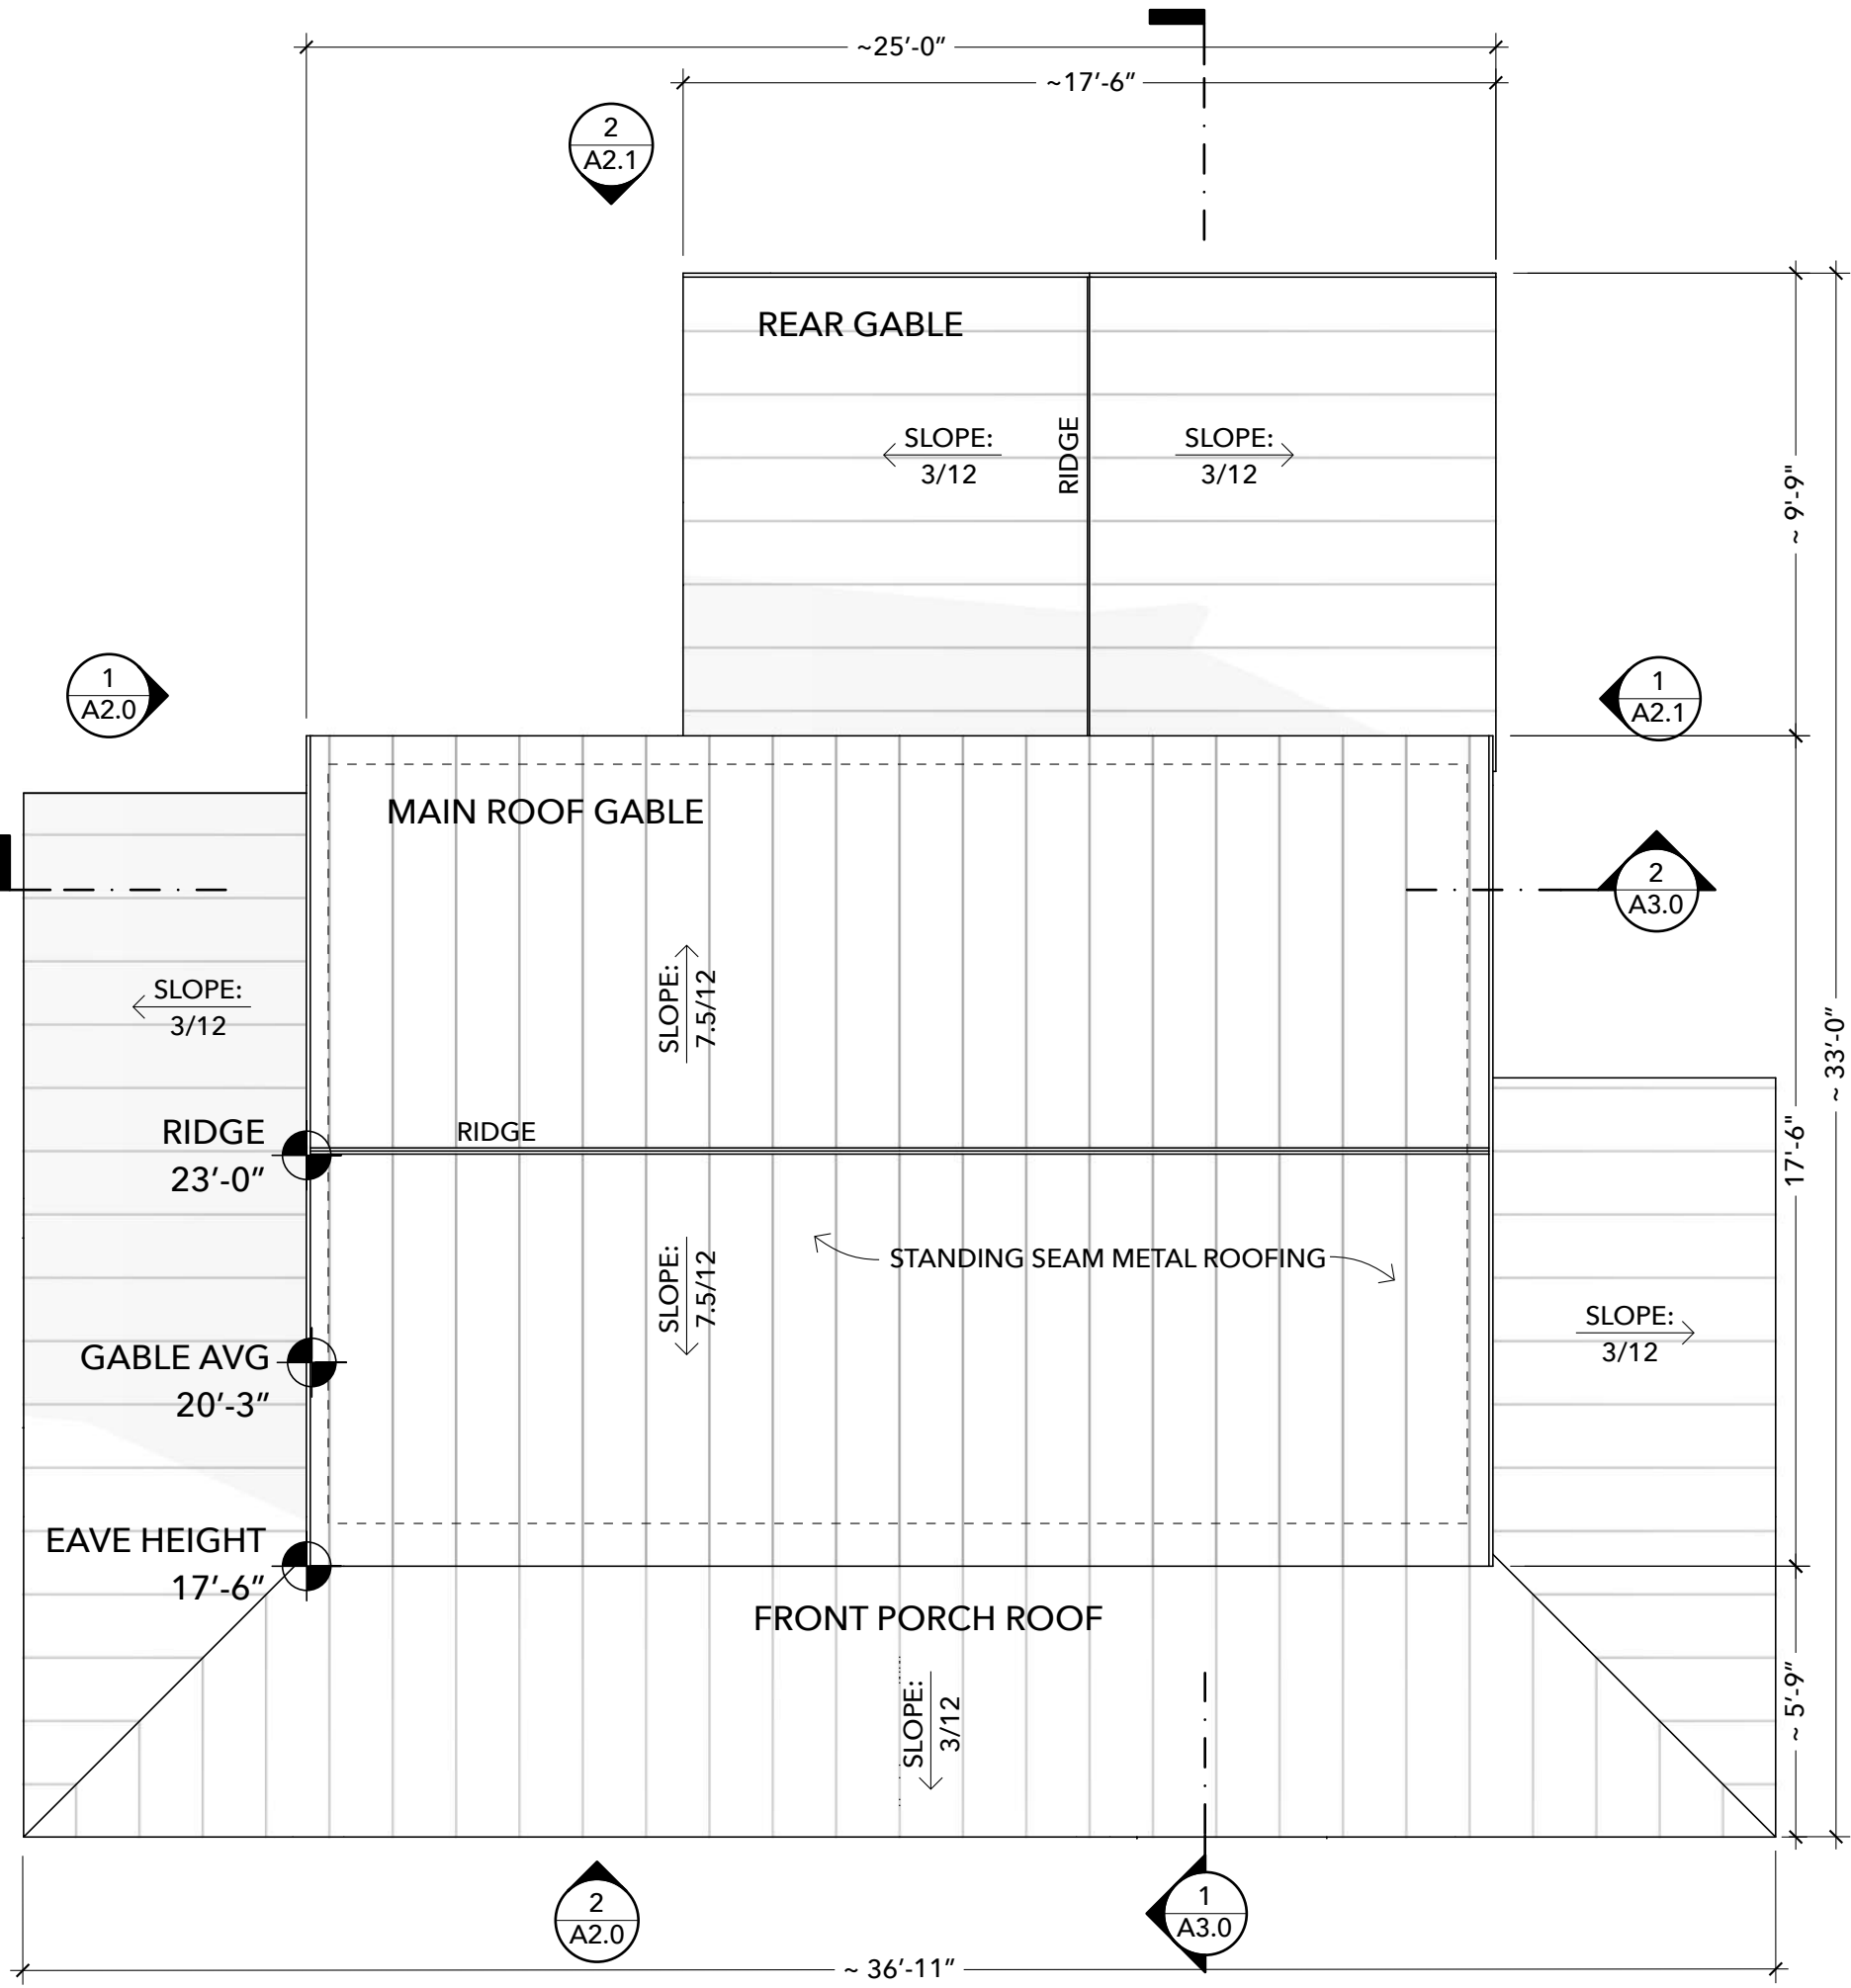

2 ROOF PLAN
SCALE: 1/4" = 1'-0"

CC Attribution share alike by Jay Osborne. These drawings are for informational purposes only. This design and its related documents are provided "as is" with no guarantees or warranties, express or implied. FreeFarmhouse & Jay Osborne disclaim liability for any damages that may result from using this work.

FLOOR PLAN NOTES:

- 1. IF MORE THAN 3 RISERS ARE NEEDED AT PORCH STEPS, A HANDRAIL SHOULD BE PROVIDED (AS REQ'D BY CODE).
- 2. GUARDRAIL MAY BE REQUIRED AT PORCH IF DROP TO GROUND IS INCREASED TO MORE THAN 24-30" (SEE LOCAL REQ'TS).
- 3. NOTE THAT SOME DIMENSIONS ARE TO THE CENTER OF THE POSTS, OTHERS TO THE EDGES OF POSTS (& BEAMS THEY SIT ON OR HOLD UP).
- 4. OPTIONAL BUILT-IN SHELVING. POSSIBLE LOCATION FOR WOODSTOVE.

DOORS


- A 36x84 9-LITE FRONT DOOR
- B 36x80 4-LITE BACK DOOR
- C 30x80 5-PANEL DOOR
- D 24x80 1-PANEL DOOR
- E 18x80 LOUVERED DOOR

WINDOWS


- 1 32x72 DH 2/2 DIVIDED LITES
- 2 32x60 DH 2/2 DIVIDED LITES
- 3 24x42 DH 2/2 DIVIDED LITES

CEILING/ ELECTRICAL NOTES:

- 1. CEILING HEIGHTS ARE APPROXIMATE (+/- 1")
- 2. UTILITY ROOM CEILING SHALL BE FIRE-RATED WITH GYP BD SHEATHING
- 3. HEAD CLEARANCE AT STAIRCASE TO BE 80" MINIMUM
- 4. SHOWER MAY INSTEAD BE REPLACED BY STACKED LAUNDRY UNITS. IN THAT CASE, MAKE SURE TO SPECIFY THE APPROPRIATE OUTLETS.

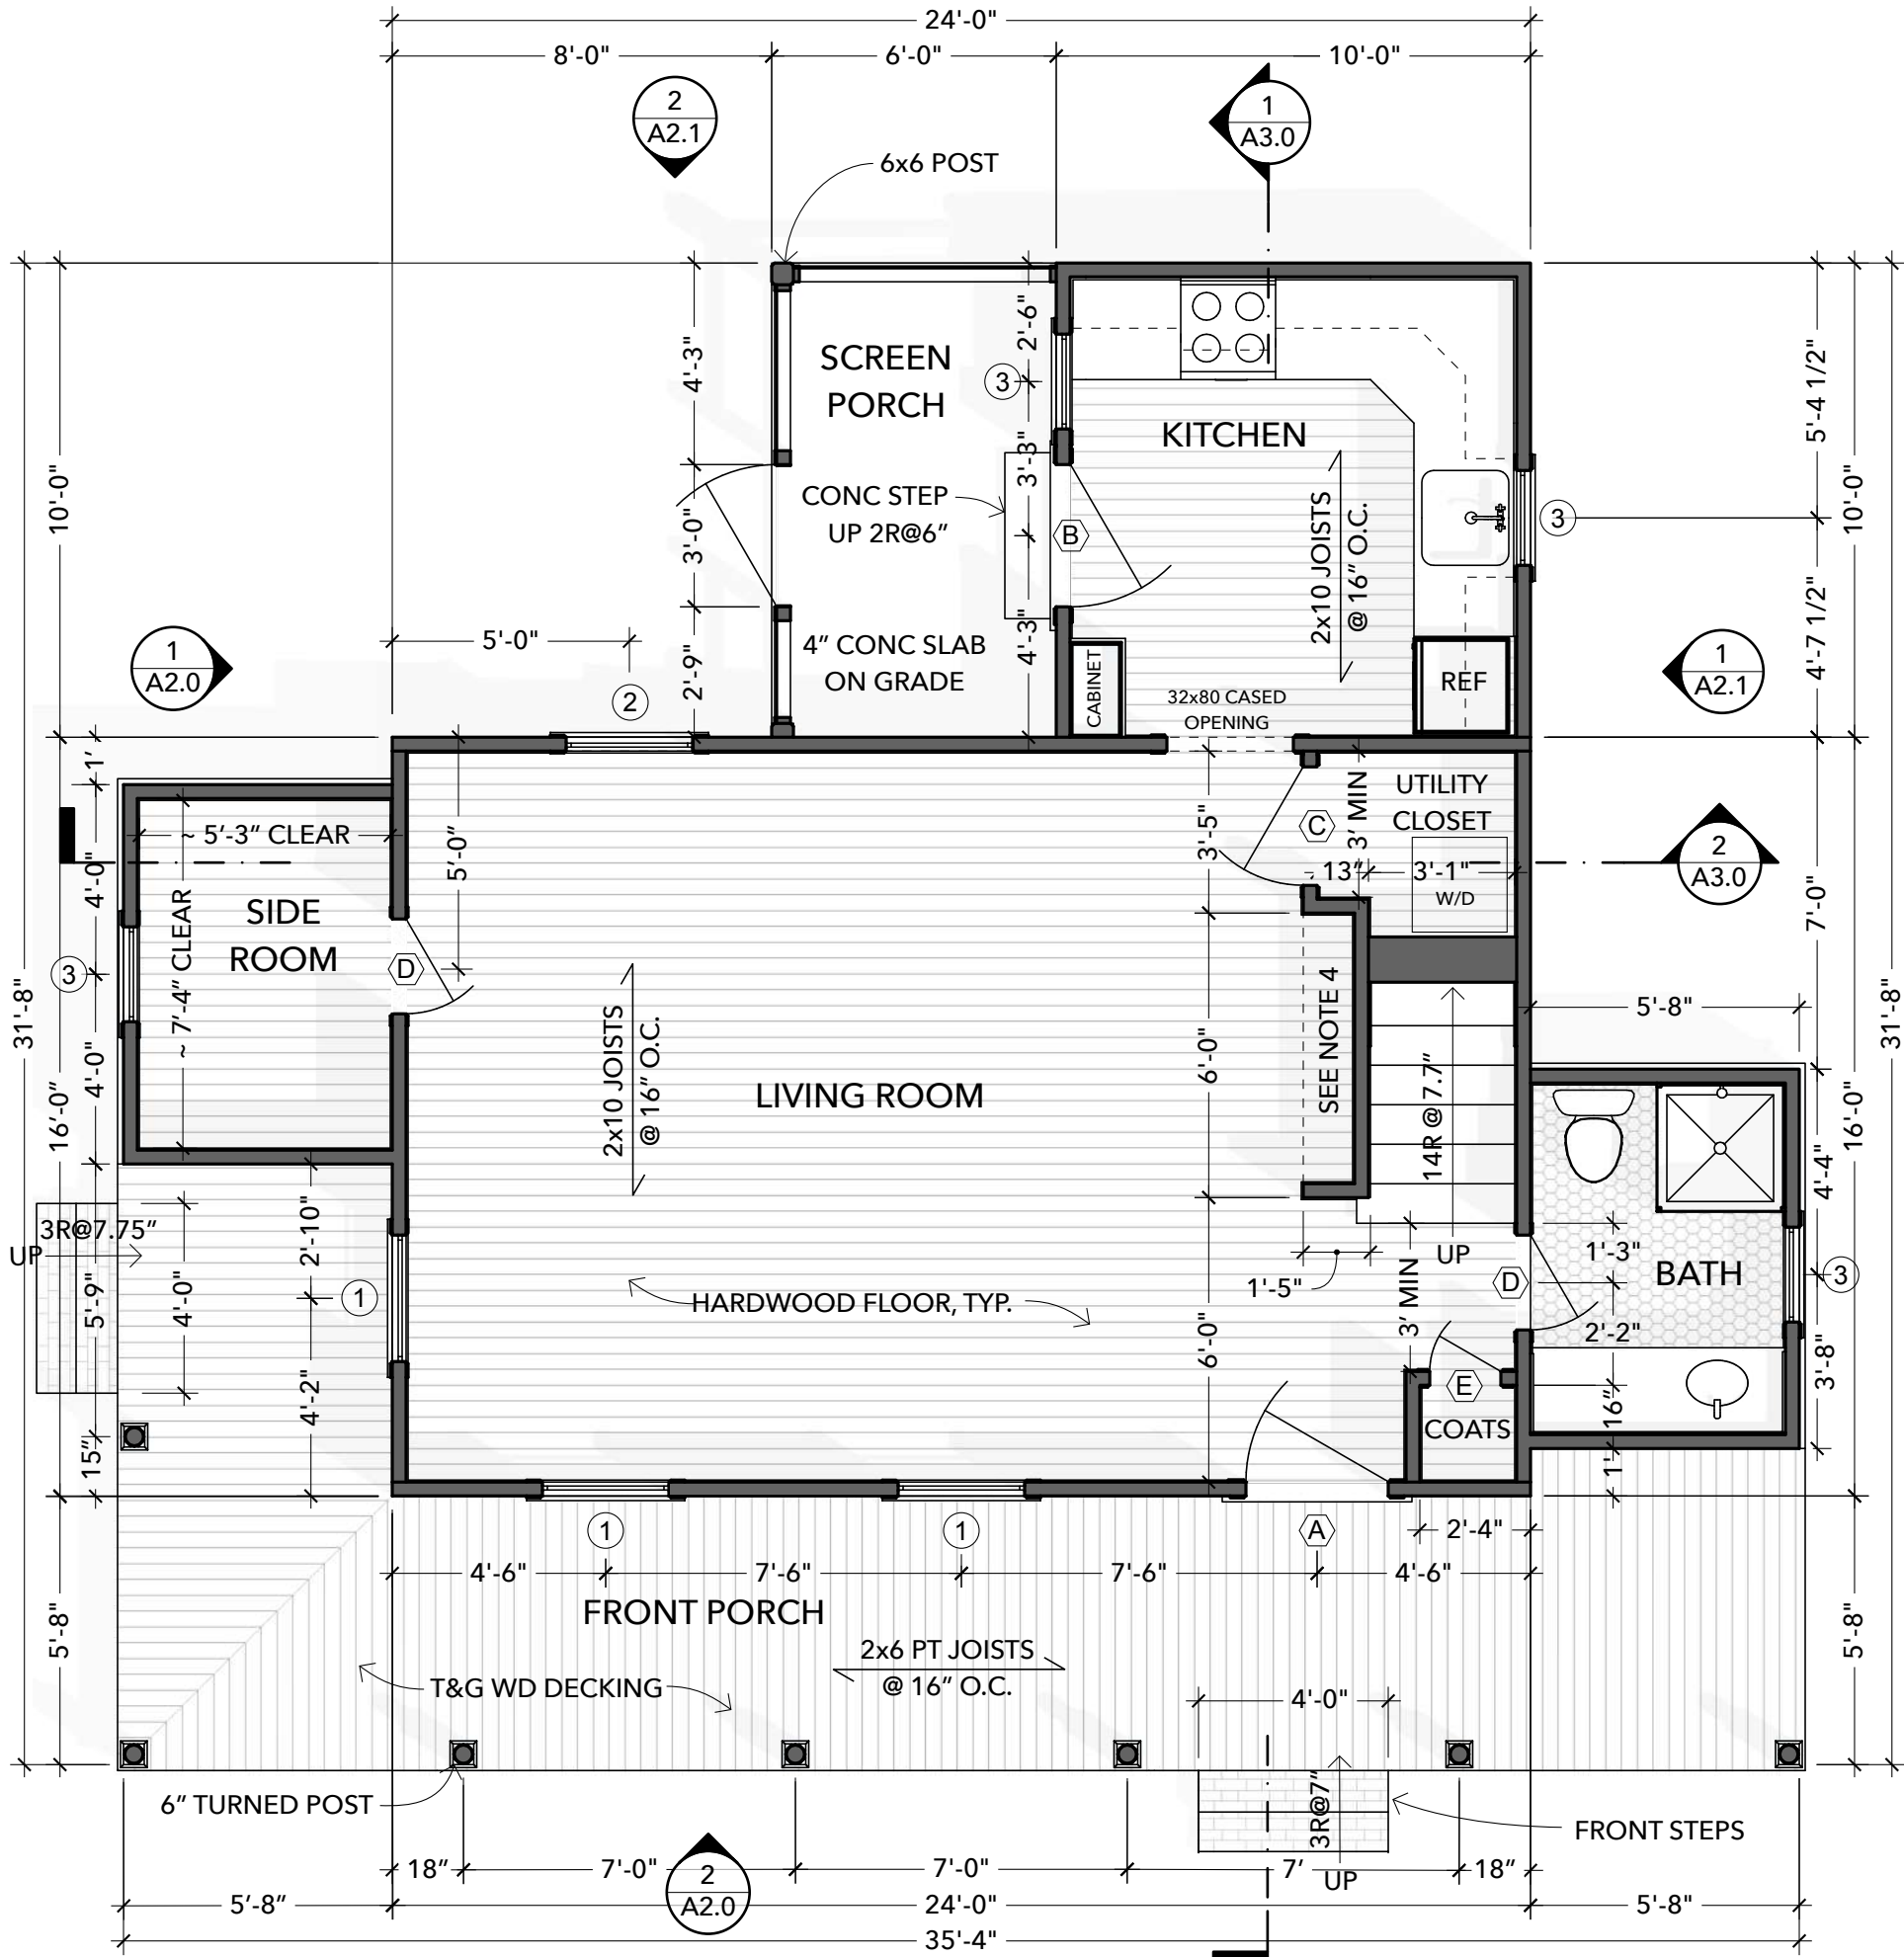

1 DOWNSTAIRS FLOOR PLAN
SCALE: 1/4" = 1'-0"

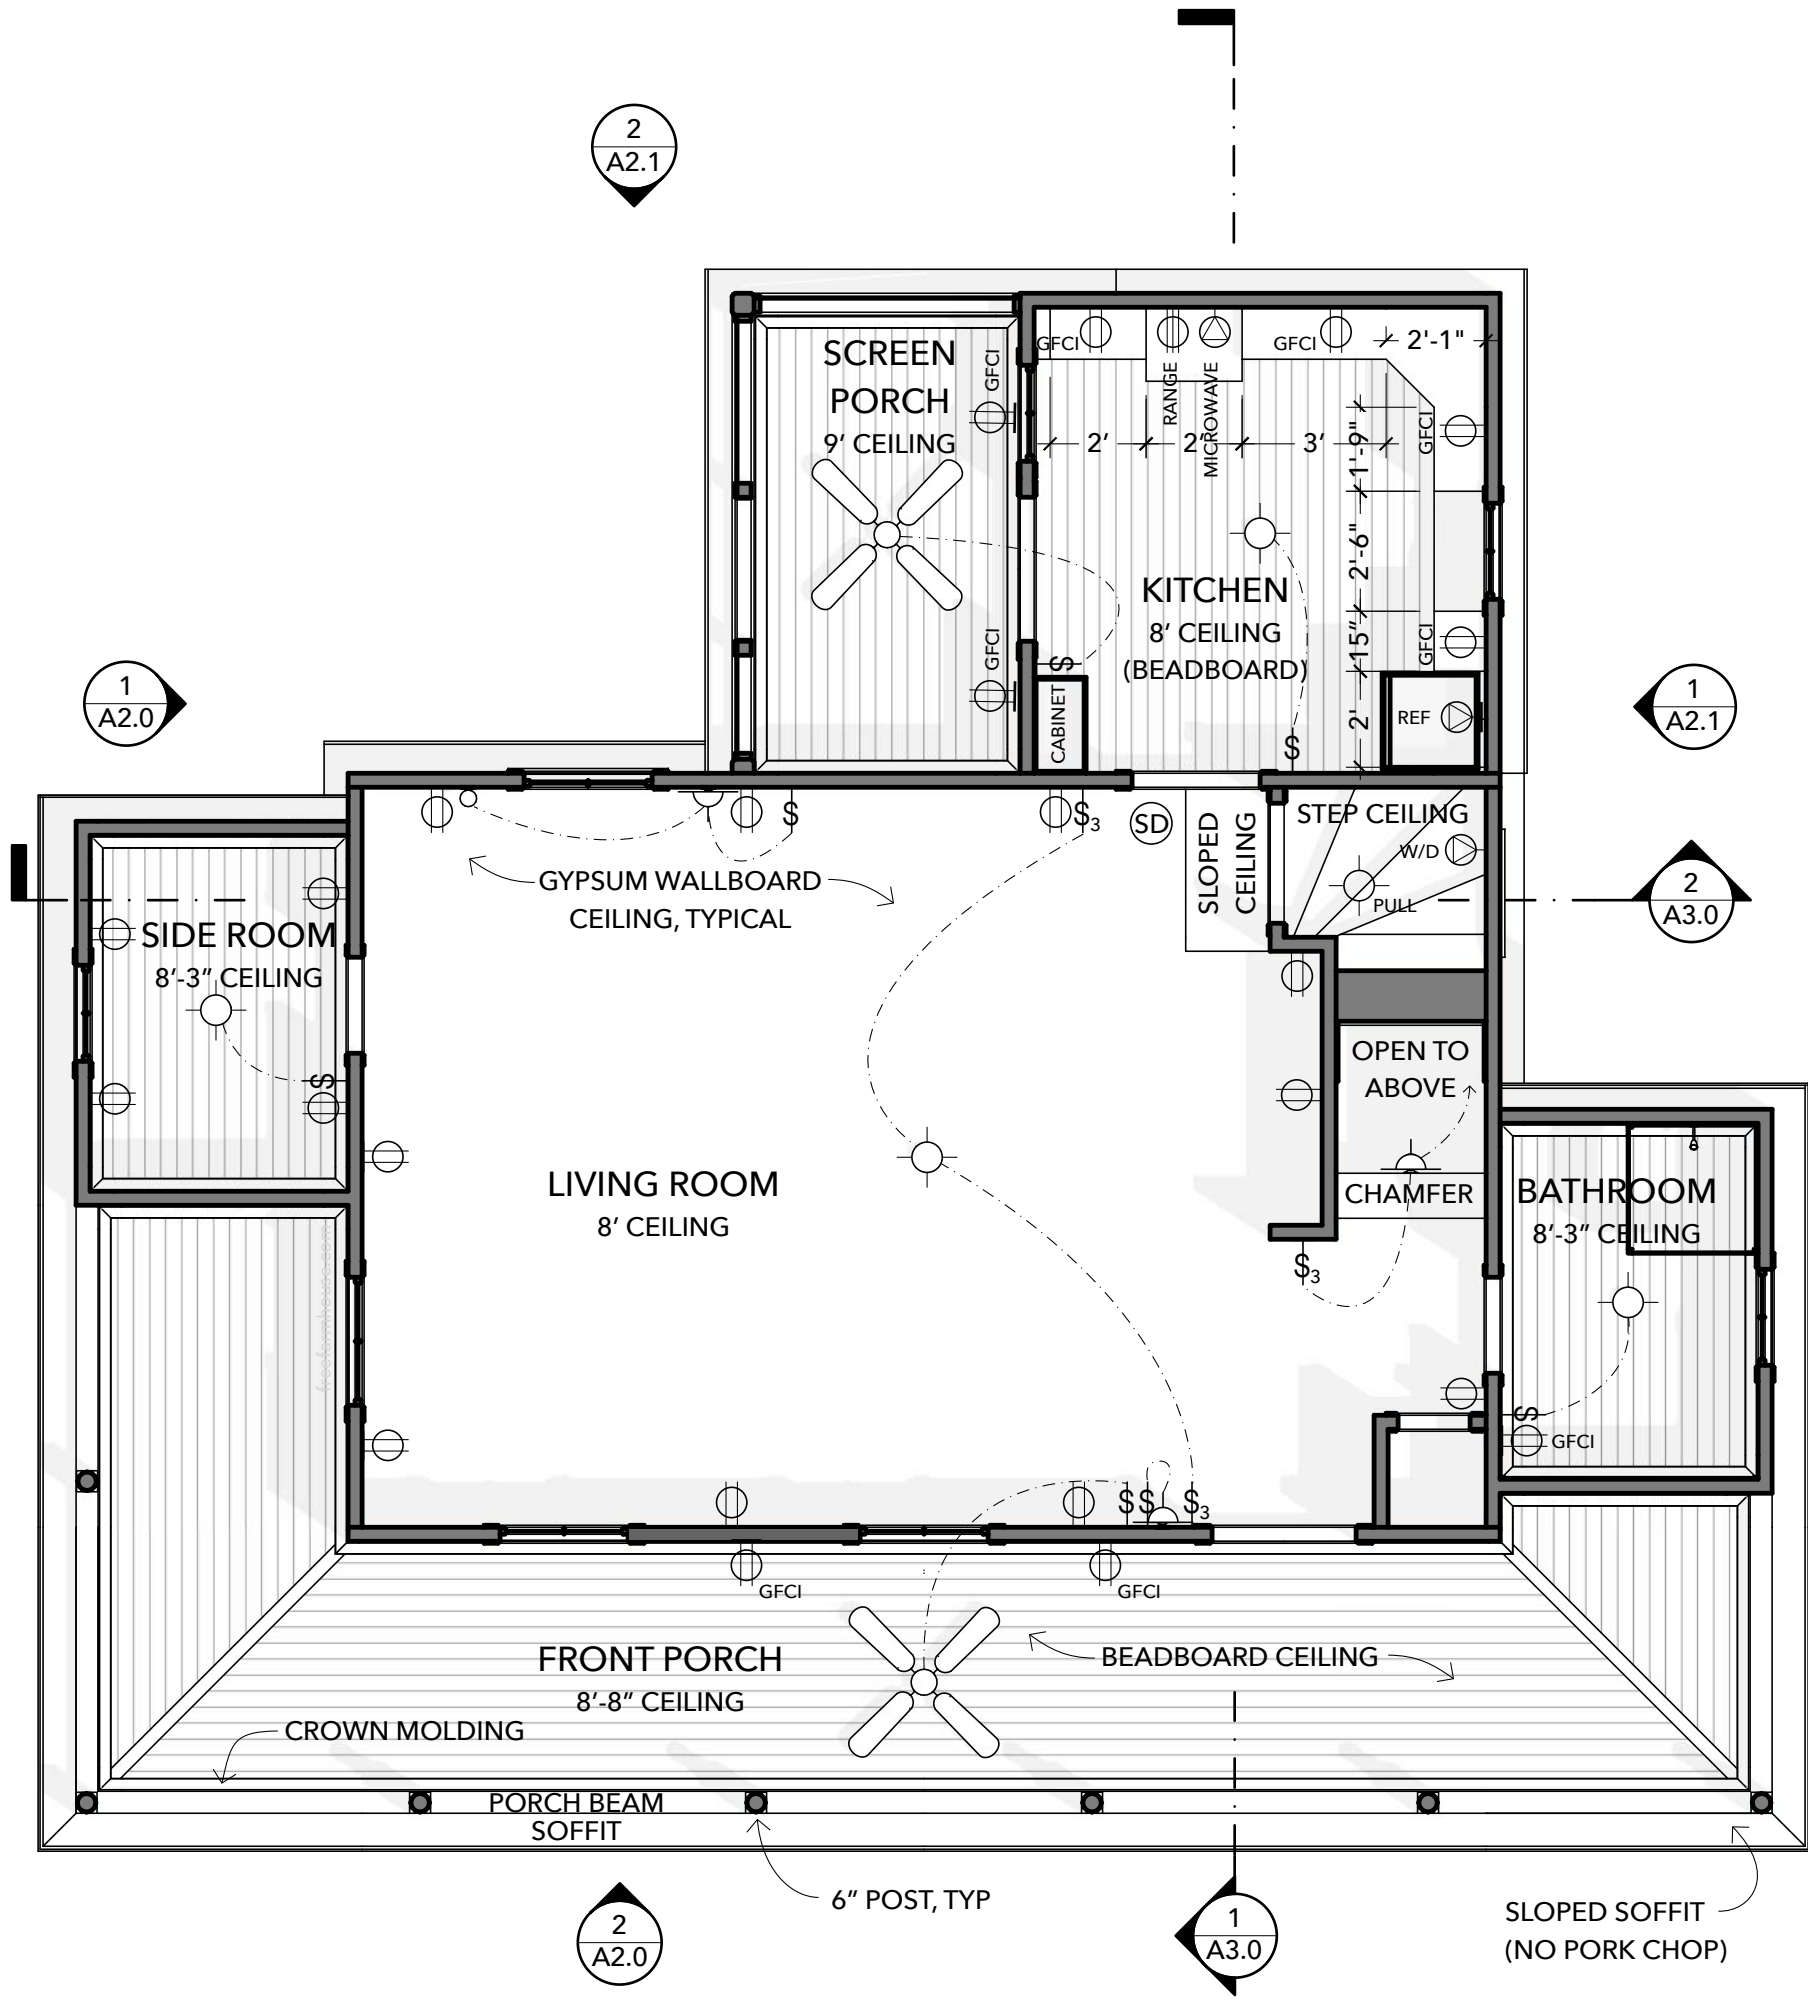

2 DOWNSTAIRS CEILING & ELECTRICAL PLAN
SCALE: 1/4" = 1'-0"



OPEN-SOURCE ARCHITECTURAL DRAWINGS
You may share, copy, and customize these blueprints.
License: [www.CreativeCommons.org/licenses/by-sa/4.0](https://creativecommons.org/licenses/by-sa/4.0/)
Some rights reserved. No promises or guarantees given.
Download the free files at www.FreeFarmhouse.com

A DESIGN BY JAY OSBORNE
CAROLINE'S FARMHOUSE
THE ORIGINAL STARTER FARMHOUSE PLANS

3 2025-08-08 ORIGINAL DESIGN (FINISHED PLANS)
2 2023-10-01 CAROLINE: BLUEPRINTS ON PATREON
1 2023-01-04 STARTER FARMHOUSE SCHEMATICS
+ See A0.1 for more project history and credits

DOWNSTAIRS PLANS

A1.1

© ATTRIBUTION SHARE-A-LIKE BY JAY OSBORNE. THESE DRAWINGS ARE FOR INFORMATIONAL PURPOSES ONLY. THIS DESIGN AND ITS RELATED DOCUMENTS ARE PROVIDED "AS IS" WITH NO GUARANTEES OR WARRANTIES, EXPRESS OR IMPLIED. FREEFARMHOUSE & JAY OSBORNE DISCLAIM LIABILITY FOR ANY DAMAGES THAT MAY RESULT FROM USING THIS WORK.

FLOOR PLAN NOTES:

- 1. WINDER STAIRS MUST FOLLOW STRICT CODES. THEY ARE SAFER THAN IN THE PAST, BUT NOW HARDER TO BUILD.
- 2. BEDROOM CLOSET AT RAISED PLATFORM (STAIRS) CAN BE OMITTED.
- 3. LINEN CLOSET (AT HALL) MAY INSTEAD BE A CHASE FOR DUCTWORK.
- 4. BEDROOM CLOSET MAY BE REPLACED BY A WARDROBE.
- 5. SIDE WINDOW AT WINDER STAIRS CAN BE OMITTED, BUT SHALL STILL BE FRAMED IN, IN CASE OF FUTURE REAR ADDITION AT 2ND LEVEL.

DOORS



- A 36x84 9-LITE FRONT DOOR
- B 36x80 4-LITE BACK DOOR
- C 30x80 5-PANEL DOOR
- D 24x80 1-PANEL DOOR
- E 18x80 LOUVERED DOOR

WINDOWS

- 1 32x72 DH 2/2 DIVIDED LITES
- 2 32x60 DH 2/2 DIVIDED LITES
- 3 24x42 DH 2/2 DIVIDED LITES

CEILING PLAN NOTES:

- 1. CEILING HEIGHTS ARE APPROXIMATE (+/- 1"). PRIORITIZE DIMENSIONS SHOWN IN SECTION DRAWINGS.
- 2. HEAD CLEARANCE AT STAIRCASE TO BE 80" MINIMUM
- 3. WALL-MOUNTED LIGHTS ARE PREFERRED WHEREVER EFFICIENCY AND STERILITY ARE NOT VIRTUES.

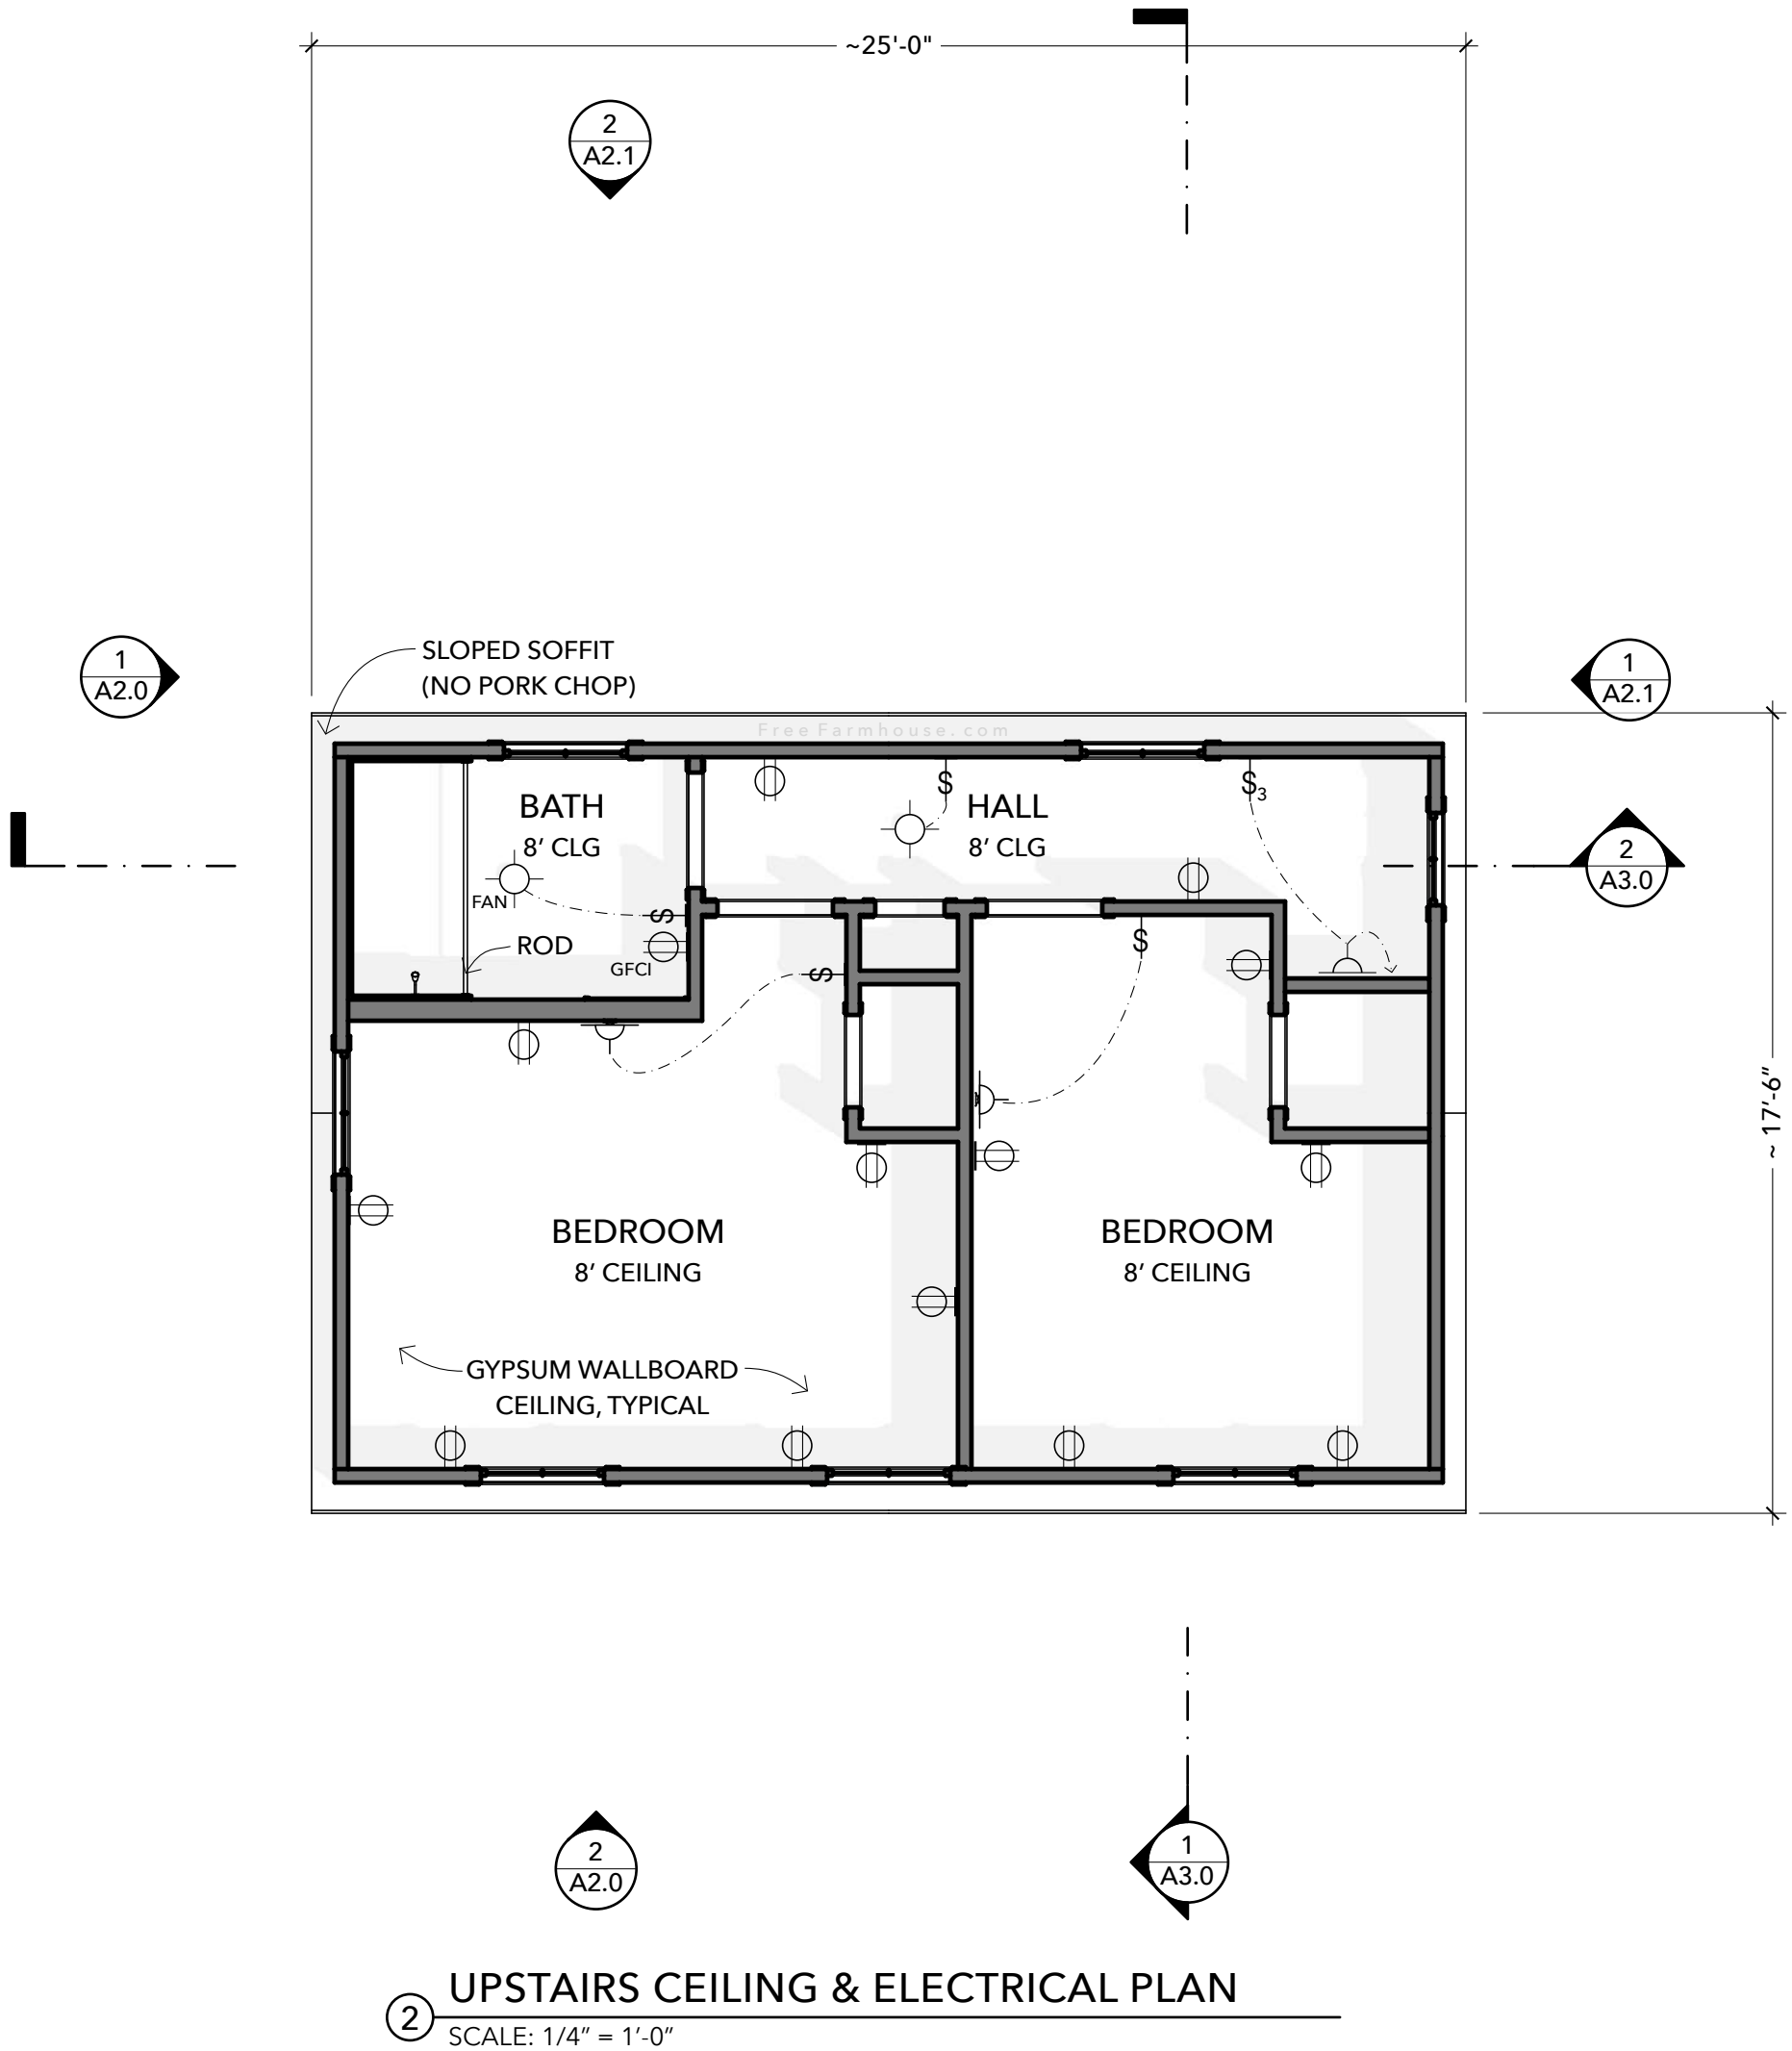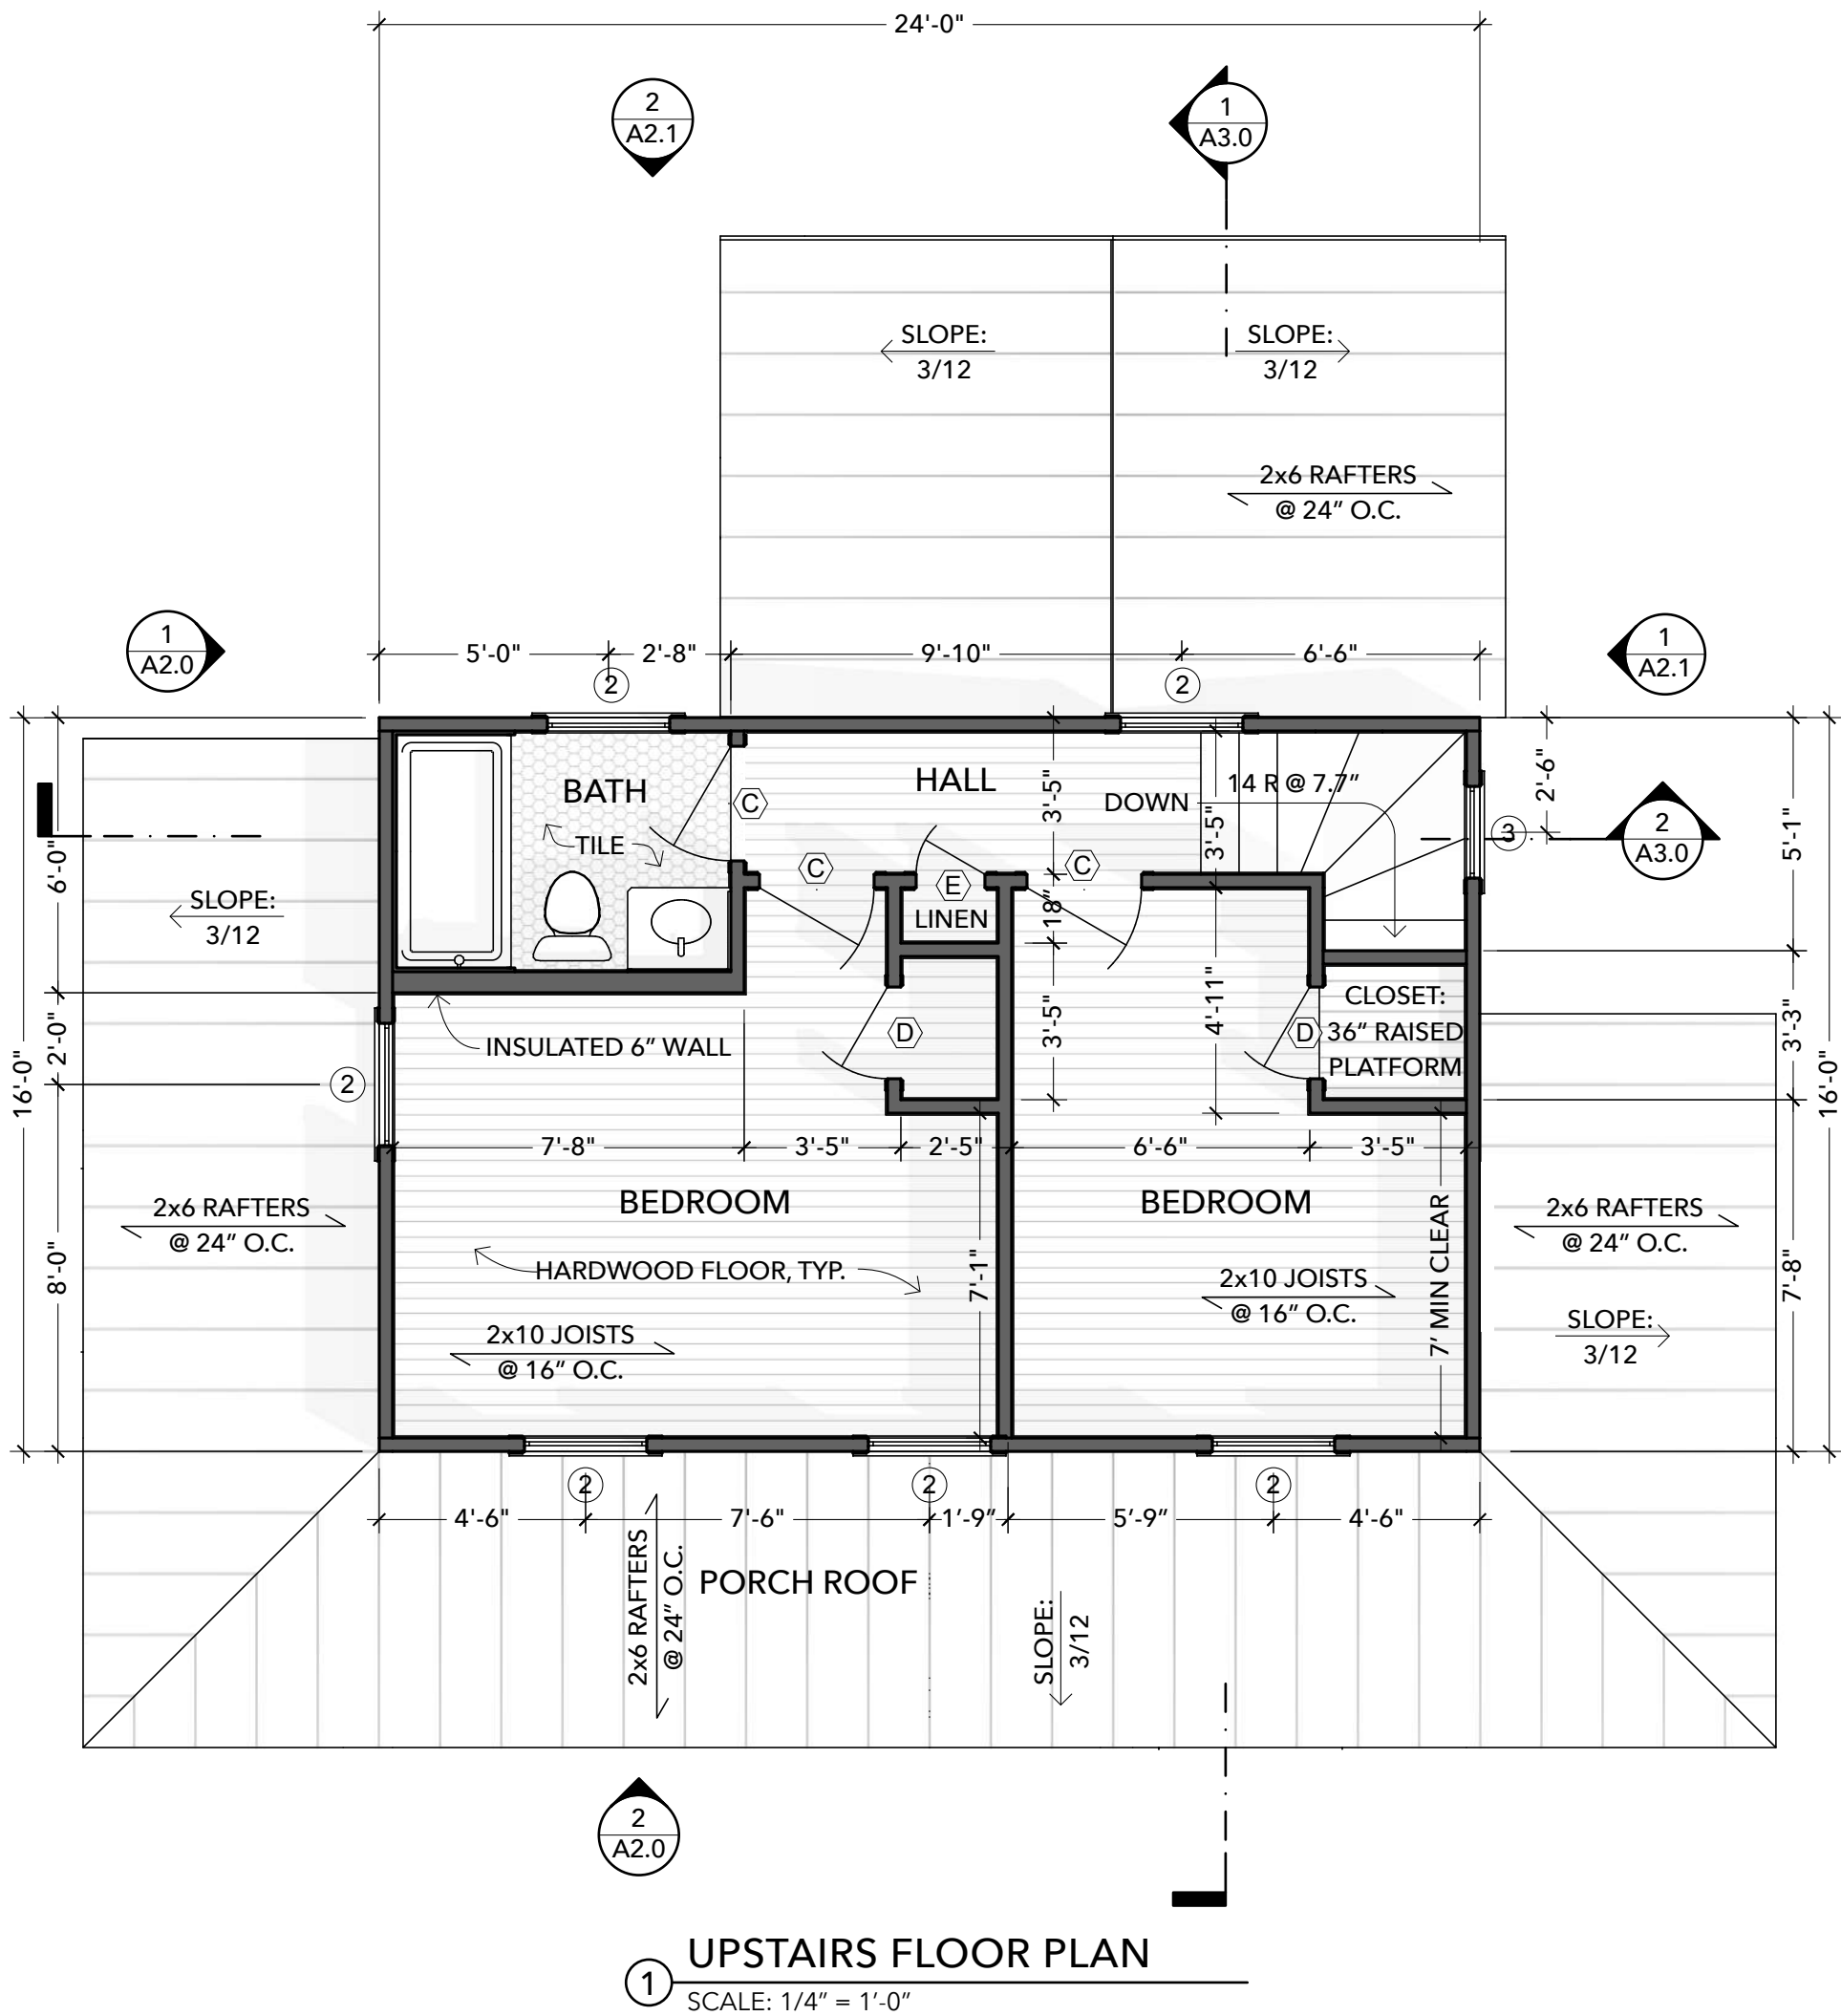

OPEN-SOURCE ARCHITECTURAL DRAWINGS
You may share, copy, and customize these blueprints.
License: [www.CreativeCommons.org/licenses/by-sa/4.0](https://creativecommons.org/licenses/by-sa/4.0/)
Some rights reserved. No promises or guarantees given.
Download the free files at www.FreeFarmhouse.com

A DESIGN BY JAY OSBORNE
CAROLINE'S FARMHOUSE
THE ORIGINAL STARTER FARMHOUSE PLANS

3 2025-08-08 ORIGINAL DESIGN (FINISHED PLANS)
2 2023-10-01 CAROLINE: BLUEPRINTS ON PATREON
1 2023-01-04 STARTER FARMHOUSE SCHEMATICS
+ See A0.1 for more project history and credits

UPSTAIRS PLANS
A1.2

ELEVATION NOTES


- 1. DATUMS ARE TO FINISH FLOOR. HOUSE HEIGHTS ARE MEASURED IN MANY WAYS, BUT THIS DESIGN VARIATION WORKS WITH MOST 25-FOOT BUILDING HEIGHT LIMITS.
- 2. WINDOW SHUTTERS SHALL BE OPERABLE. TACK-ON VINYL SHUTTERS ARE STRICTLY FORBIDDEN, BECAUSE THE HOUSE WOULD LOOK BETTER WITH NO SHUTTERS AT ALL.
- 3. THOU SHALT NOT USE VINYL SIDING. THIS IS A HOUSE, NOT A CHEAP PLASTIC TOY.
- 4. IF HIGH DROP TO GROUND, WINDOW SILLS MAY NEED TO BE >24" ABOVE FLOOR.
- 5. DO NOT "PORK CHOP" ANY OF THE ROOF EAVES.

6. **DOORS:** MARVIN ULTIMATE SERIES. BUT ANTIQUES PREFERRED. TRIM: WOOD OR FIBER CEMENT: 1x4 SIDE, 2x6 UPPER (W/ EXPOSED FLASHING), 3" SILL.


7. **WINDOWS:** DOUBLE HUNG W/ 2/2 DIVIDED LITES, MARVIN ULTIMATE SERIES, OR ANTIQUE. TRIM: SOLID WOOD OR FIBER CEMENT: 1x4 SIDE, 2x6 UPPER, 3" SILL.

8. **SIDING:** 4-6" FIBER CEMENT CLAPBOARD. JAMES HARDIE: ARTISAN SERIES. OTHER OPTIONS: WOOD, SHINGLES, BOARD & BATTEN. BUT VINYL SIDING IS FORBIDDEN.


9. **ROOFING:** STANDING SEAM METAL PANELS (16"). IF BUDGET ALLOWS: WOOD SHINGLES OR SLATE. TO SAVE COSTS: USE 5V GALVALUME PANELS OR ROUND CORRUGATED STEEL. DON'T USE METAL PANELS WITH SQUARE-ISH CORRUGATIONS.

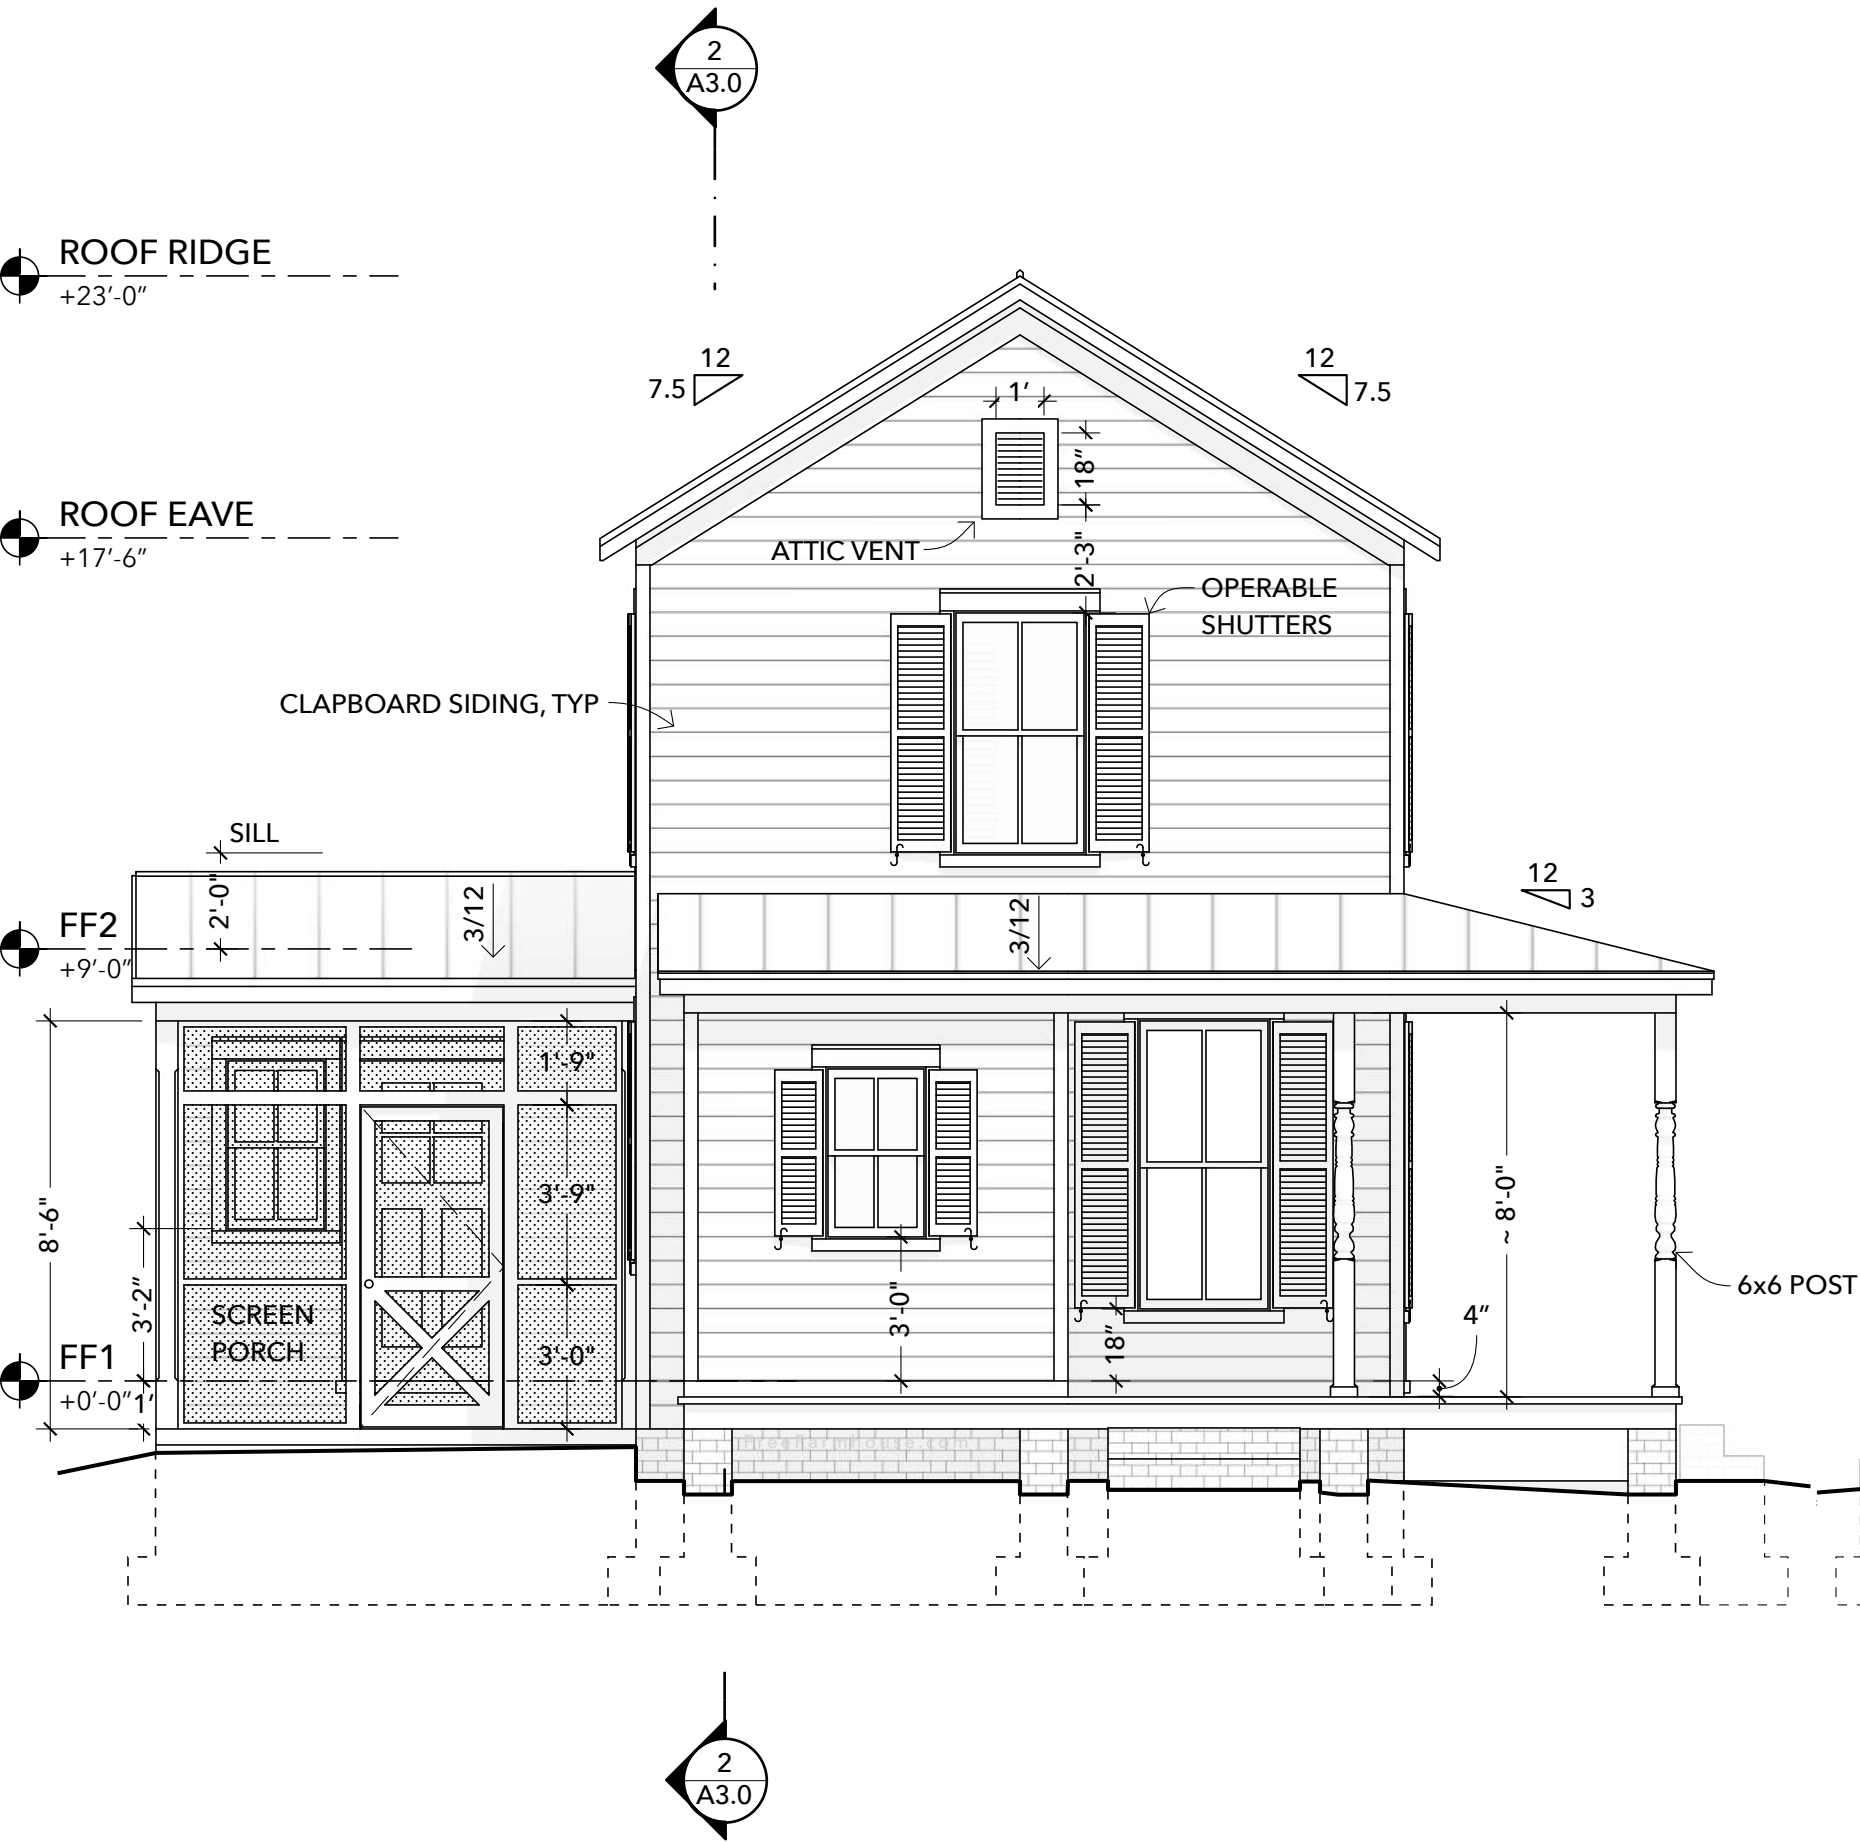

1 WEST ELEVATION
SCALE: 1/4" = 1'-0"

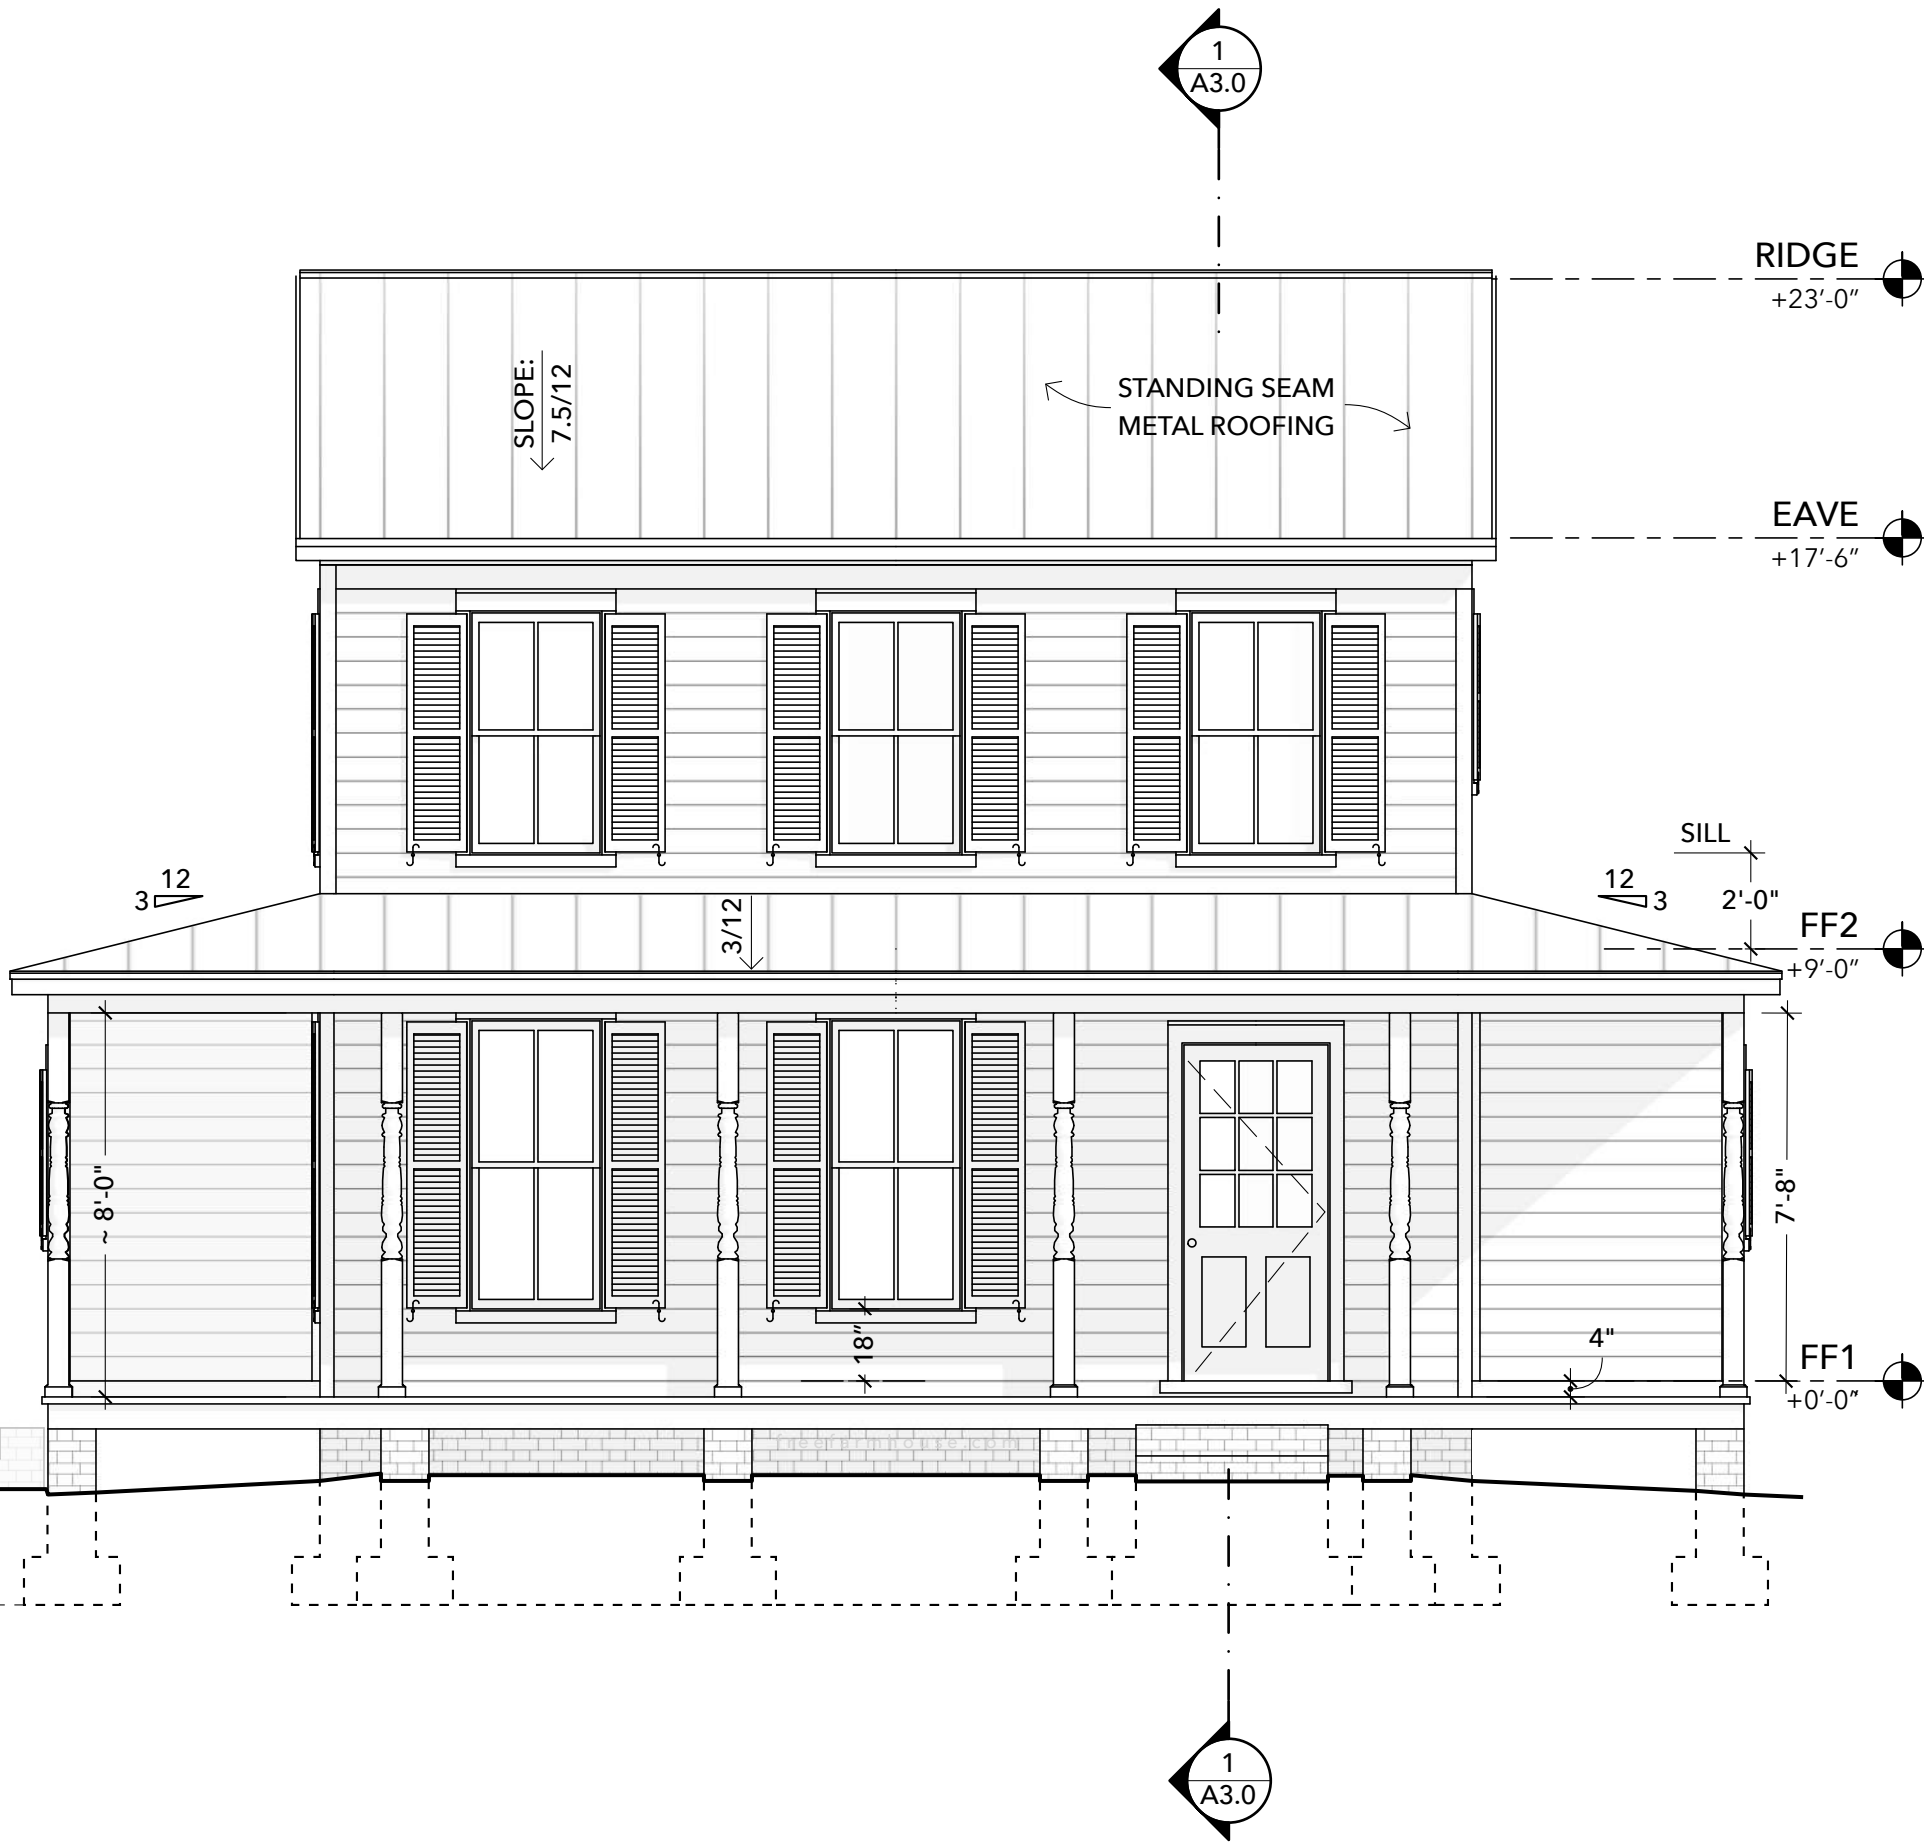

2 SOUTH ELEVATION (FRONT)
SCALE: 1/4" = 1'-0"

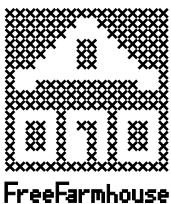

OPEN-SOURCE ARCHITECTURAL DRAWINGS
You may share, copy, and customize these blueprints.
License: [www.CreativeCommons.org/licenses/by-sa/4.0](https://creativecommons.org/licenses/by-sa/4.0/)
Some rights reserved. No promises or guarantees given.
Download the free files at www.FreeFarmhouse.com

A DESIGN BY JAY OSBORNE
CAROLINE'S FARMHOUSE
THE ORIGINAL STARTER FARMHOUSE PLANS


3 2025-08-08 ORIGINAL DESIGN (FINISHED PLANS)
2 2023-10-01 CAROLINE: BLUEPRINTS ON PATREON
1 2023-01-04 STARTER FARMHOUSE SCHEMATICS
+ See A0.1 for more project history and credits

FRONT ELEVATIONS
A2.0


CC BY Attribution Share-Alike by Jay Osborne. These drawings are for informational purposes only. This design and its related documents are provided "as is" with no guarantees or warranties, express or implied. FreeFarmhouse & Jay Osborne disclaim liability for any damages that may result from using this work.

SECTION NOTES

- 1. SEE TYPICAL SECTION DETAIL ON 8/A4.0
- 2. FOUNDATION TO BE ENGINEERED BASED ON SITE-SPECIFIC REQUIREMENTS
- 3. WINDER STAIRS HAVE STRICT REQUIREMENTS. FOR MORE INFO, SEE 5-7/A4.0
- 4. WINDERS CAN BE BUILT AS A SERIES OF PLATFORMS. MAKE SURE TO USE 1-HR FIRE-RATED GYPSUM WALLBOARD SHEATHING UNDER THE STAIRS IN THE UTILITY CLOSET.
- 5. MAINTAIN 80" MIN HEAD CLEARANCE AT STAIRCASE.
- 6. CRAWLSPACE ACCESS CAN BE FROM THE UTILITY CLOSET.

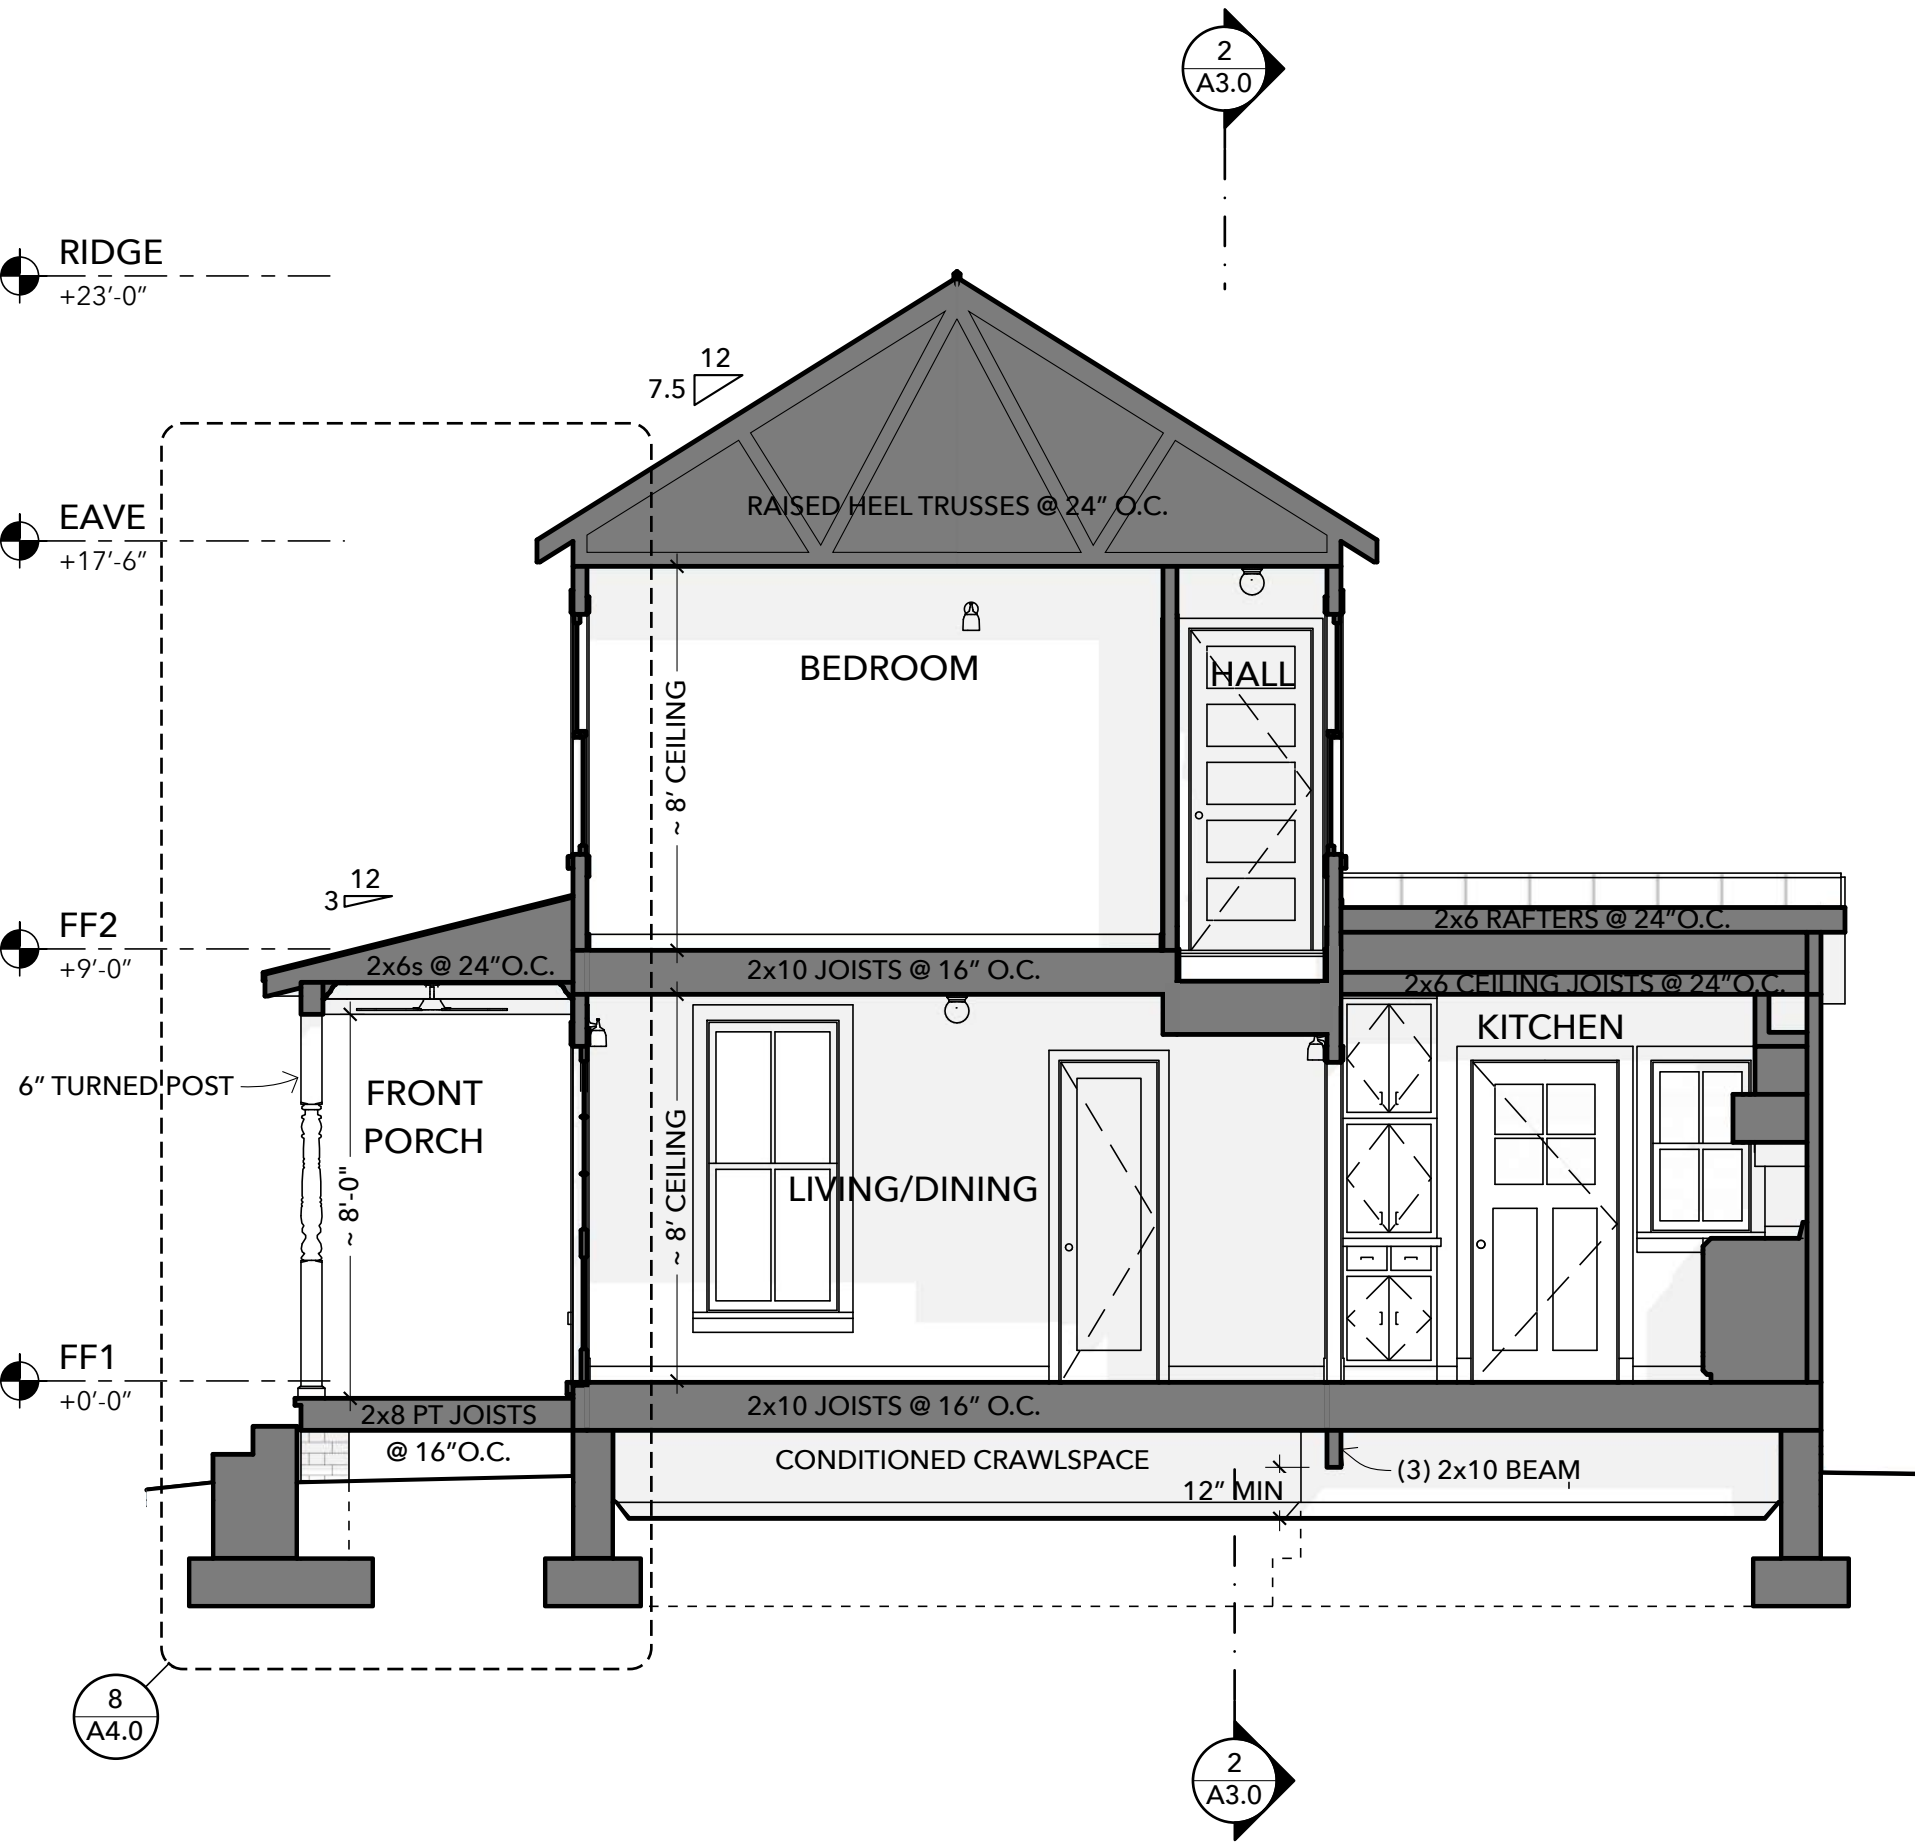

1 TRANSVERSE SECTION
SCALE: 1/4" = 1'-0"

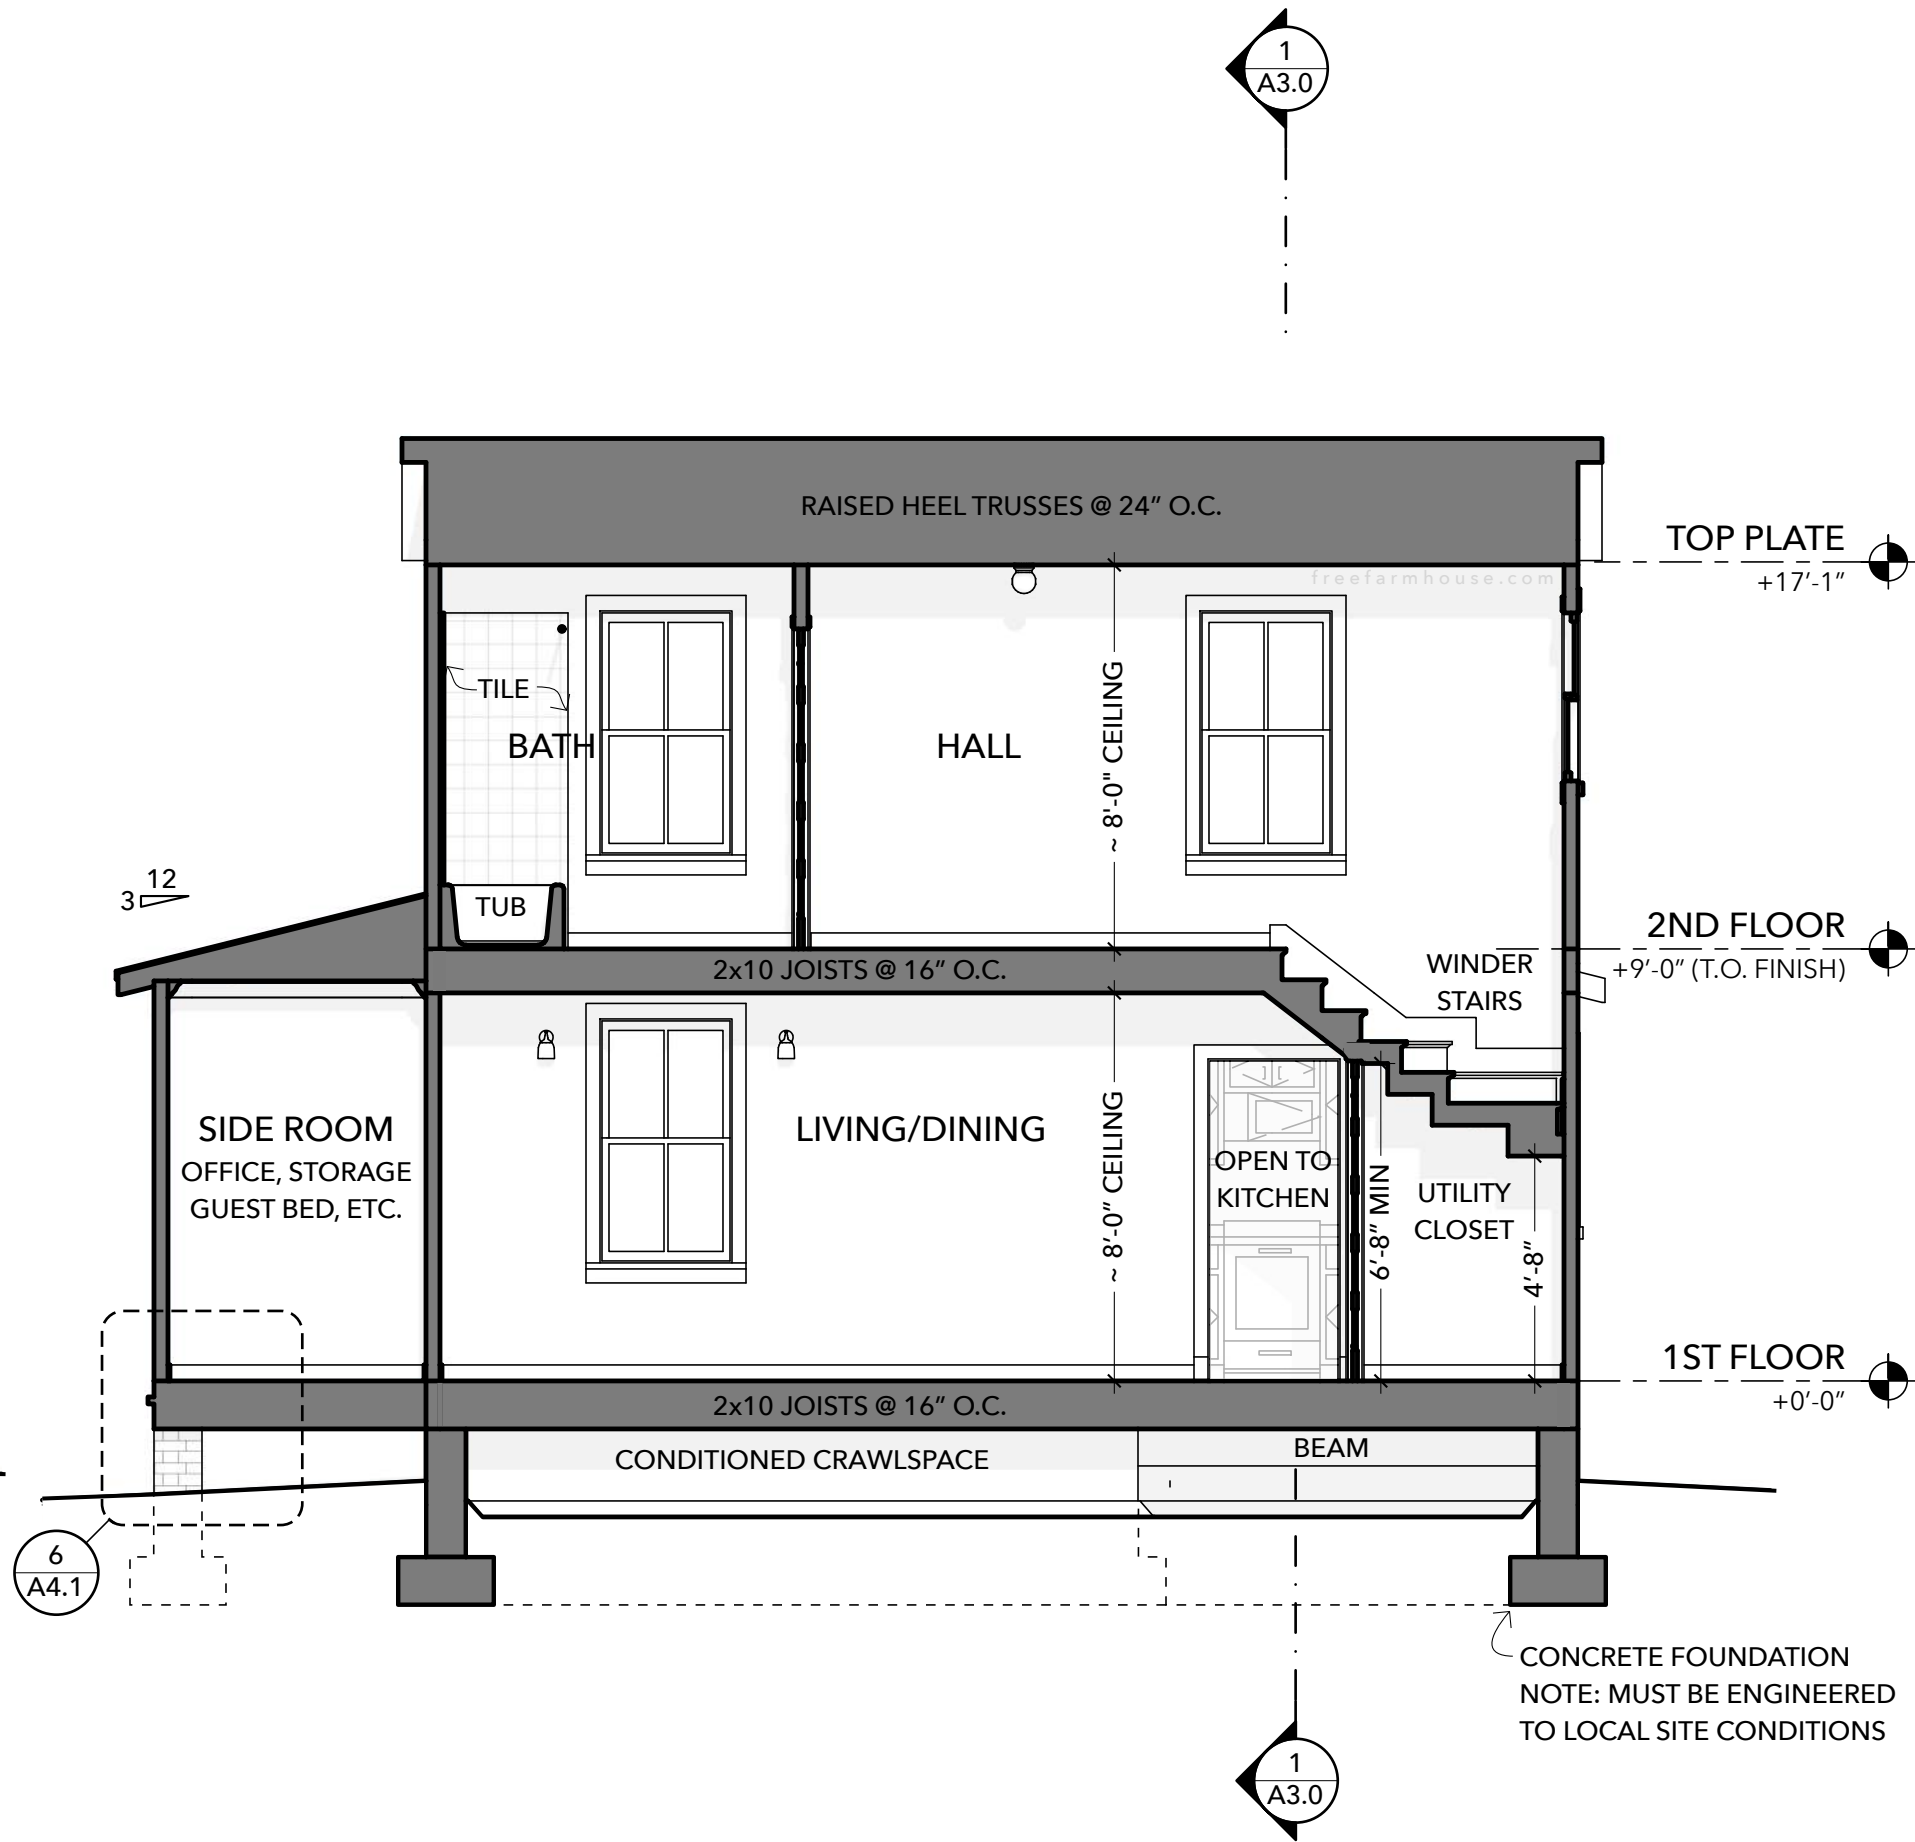

2 LONGITUDINAL SECTION
SCALE: 1/4" = 1'-0"




OPEN-SOURCE ARCHITECTURAL DRAWINGS
You may share, copy, and customize these blueprints.
License: [www.CreativeCommons.org/licenses/by-sa/4.0/](https://creativecommons.org/licenses/by-sa/4.0/)
Some rights reserved. No promises or guarantees given.
Download the free files at www.FreeFarmhouse.com


A DESIGN BY JAY OSBORNE
CAROLINE'S FARMHOUSE
THE ORIGINAL STARTER FARMHOUSE PLANS

- 3 2025-08-08 ORIGINAL DESIGN (FINISHED PLANS)
 - 2 2023-10-01 CAROLINE: BLUEPRINTS ON PATREON
 - 1 2023-01-04 STARTER FARMHOUSE SCHEMATICS
- + See A0.1 for more project history and credits


SECTION VIEWS
A3.0

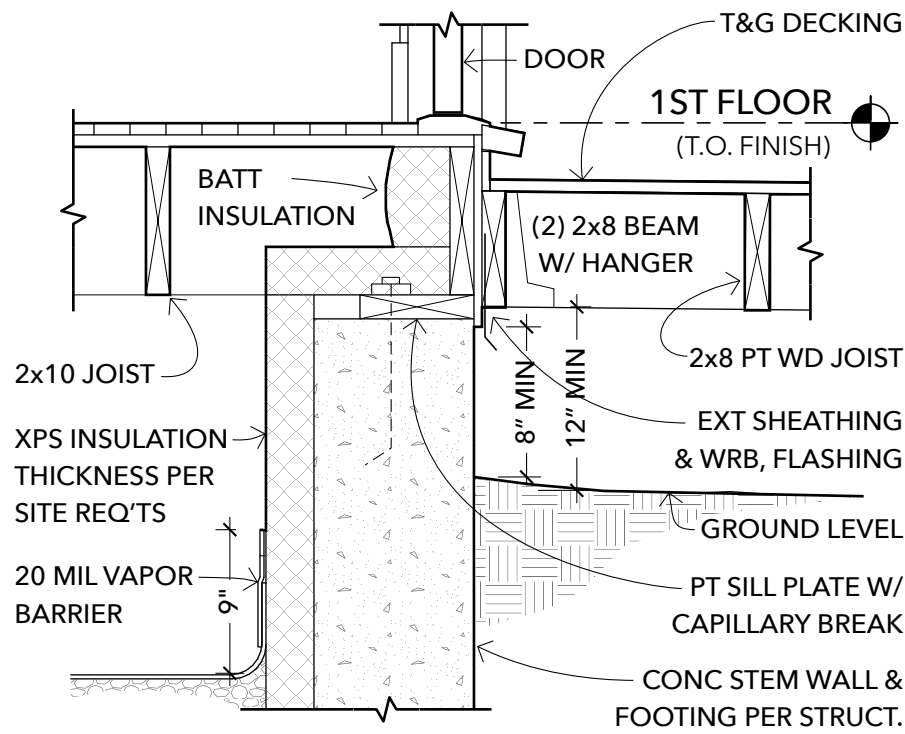


1A FOUNDATION OPT A: CRAWLSPACE
SCALE: 1" = 1'-0" CONDITIONED CRAWLSPACE

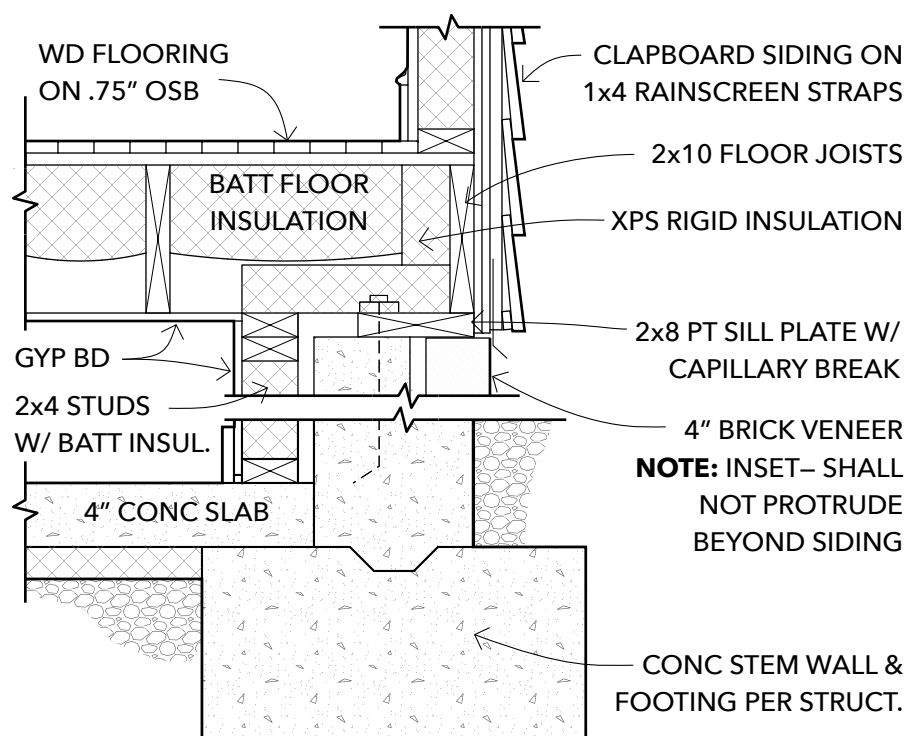


1B FOUNDATION OPT B: BASEMENT
SCALE: 1" = 1'-0" OPTION (PORCH NOT SHOWN)

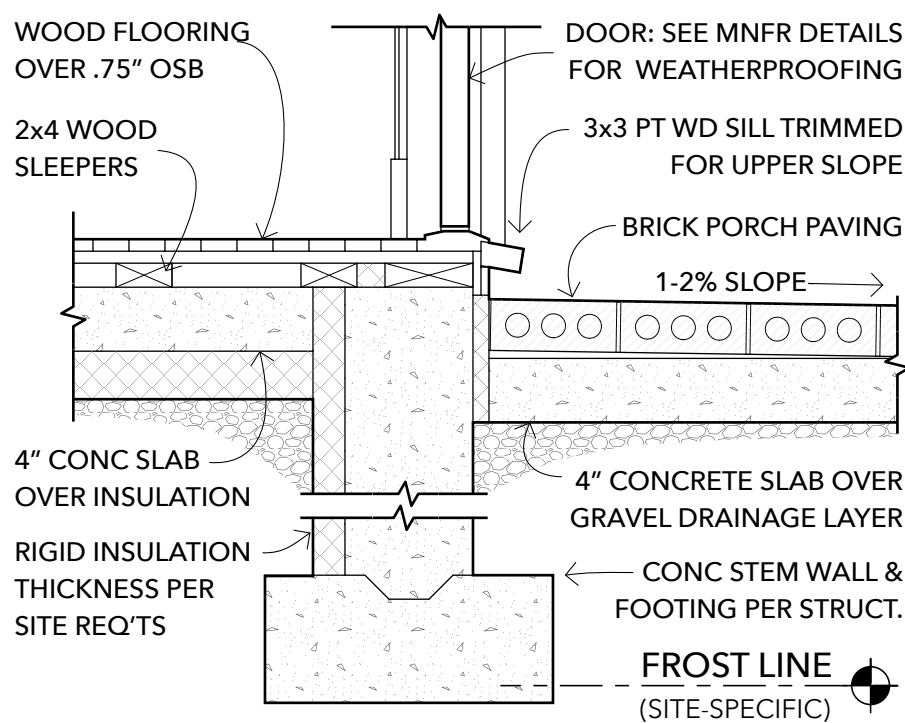


1C FOUNDATION OPTION C: SLAB
SCALE: 1" = 1'-0" UNCOMMON FOR OLD HOUSES

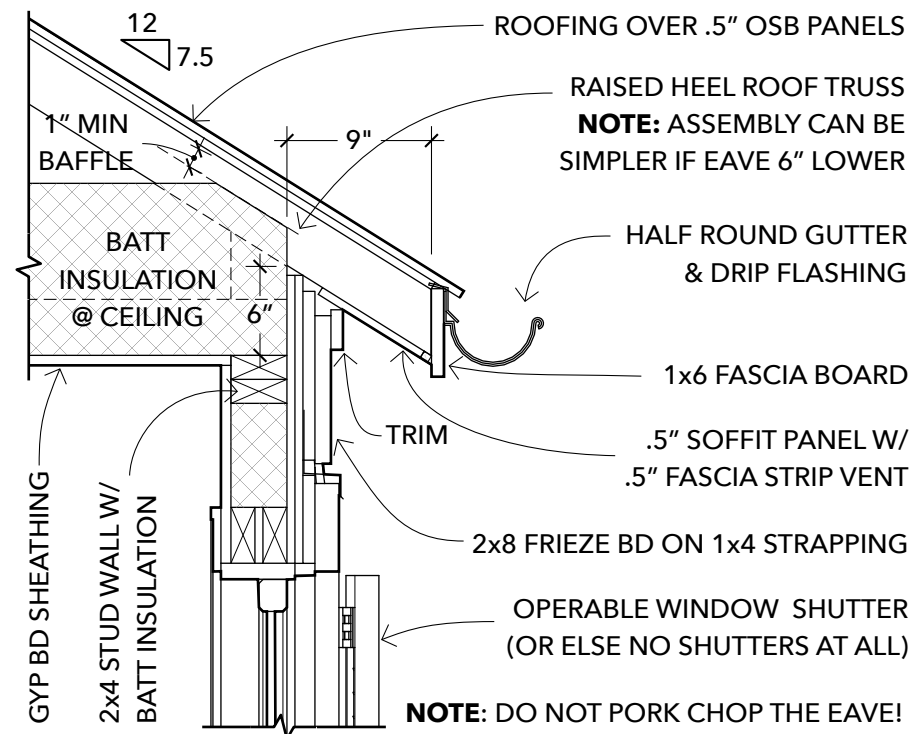


2 MAIN ROOF EAVE DETAIL
SCALE: 1" = 1'-0"

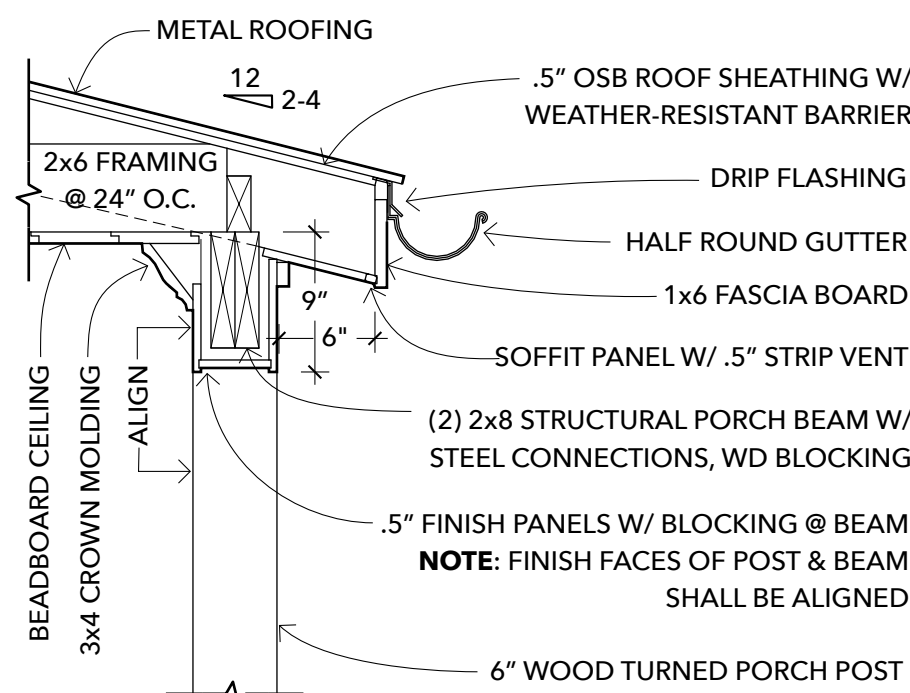


3 PORCH EAVE DETAIL
SCALE: 1" = 1'-0"

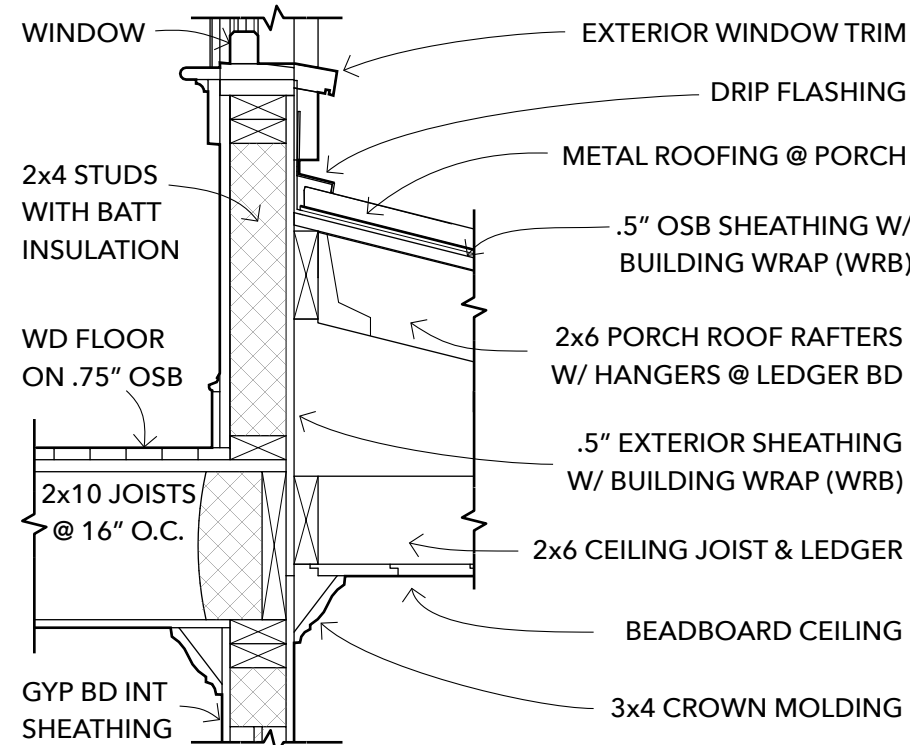


4 PORCH ROOF @ WALL
SCALE: 1" = 1'-0"

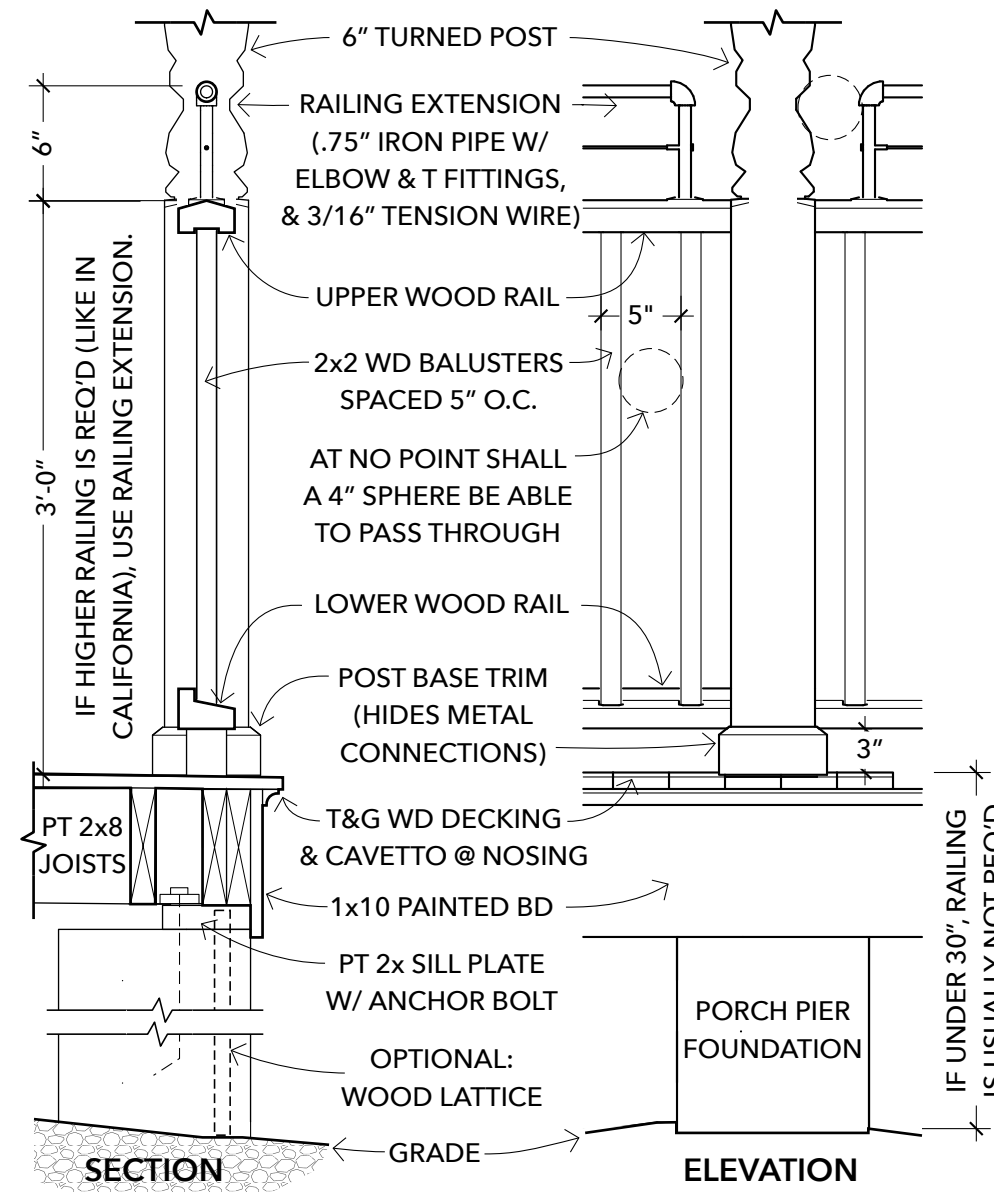


5 PORCH (SHOWS RAILING OPTIONS)
SCALE: 1" = 1'-0" IF 42\"/>

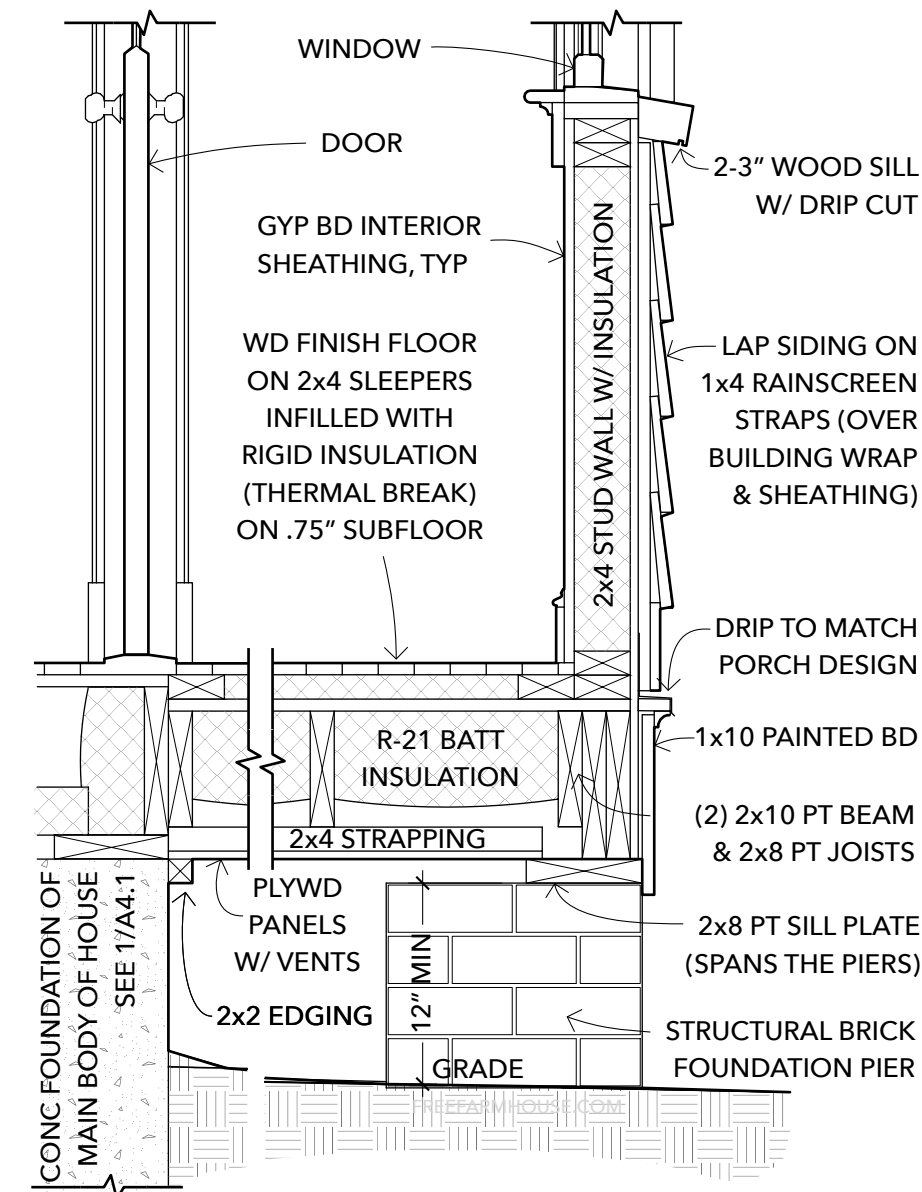


6 INSULATED "PORCH ADDITION"
SCALE: 1" = 1'-0" NOTE: TO BE BUILT IN PHASE 1

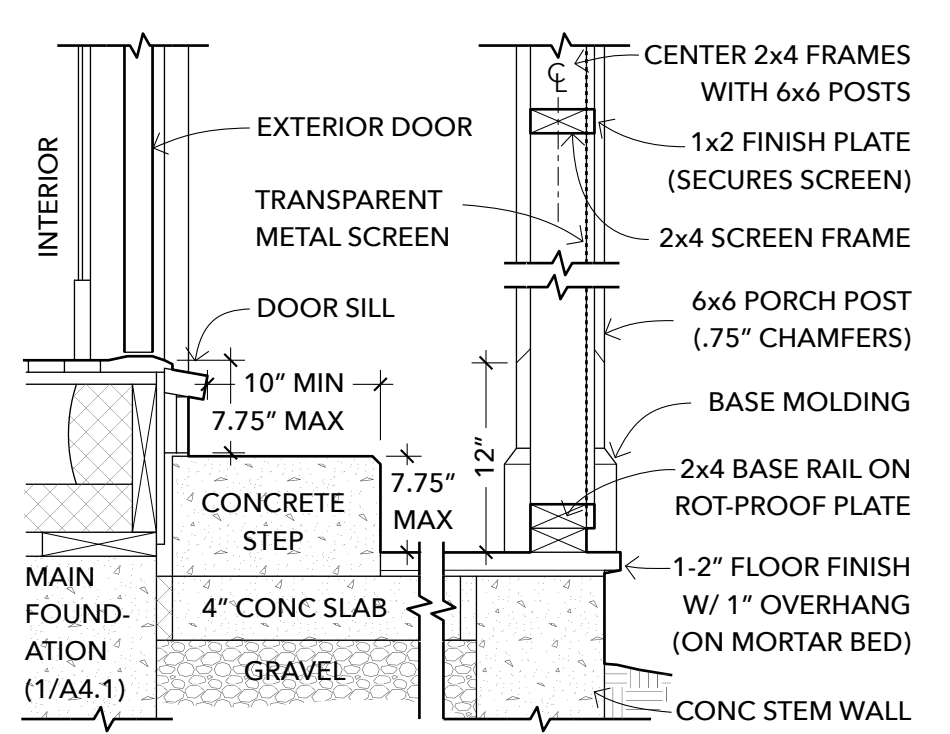


7 SCREEN PORCH @ CONC SLAB
SCALE: 1" = 1'-0"

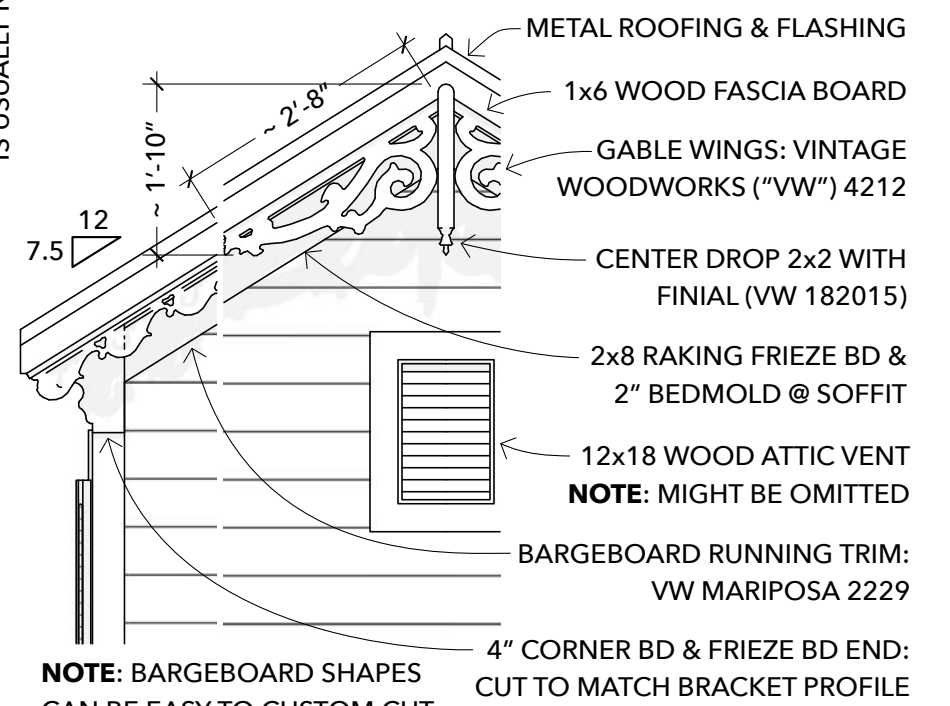

8 GABLE ORNAMENT (OPTION)
SCALE: 1/2" = 1'-0" GINGERBREAD DECORATIONS

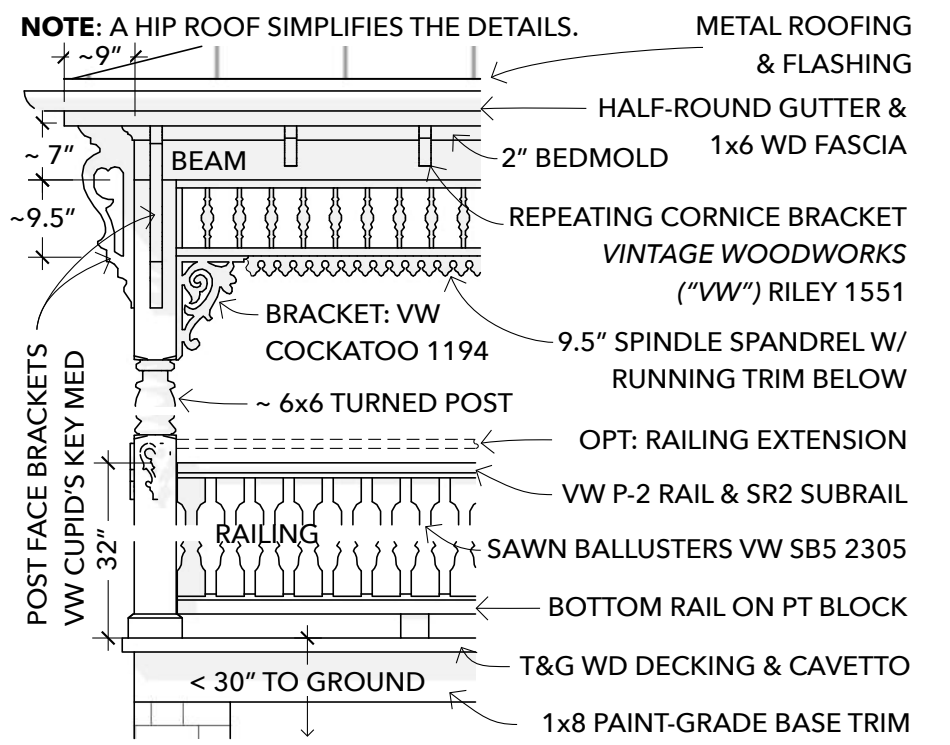

9 PORCH ORNAMENT (OPTION)
SCALE: 1/2" = 1'-0" GINGERBREAD DECORATIONS

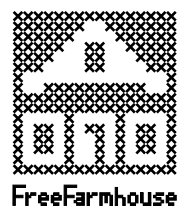

OPEN-SOURCE ARCHITECTURAL DRAWINGS
You may share, copy, and customize these blueprints.
License: [www.CreativeCommons.org/licenses/by-sa/4.0](https://creativecommons.org/licenses/by-sa/4.0/)
Some rights reserved. No promises or guarantees given.
Download the free files at www.FreeFarmhouse.com

A DESIGN BY JAY OSBORNE
CAROLINE'S FARMHOUSE
THE ORIGINAL STARTER FARMHOUSE PLANS

3 2025-08-08 ORIGINAL DESIGN (FINISHED PLANS)
2 2023-10-01 CAROLINE: BLUEPRINTS ON PATREON
1 2023-01-04 STARTER FARMHOUSE SCHEMATICS

+ See A0.1 for more project history and credits

EXTERIOR DETAILS
& OPTIONS
A4.1

MARK	ITEM	SIZE	MATERIAL	NOTES	MANUFACTURER / MODEL
F-00	BRICK	-	SMOOTH BRICK	SOLID RED COLOR, SAND-FACED, AVOID WIRE CUT OR "EXTRUDED" LOOK	OLD CAROLINA BRICK COMPANY
F-02	PORCH DECKING	1x4	PAINTED WOOD	TONGUE & GROOVE, UNPAINTED CEDAR PREFERRED, PAINTED WORKS FINE	RECLAIMED PREFERRED
F-04	PORCH COLUMNS	6x6	PAINTED WOOD	TURNED PORCH POSTS (ALTERNATIVELY: 6x6 POSTS WITH CHAMFERED EDGES)	-
F-20	CLAPBOARD SIDING	6"	FIBER CEMENT	VINYL AND ALUMINUM SIDING ARE FORBIDDEN (DETAILS NEVER LOOK RIGHT).	JAMES HARDIE / ARTISAN LAP SIDING
F-22	EXT OPENING CASING	5-6"	FIBER CEMENT	FOR ALL SIDING, WOOD IS STILL AN OPTION. CEDAR PREFERRED.	HARDIPLANK OR 2x LUMBER
F-24	BED MOLDING	2.5", 4"	ROT-RESISTANT	PAINTED. EXTERIOR-GRADE. WOOD PREFERRED.	-
F-26	ASTRAGAL	1"	ROT-RESISTANT	PAINTED. VARIOUS EXTERIOR-GRADE MATERIAL OPTIONS ARE OKAY HERE	-
F-28	CROWN MOLDING	3-6"	ROT-RESISTANT	PAINTED. EXTERIOR-GRADE. WOOD PREFERRED.	-
F-40	STANDING SEAM ROOF	16" O.C.	GALVALUME	METAL. NO CORRUGATIONS. USE 5V PANELS FOR ECONOMICAL OPTION.	-
F-42	HALF-ROUND GUTTER	5" DIA	COPPER	GALV STEEL ALSO AN OPTION. ADJUST SIZE ACCORDING TO CLIMATE.	-
F-44	KITCHEN COUNTERTOP	1.5-2"	-	CHOOSE: QUARTZ, BUTCHER BLOCK, PORCELAIN TILE, GRANITE, SOAPSTONE	CHOICE BY HOMEOWNER.
F-48	BATHROOM COUNTERTOP	1.5-2"	-	CHOOSE: CERAMIC, QUARTZ, PORCELAIN, BUTCHER BLOCK, GRANITE, MARBLE	CHOICE BY HOMEOWNER.
F-50	HARDWOOD FLOOR	2-3" BDS	FINISH WOOD	TONGUE & GROOVE, STAINED. CREATE FLOOR PATTERNS AS DESIRED.	RECLAIMED PREFERRED.
F-52	FLOOR TILE	1-2" HEX	CERAMIC	HEXAGONAL PATTERN. WHITE COLOR, SMALLEST TILES PREFERRED	-
F-60	WALL TILE	4" SQ	CERAMIC	WHITE SUBWAY TILE, OR CHOICE BY HOMEOWNER.	-
F-62	BASE MOLDING	.5"x5"	FINISH WOOD	MAY INCLUDE DECORATIVE BASE CAP MOLDING.	-
F-64	INT OPENING CASING	.5"x5"	WOOD	PAINTED, WITH .1"-THICK PLINTH BLOCK AT BASE	-
F-68	BEADBOARD	1/2"	COMPOSITE PANEL	EXTERIOR GRADE BEADBOARD TO BE USED AT PORCH CEILING.	-
F-74	HANDRAIL	2"	FINISH WOOD	STAINED SAME COLOR AS FLOOR. MAKE SURE TO FOLLOW ALL REGULATIONS.	-
F-76	NEWEL POST (OPT)	4x4	WOOD	PAINTED, MODESTLY DECORATIVE. RECLAIMED/ANTIQUE PREFERRED.	-
F-78	BALUSTERS	2x2	WOOD	PAINTED, MODESTLY DECORATIVE. RECLAIMED/ANTIQUE PREFERRED.	-
F-79	CROWN MOLDING	4-6"	WOOD	PAINT-GRADE	-
F-80	WINDOW SHUTTERS	SEE NOTE	WOOD/COMPOSITE	SHUTTERS SHALL BE OPERABLE, AND SIZED TO EACH WINDOW.	- TIMBERLANE. OR BOARD & BATTEN.

1

MATERIALS SCHEDULE


PRODUCTS ARE RECOMMENDATIONS (ADD "OR SIMILAR" TO EACH), BUT NOTES SHOULD BE HEDEED

MARK	ITEM	SIZE	NOTES	MANUFACTURER / MODEL
X-00	REFRIGERATOR	24" MAX WIDTH	ENERGY STAR, COUNTER DEPTH (24" DEPTH STRONGLY PREFERRED)	BLOMBERG BRFB1042SS
X-02	KITCHEN SINK	24" UNIT WIDTH	DOUBLE OR SINGLE BOWL, VITREOUS CHINA PREFERRED	HIGHPOINT COLLECTION OR SINKOLOGY FIRECLAY
X-04	RANGE / OVEN	24"x24"x36"	-	-
X-06	MICROWAVE/HOOD	24" WIDTH	FOR SIZE FLEXIBILITY, CABINET ABOVE THIS UNIT MAY BE OPEN SHELVING	FRIGIDAIRE UMV1422 US
X-08	WATER FAUCET	-	CHOICE BY HOMEOWNER.	-
X-12	DISHWASHER (OPT)	24" WIDTH	-	-
X-16	FLOOR CABINETS	VARIES	FOR AN ECONOMICAL OPTION, USE IKEA UNITS WITH CUSTOM DOORS.	IKEA / SEKTION
X-18	WALL CABINETS	VARIES	GLASS DOORS, WITH MANY PANES, PREFERRED. DOORS MAY BE BUILT DIY.	IKEA / SEKTION
X-20	TOILET	26"x18"	SINGLE BOWL, VITREOUS CHINA. [FREEFARMHOUSE.COM] STANDARD SIZE.	TOTO / ROWAN CST405MF OR EQUIVALENT
X-26	BATHROOM VANITY	30"(& 36") WIDE	CABINETS AND COUNTERTOP SURFACES TO BE CHOSEN BY HOMEOWNER.	-
X-30	BATHTUB	30x48	WALL TILE. GLASS DOORS OR CURTAIN. SEAT W/ SINGLE SLAB OF STONE	-
X-62	WASHER DRYER COMBO	30x30x72 MAX	VENTLESS, COMPACT (STACKED UNITS ALSO WORK IN JUNE & APRIL ALCOVES)	HAIER / HWD1600BW
X-68	WATER HEATER	17x15x5	WALL-MOUNTED, TANKLESS, INSTANT WATER HEATER.	STIEBEL ELTRON TEMPRA

2

FIXTURES SCHEDULE


PRODUCTS ARE RECOMMENDATIONS (ADD "OR SIMILAR" TO EACH), BUT NOTES SHOULD BE HEDEED

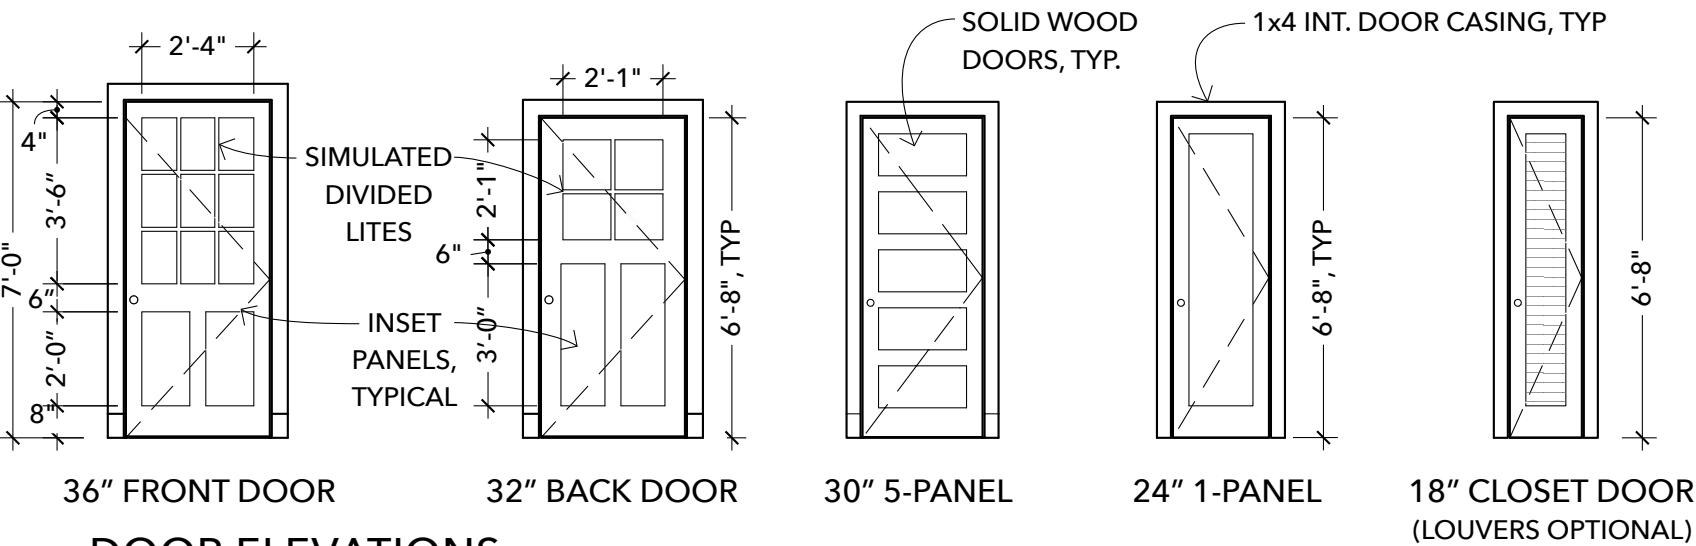

5

DOOR ELEVATIONS

SCALE: 1/4" = 1'-0" NOTE: 32" CLEAR OPENING REQ'D AT FRONT DOOR (ACCOUNT FOR DOOR THICKNESS & HINGE).

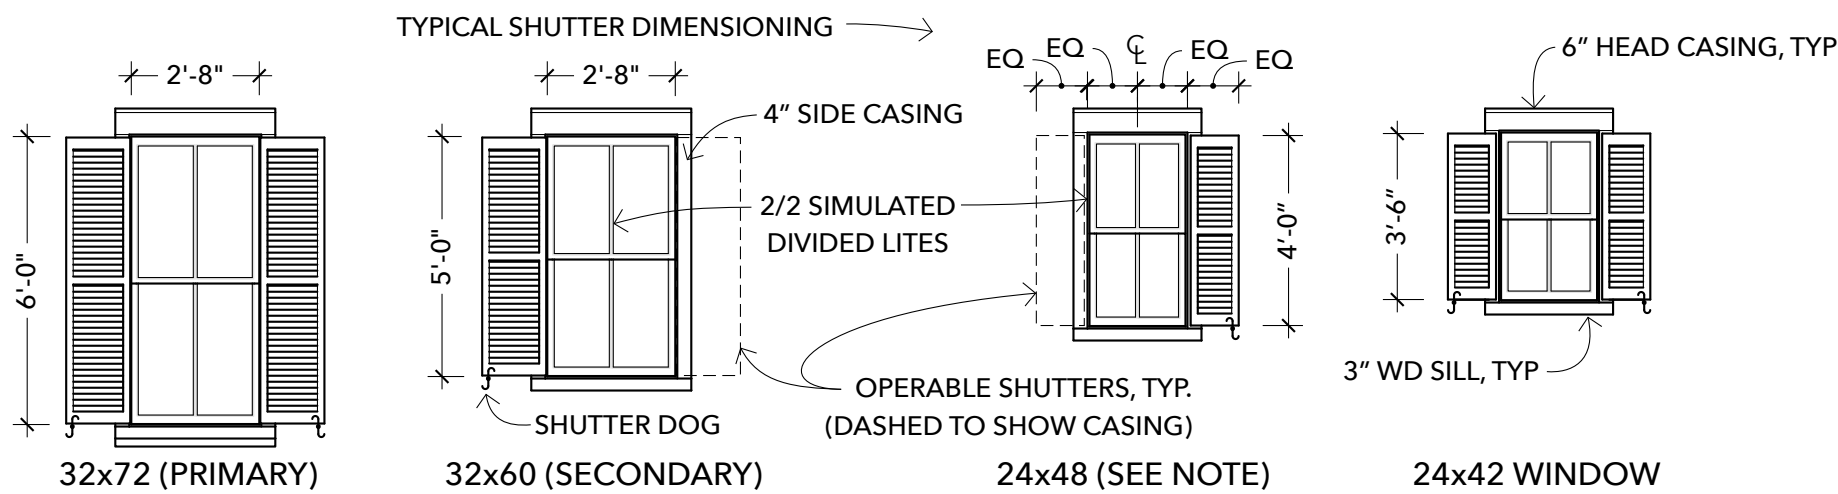

6

WINDOW ELEVATIONS

SCALE: 1/4" = 1'-0" NOTE: 24x48 WINDOW MAY BE REPLACED BY 24x42 WINDOW. MAINTAIN HEADER HEIGHTS.

ITEM	MANUFACTURER / MODEL
INTERIOR CEILING LIGHT SCONCE	-
INTERIOR WALL LIGHT SCONCE	-
KIT. WASTE CABINET HARDWARE	-
KIT. SINK HARDWARE	-
SHOWER HARDWARE	-
BATH SINK HARDWARE	-
WINDOW SHUTTER HARDWARE	-
(OPT) PORCH HANGING LIGHT	-
(OPT) KITCHEN FLOORING (IF UNIQUE)	-

GINGERBREAD ORNAMENT OPTIONS: (**NOTE: VW = "VINTAGE WOODWORKS"**)

- PORCH BRACKET - VW COCKATOO 1194
- REPEATING CORNICE BRACKET (PORCH) - VW: EMMA 1560 (~6"x6")
- POST FACE BRACKET - VW "CUPID'S KEY" MEDIUM
- REPEATING CORNICE BRACKET (EAVE) - VW RILEY 1551
- GABLE WING - VW 4212
- CENTER DROP - 2x2, FINIAL (VW 182015)
- BARGEBOARD RUNNING TRIM - VW MARIPOSA 2229
- SAWN BALLUSTERS - VW SB5 2305
- PORCH RAILING - VW P-2 RAIL & SR2 SUBRAIL

SIMPLER ORNAMENT:

- REPEATING CORNICE BRACKET - VW: RILEY 1551

3

ADDITIONAL PRODUCT CHOICES

NOTE: MAY BE OMITTED, OR GIVEN MULTIPLE OPTIONS.

FINAL NOTES & FURTHER READING

ARCHITECTURAL PLANS NEVER HAVE ALL OF THE INFORMATION A BUILDER COULD NEED. BY PRACTICAL NECESSITY, PLANS ALWAYS OMIT SOME USEFUL IDEAS OR EXPLANATIONS. CODE DIAGRAMS CAN BE PLACED IN THE PLANS, AND SHOP DRAWINGS MAY BE INCLUDED – YET SUCH INFORMATION IS ALWAYS BETTER PRESENTED BY ALTERNATIVE METHODS. SO AS A SUPPLEMENT TO THESE DRAWINGS, HERE IS A LIST OF SOME USEFUL RESOURCES:

- IF THE DESIGN IS BEING MODIFIED**, ONE OF THESE (YOUR PICK) IS REQUIRED READING:
- "GET YOUR HOUSE RIGHT", BY MARIANNE CUSATO & BEN PENTREATH
 - "TRADITIONAL CONSTRUCTION PATTERNS", BY STEPHEN MOUZON & SUSAN HENDERSON


- FOR TECHNICAL INFORMATION AND GUIDANCE:**
- "SKETCHUP & LAYOUT FOR ARCHITECTURE", BY NICK SONDER (THE SOFTWARE USED HERE)
 - "RESIDENTIAL BUILDING CODES ILLUSTRATED", BY FRANCIS CHING AND OTHERS

- FOR A BIG PICTURE UNDERSTANDING:**
- "A PATTERN LANGUAGE", BY CHRISTOPHER ALEXANDER (GENERAL DESIGN PRINCIPLES)
 - "HOW BUILDINGS LEARN", BY STEWART BRAND (ADAPTABLE ARCHITECTURE STRATEGIES)

4

NOTES & ADDITIONAL RESOURCES

INCLUDING REQUIRED & RECOMMENDED READING

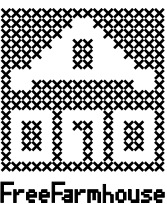

OPEN-SOURCE ARCHITECTURAL DRAWINGS
You may share, copy, and customize these blueprints.
License: [www.CreativeCommons.org/licenses/BY-SA/4.0](https://creativecommons.org/licenses/by-sa/4.0/)
Some rights reserved. No promises or guarantees given.
Download the free files at www.FreeFarmhouse.com


A DESIGN BY JAY OSBORNE
CAROLINE'S FARMHOUSE
THE ORIGINAL STARTER FARMHOUSE PLANS

- 3** 2025-08-08 ORIGINAL DESIGN (FINISHED PLANS)
- 2** 2023-10-01 CAROLINE: BLUEPRINTS ON PATREON
- 1** 2023-01-04 STARTER FARMHOUSE SCHEMATICS

+ See A0.1 for more project history and credits

SCHEDULES


A5.0

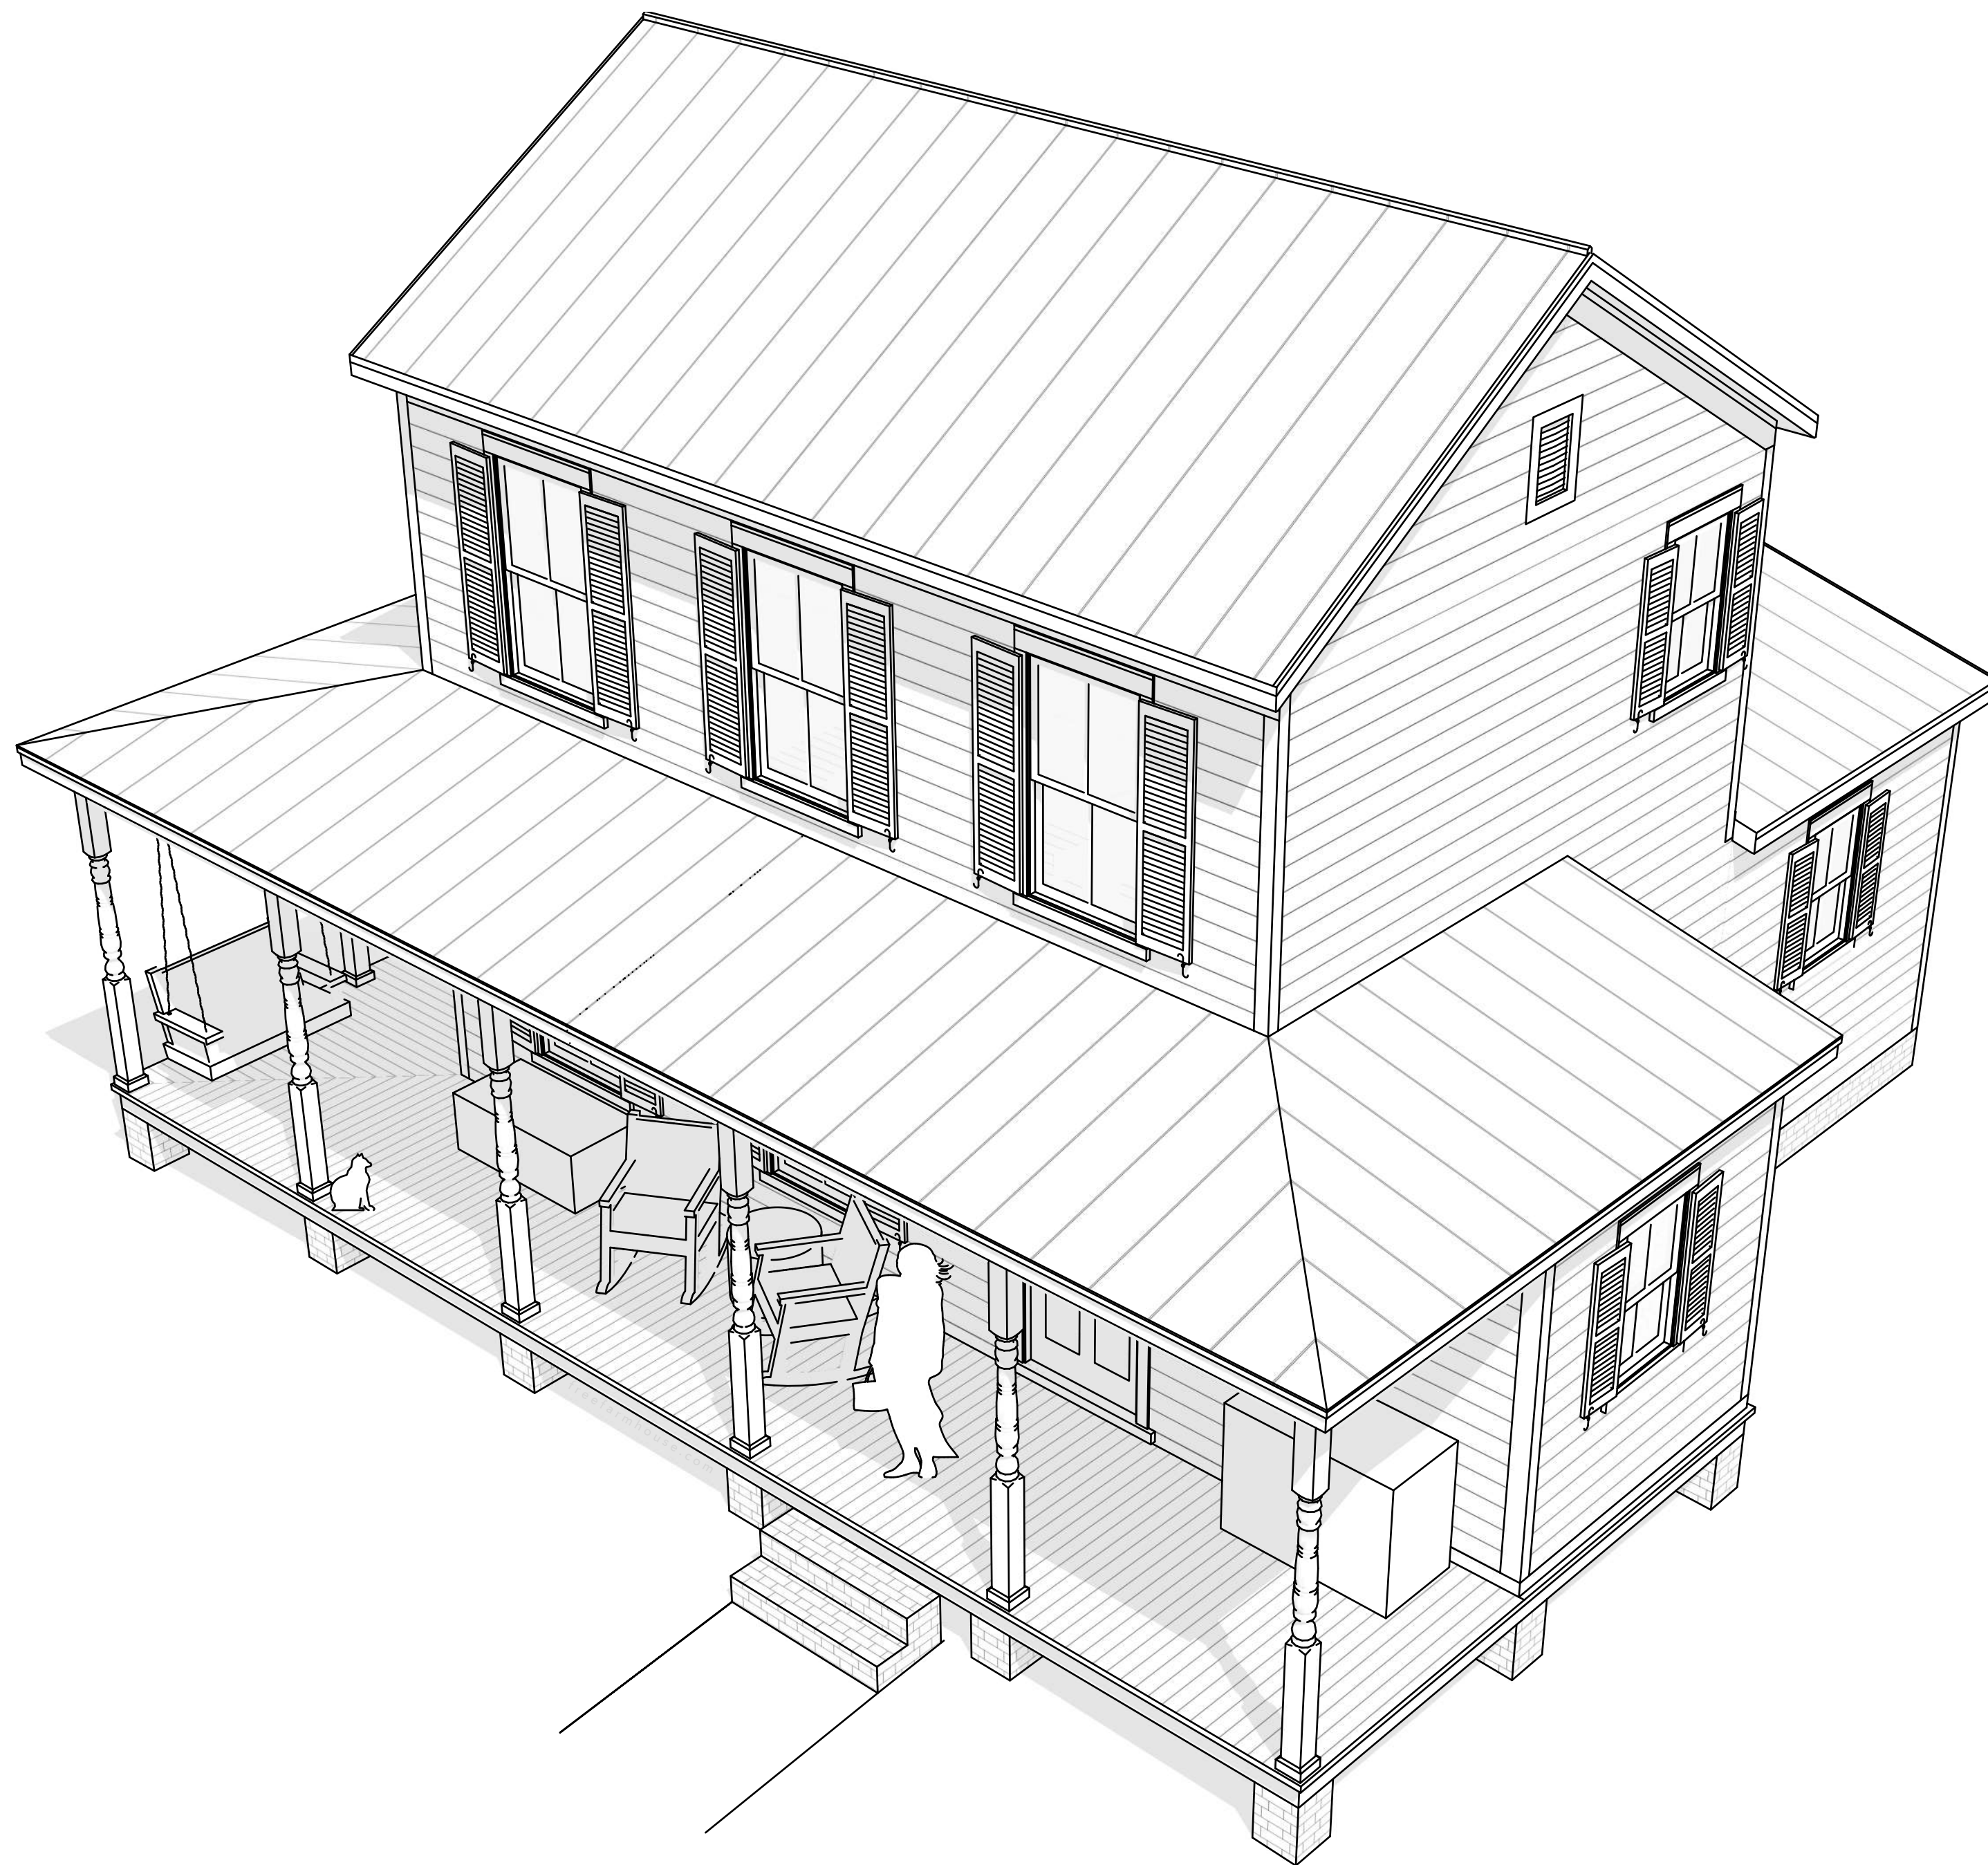

My Starter Farmhouses are designed with interchangeable options (like porches, interior layouts, and rear additions). Caroline's variation includes an open living area and a wrap-around porch. Also, this variation has many additions: a kitchen and screen porch, a downstairs bathroom, and tiny bonus room (which can be an office or guest room). Altogether, this house is still only 920 square feet in size.

CAROLINE'S STARTER FARMHOUSE
DESIGN OVERVIEW
A DESIGN BY JAY OSBORNE


Each of the Starter Farmhouse designs begin as a 16x24 primary massing – about 750 square feet at the smallest. In a time before 30-year mortgages, houses usually started this small and grew as needed. These additions gave a sense of personality and charm to each house. Likewise, you'll be able to enlarge this design by choosing from a series of additions. Or you can build it all at once.

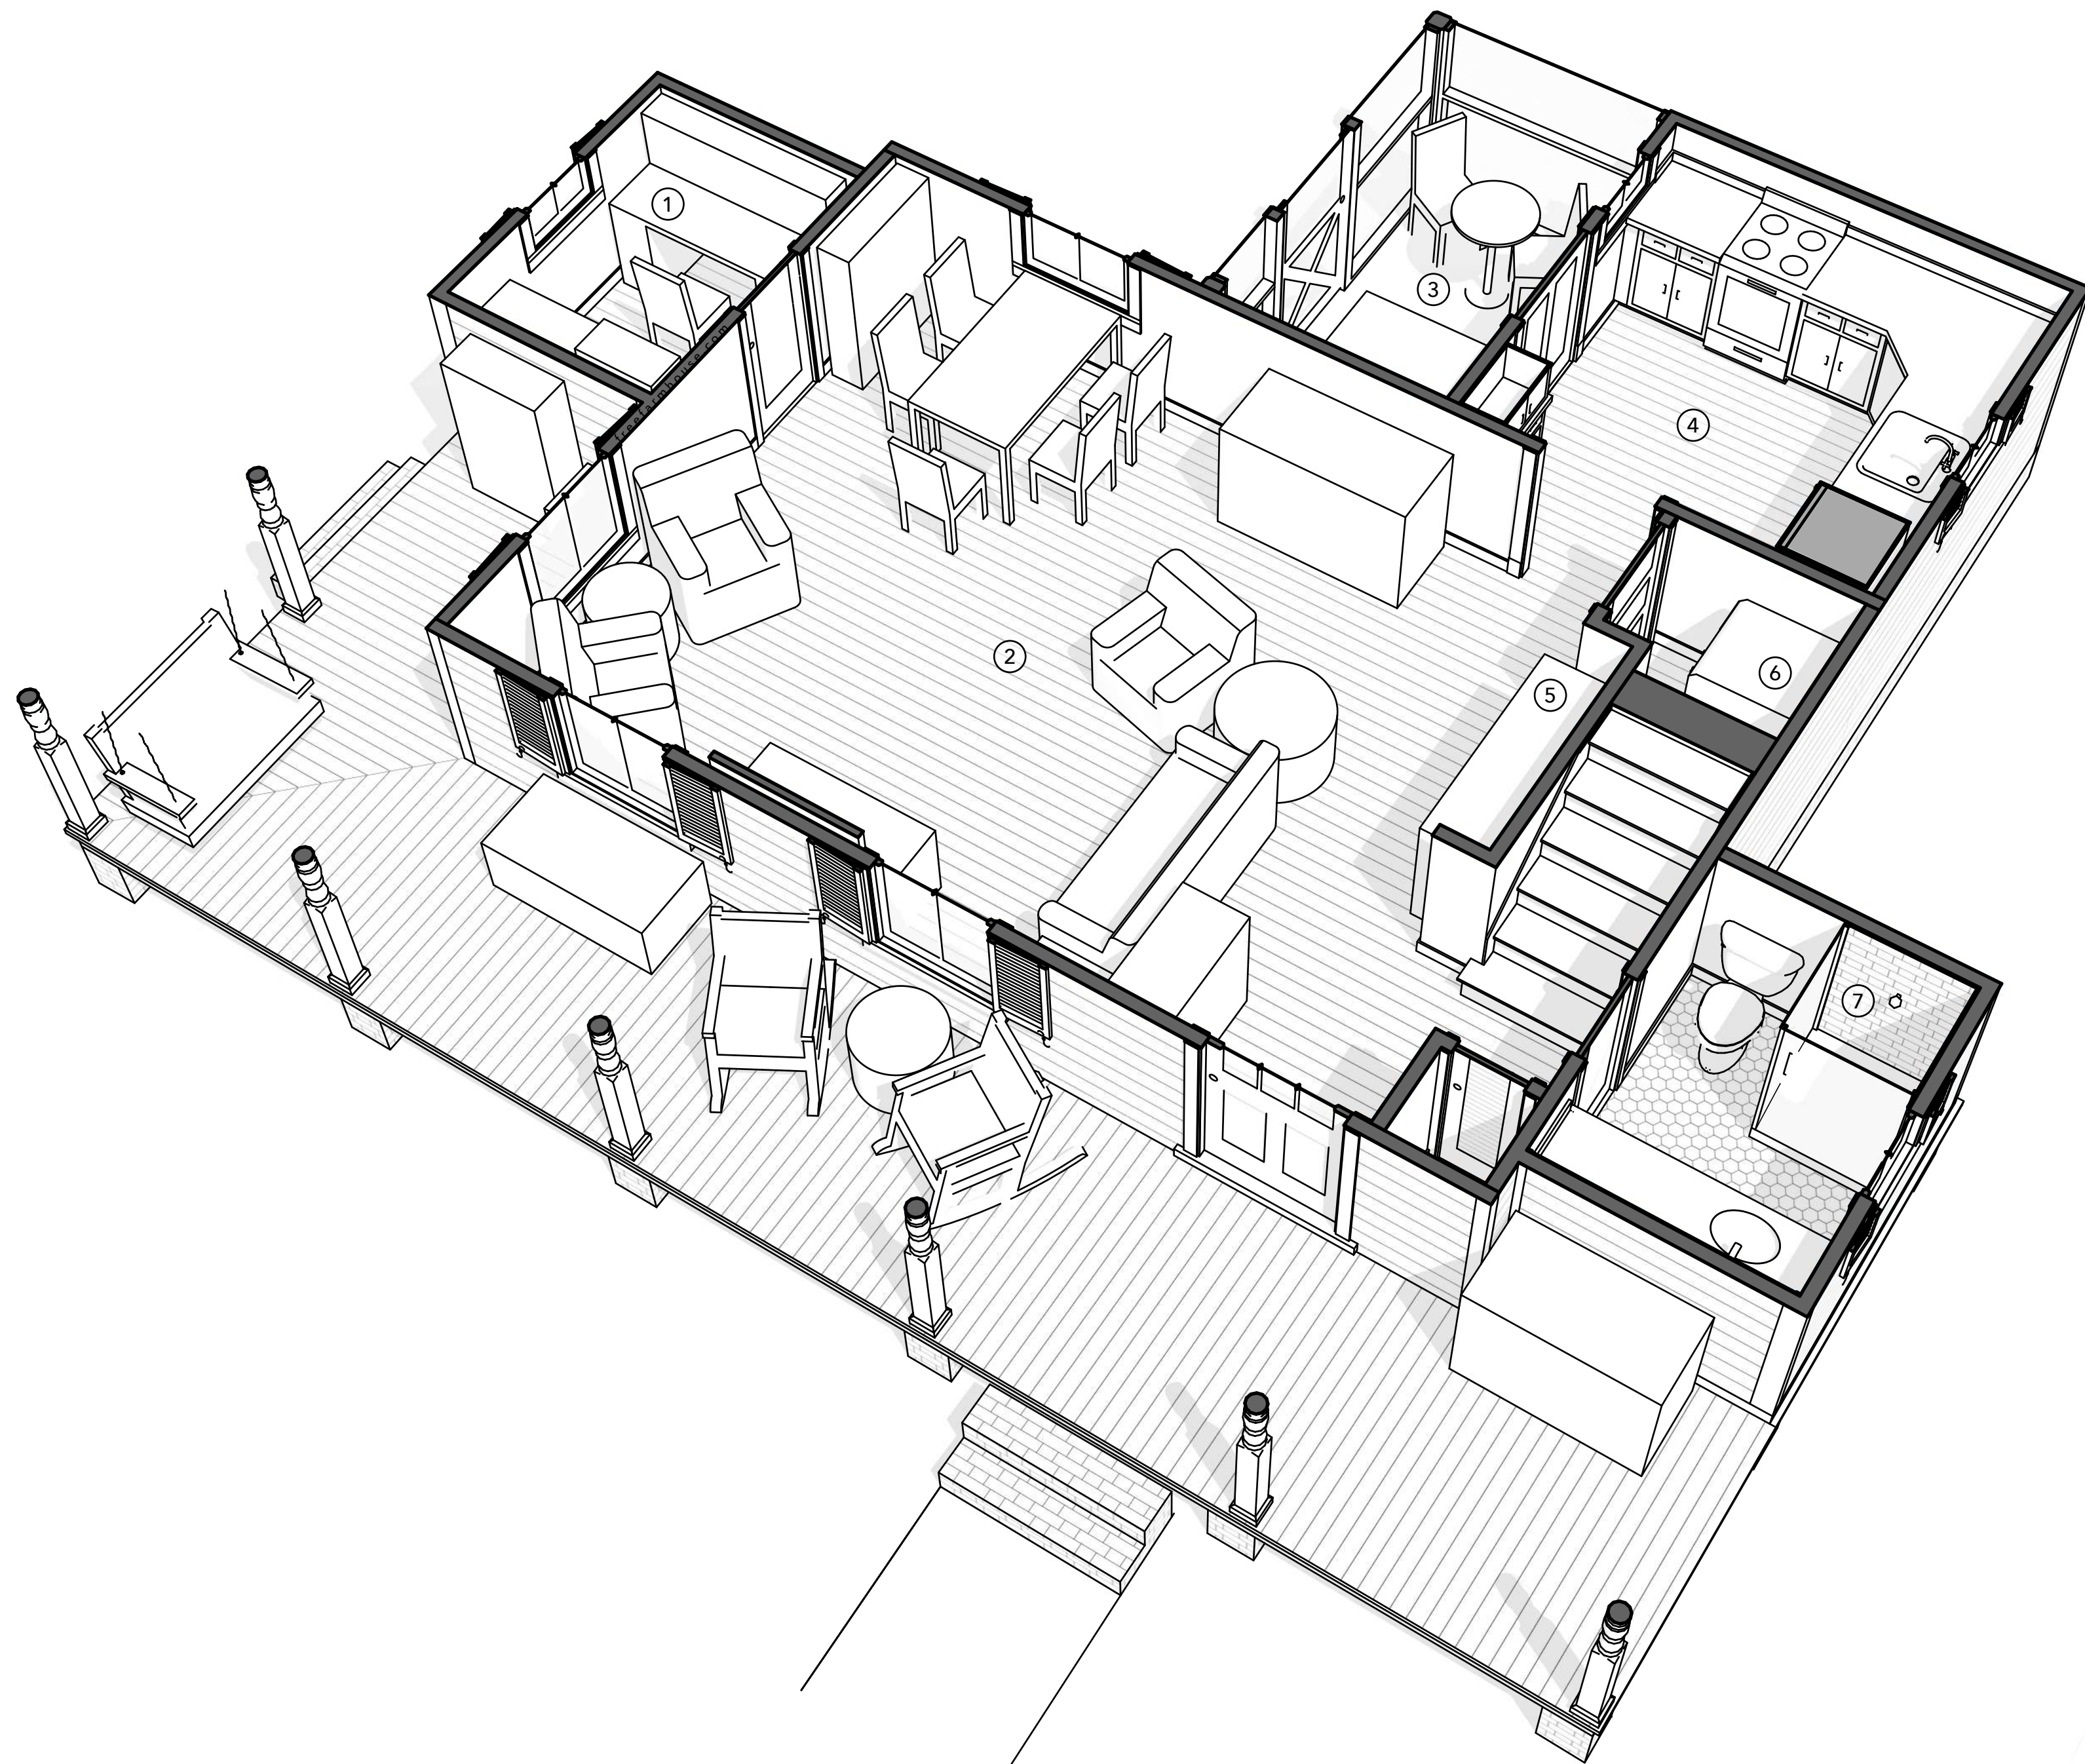

(1) A tiny office is shown here, but it could be storage, laundry, or even a guest bedroom. It would be a true “bed-room”, with only space for a queen-size bed and a shelving unit. **(2)** The lower level of this house is arranged in an open plan. Because of this layout, it can work well for large gatherings. However, it also retains intimacy and formality by placing utilitarian functions in separate rooms.

CAROLINE'S STARTER FARMHOUSE
DOWNSTAIRS PLAN
 A DESIGN BY JAY OSBORNE

(3) The screen porch to the rear can function as a mudroom. **(4)** This kitchen isn't an “exhibition kitchen” open to the living area. You don't need to keep it spotless just in case you have visitors. **(5)** This wall could hold various functions: built-in cabinets, coat hooks, a movie screen, or a woodstove. **(6)** The laundry closet. **(7)** Stacked laundry machines could be included here, instead of this shower.

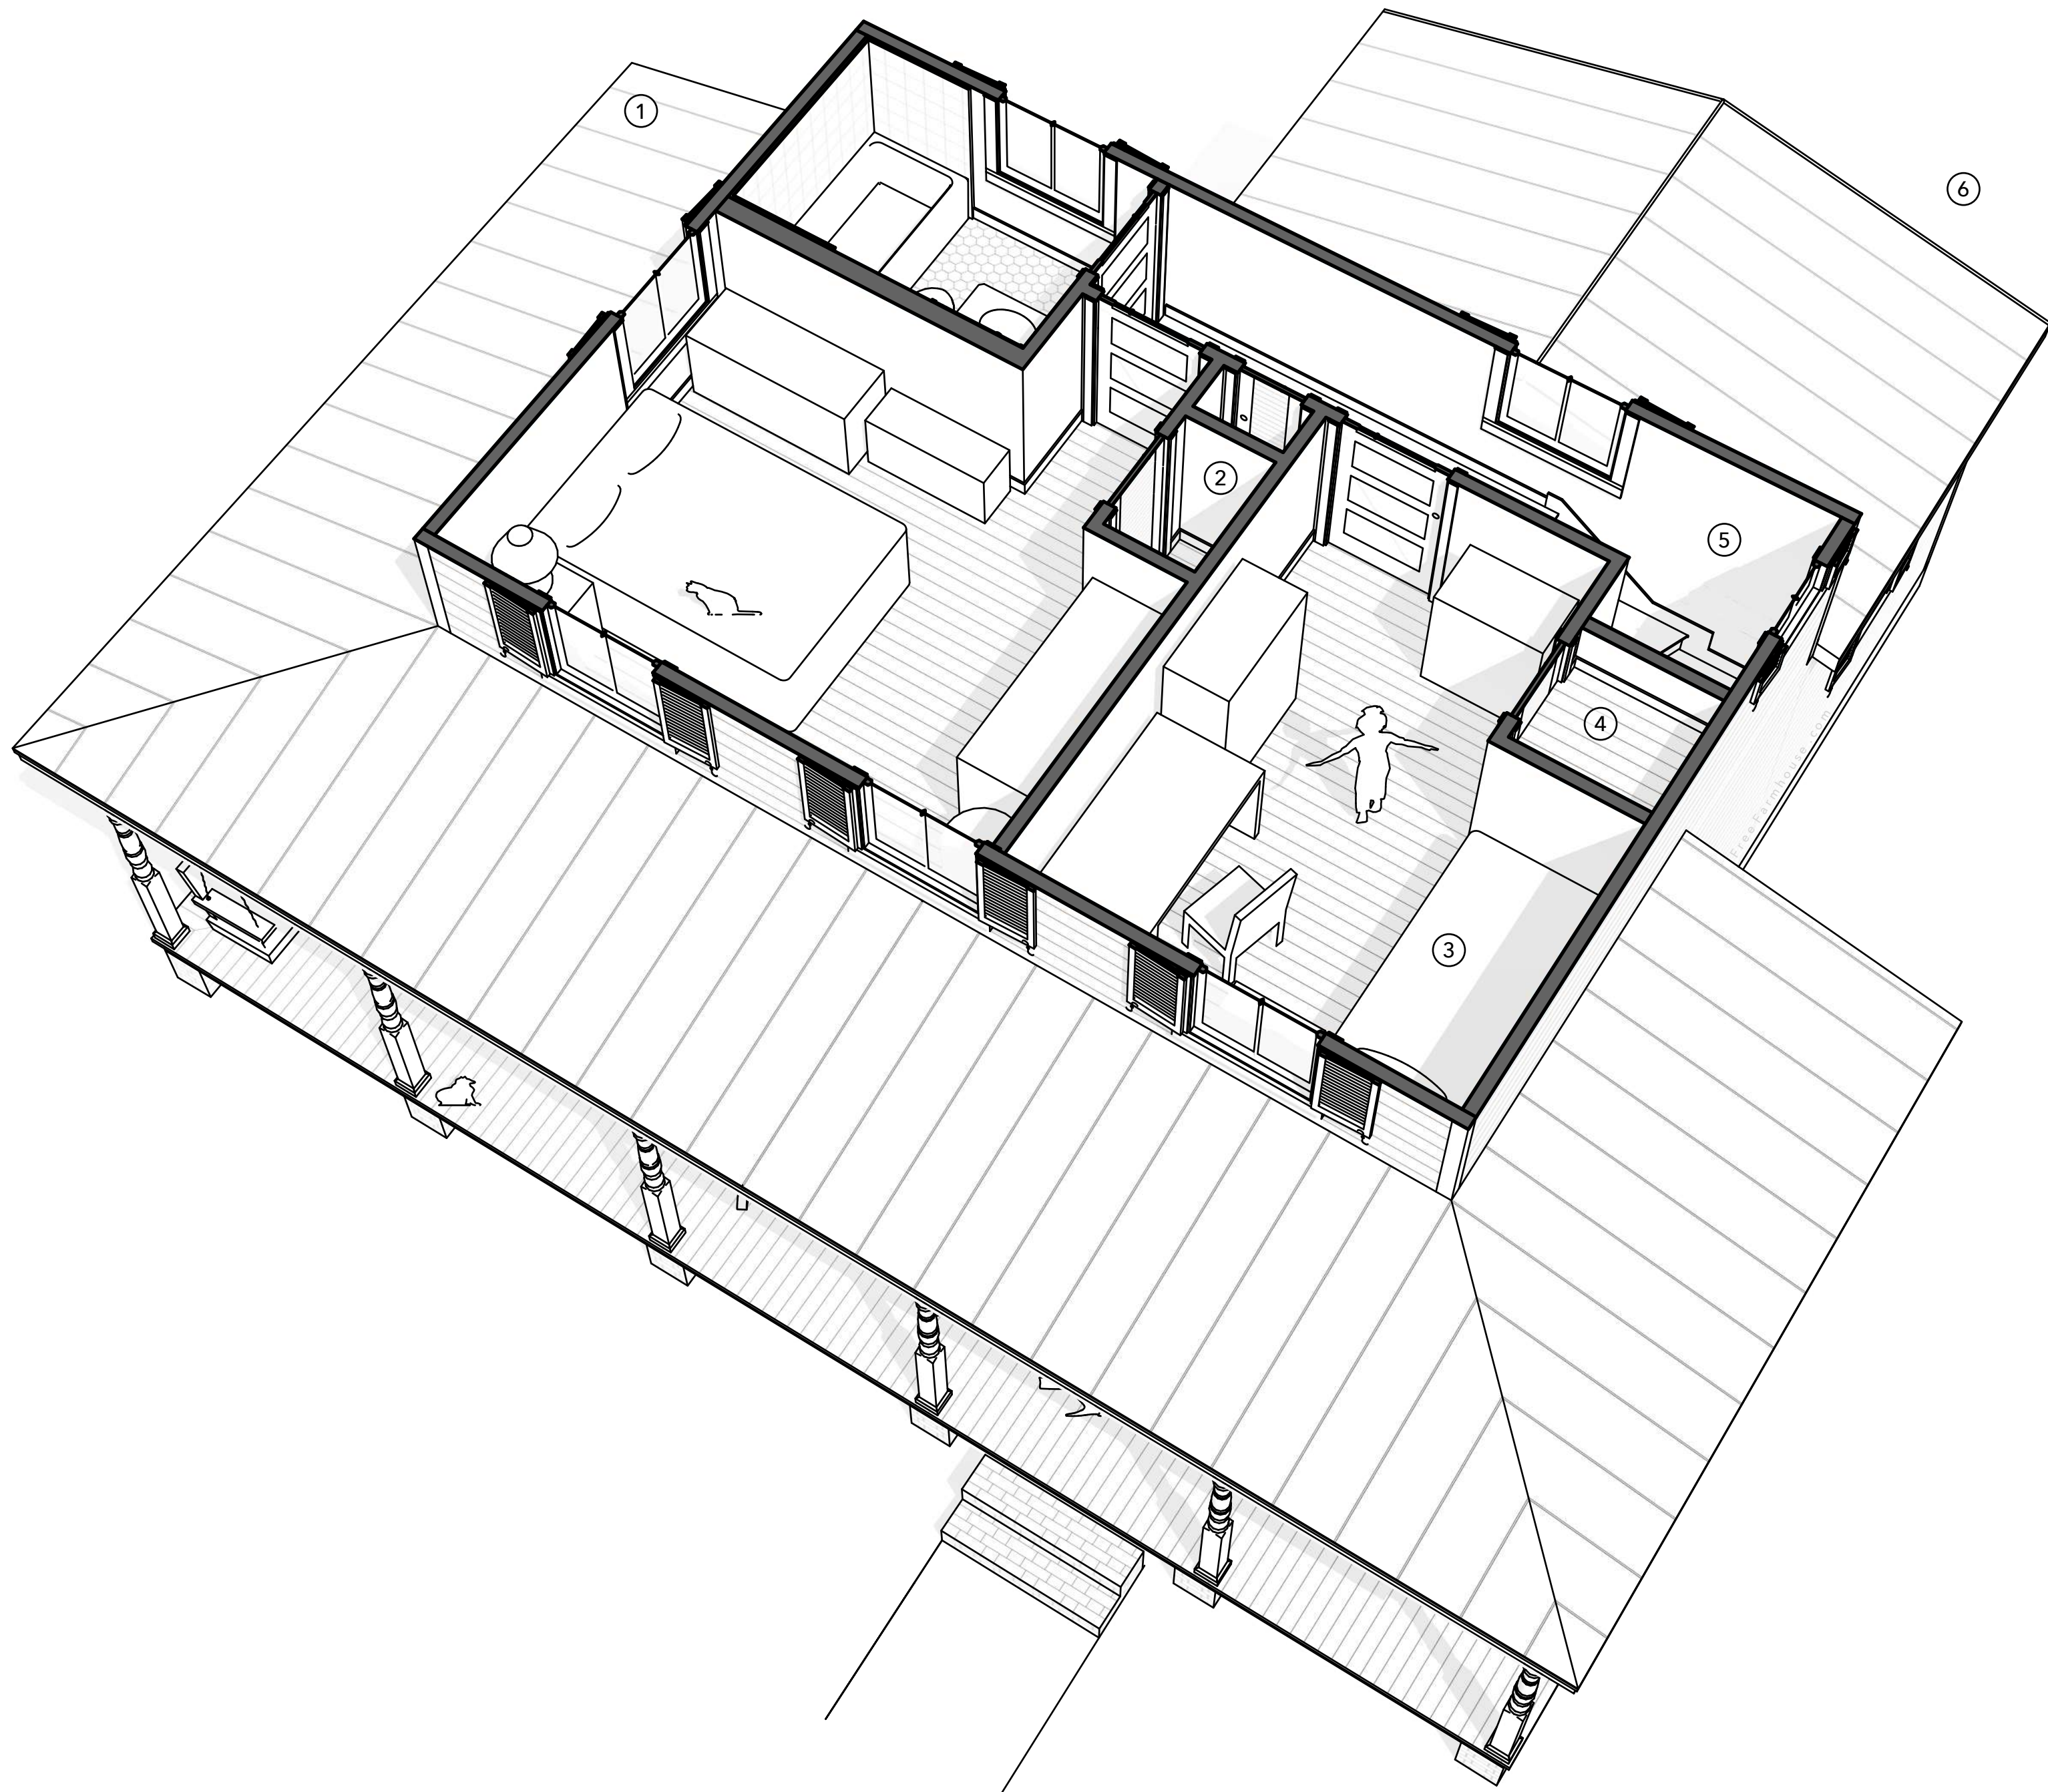

(1) The lower roofs surround the house, but they'd barely be noticeable from upstairs (unless you're standing right next to a window). **(2)** The closets here can be omitted or rearranged, depending on preferences. **(3)** The bedroom alcove needs enough space for a bed (a 7-foot width is required by code). Because of stairway head height minimums, this significantly limits the room size and layout.

CAROLINE'S STARTER FARMHOUSE
UPSTAIRS PLAN
 A DESIGN BY JAY OSBORNE

(4) For stairway head clearances (80" min), this closet needs that raised platform. **(5)** A second window is included above the winder stairs, in case a rear addition is added (which would block the hall's back window). **(6)** The rear kitchen/porch can become a hyphen connecting to a garage. Garages tend to be massive, blocking views and light. A hyphen preserves natural lighting and cross breezes.



Caroline's Farmhouse has a wrap-around porch with many small additions. Though it would look great surrounded by a large field, it could also fit well in a 50-foot diameter forest clearing. The house is simple, economical, and compact.

(1) Real window shutters are functional. If cost is an issue, omit them. No fakes.

(2) The large windows on the lower level still look great if the porch is removed.

CAROLINE'S STARTER FARMHOUSE


FRONT OF THE HOUSE

A DESIGN BY JAY OSBORNE

(3) A note of caution— even though this is perhaps the simplest eave imaginable, builders tend to mangle historical details like this by building “pork chop eaves.”

(4) The porch roof shouldn't be too steep. It may need long gutters, and downspouts at the side rooms.

(5) The porch is low to the ground with only three steps down to avoid railings. Strict codes make traditional railings costly to build.

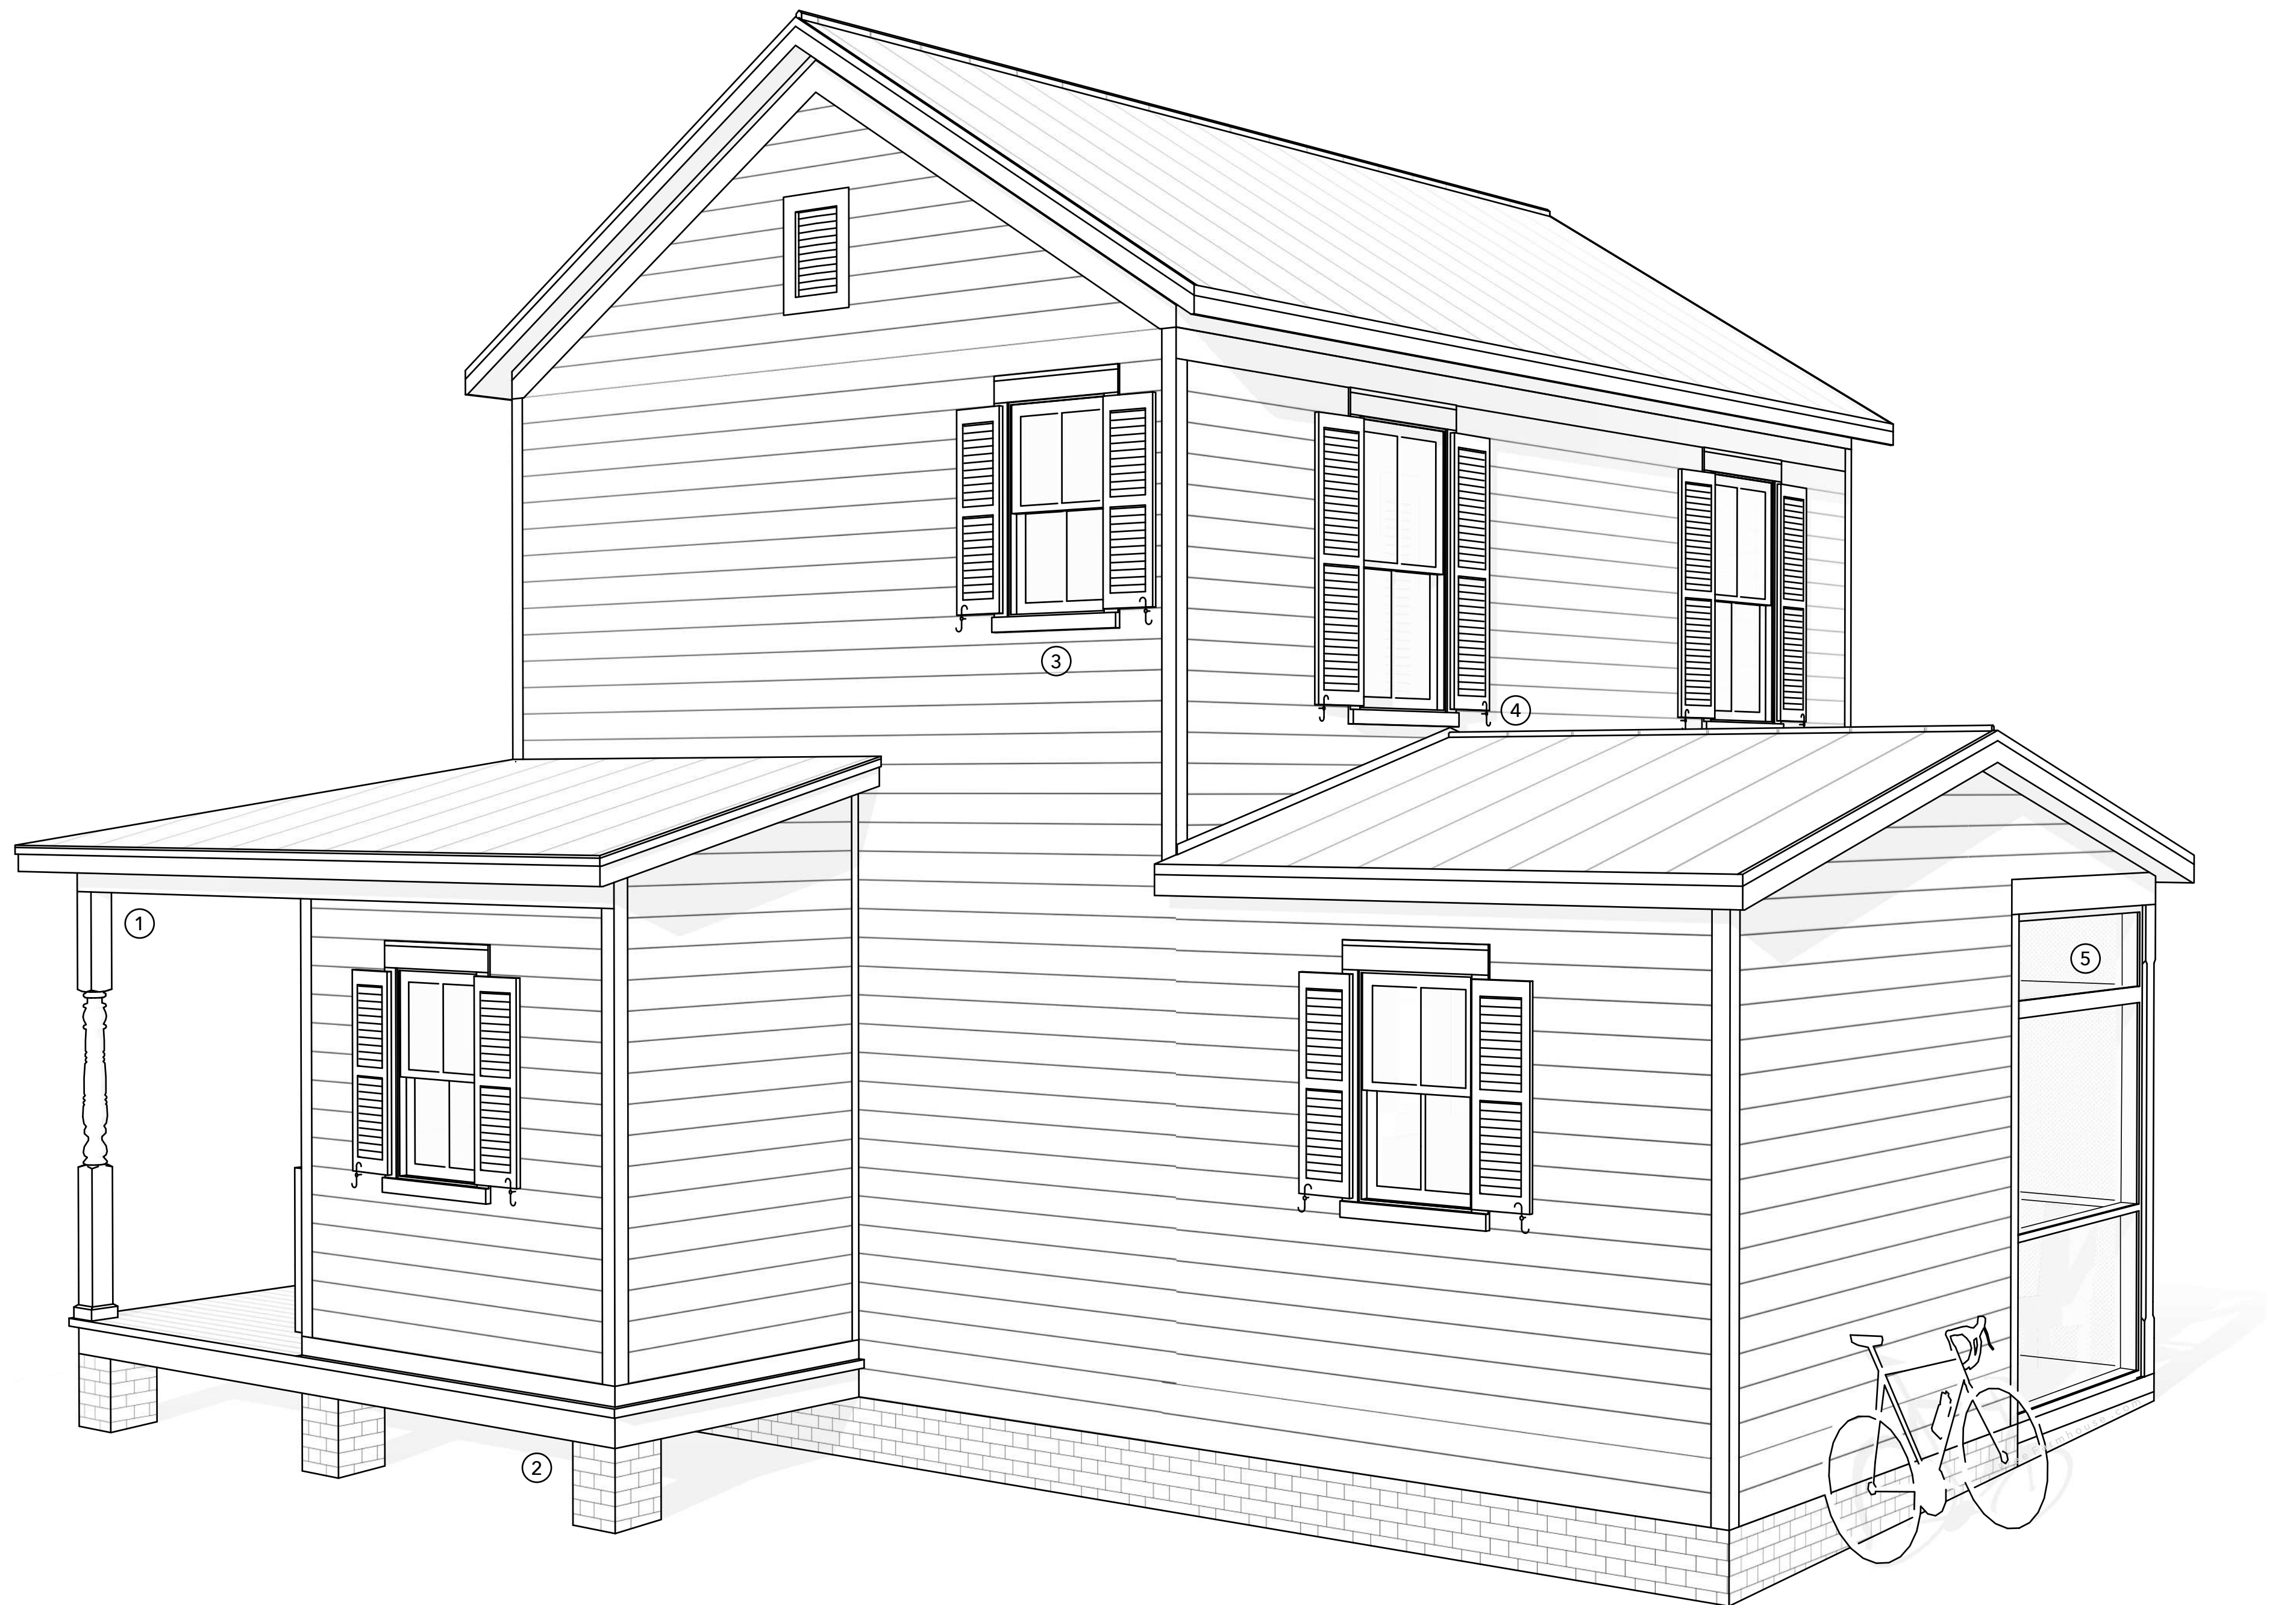

(1) The porch columns could have more gingerbread added to them, perhaps as a future renovation. Such decorations are not easy to add onto normal modern houses. **(2)** The side room additions are designed to look like filled-in porch bays, requiring an insulated and ventilated floor assembly. Overall, it's easy but unconventional. This adds character and a sense of history to the house's design.

CAROLINE'S STARTER FARMHOUSE
BACK OF THE HOUSE
A DESIGN BY JAY OSBORNE


(3) This window could be omitted, but its opening should at least be framed in. That's because, with a rear addition, the window at the upstairs hall would be closed up, making a dark, stuffy space. **(4)** The rear roof can be slightly shallower, to avoid this pinch point. **(5)** The screen porch can function as a mudroom, and can be walled in. This is a potential connection point to a future attached garage.




(1) The porch's open crawlspace can be enclosed with wooden lattice (and a metal screen on the inside). The decking has to be low to avoid the need for a guardrail, but the compromise is that this crawlspace is tiny. **(2)** You can have a basement instead of a conditioned crawlspace. Put the basement stairs directly under the other stairs. **(3)** The open living area has many possible arrangements.

CAROLINE'S STARTER FARMHOUSE
SECTION PERSPECTIVE
 A DESIGN BY JAY OSBORNE

(4) The roof can be framed with normal trusses. The slope corresponds to historical roof pitches. Making it shallower could reduce its old fashioned charm. **(5)** The kitchen has space for open shelves or narrow cabinets, which work great as pantries. **(6)** The kitchen has many windows to improve the daylighting and cross breezes. Balanced light sources make a space feel more cozy and inviting.

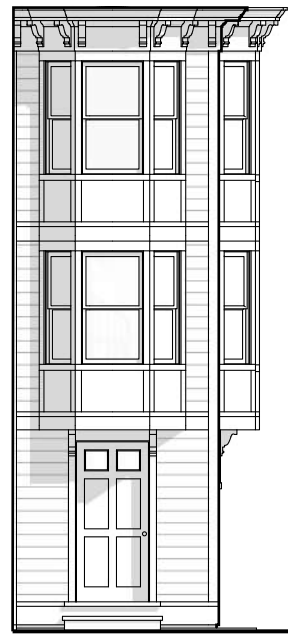

Bicycle
Townhouse

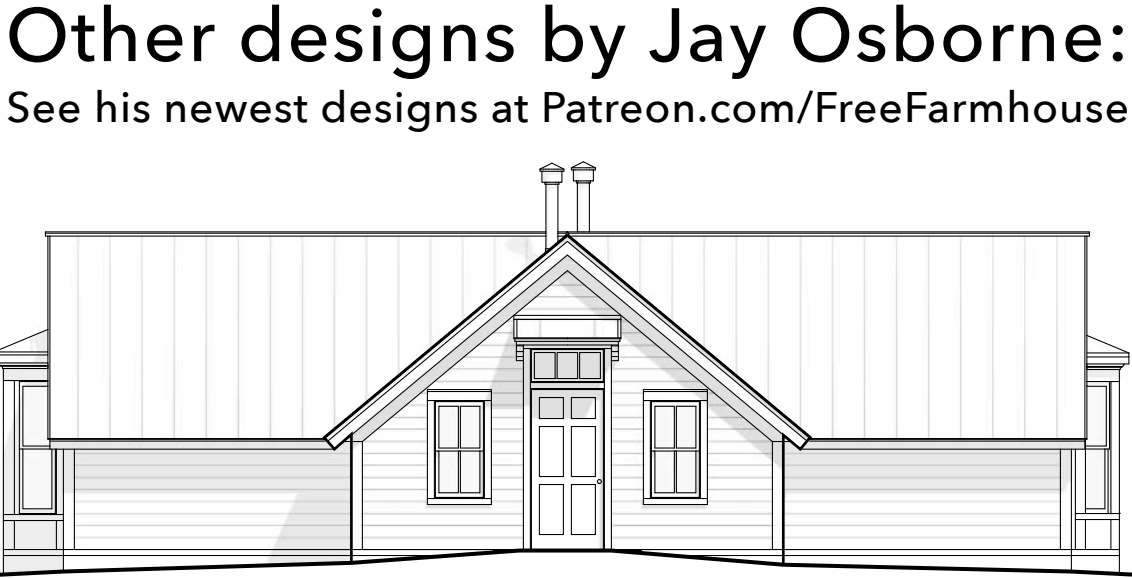

First Halfstory House



Canadian Farmhouse




Mae's Backyard Farmhouse



Julie's Backyard Farmhouse



Australian Farmhouse

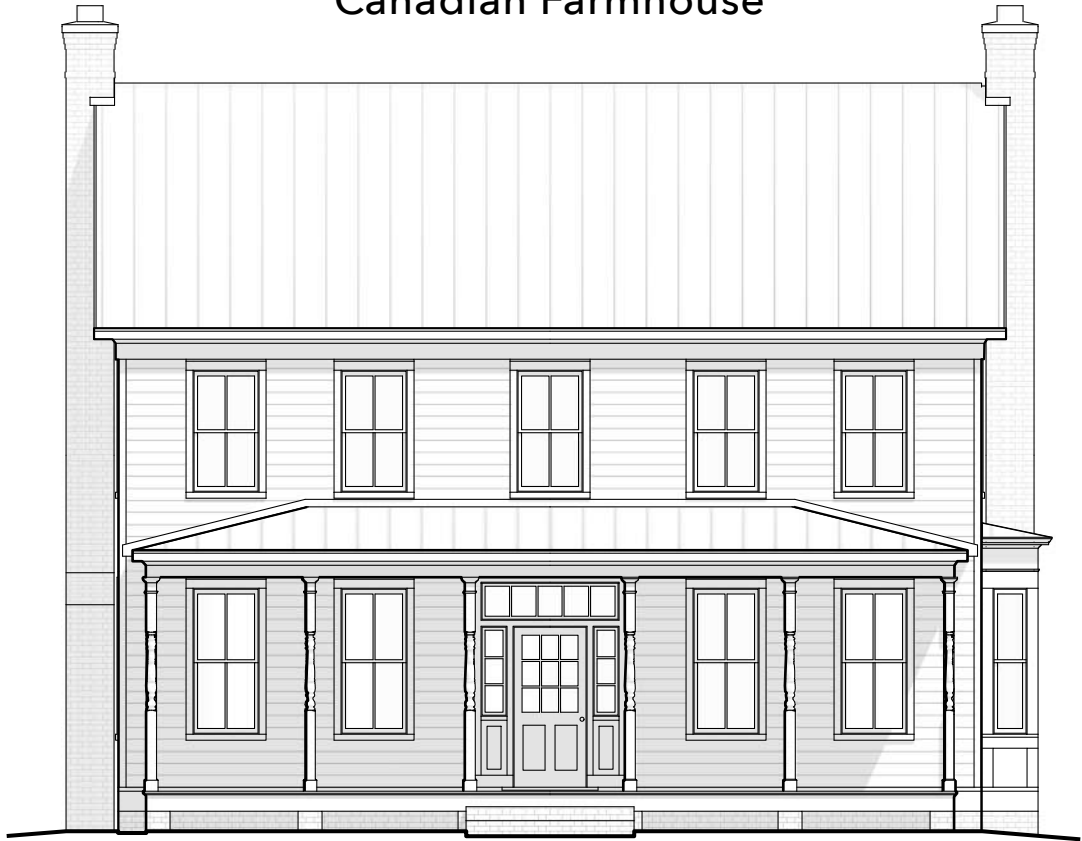

Eastern Farmhouse



April's Backyard Farmhouse



June's Backyard Farmhouse



Southern Farmhouse



Thoreau Cabin



Lone Star Farmhouse



Western Farmhouse



Virginia's Starter Farmhouse



Georgia's Starter Farmhouse



Caroline's Starter Farmhouse



Marilyn's Starter Farmhouse



Carriage House